




SYMBL.	DIS.	PLANT NAME	HGT.
	T1	Delonix Regia	7.0m
	T2	Acacia Arabica	5.0m
	T3	Washingtonia Robusta	15.0m
	T4	Parkinsonia Aculeata	1.0m


No.	REMARKS
1	CEMENT TILES
2	INTERLOCKING TILES 8 CM th.
3	ASPHALT ROAD
4	GREEN AREA

Type	W	H	Specifications
G1	6.8	2.2	Steel Flush Door with Glass Panel (four Leaf)
G2	5.7	2.2	Steel Flush Door with Glass Panel (double Leaf)

GROUND FLOOR
SCALE 1:50

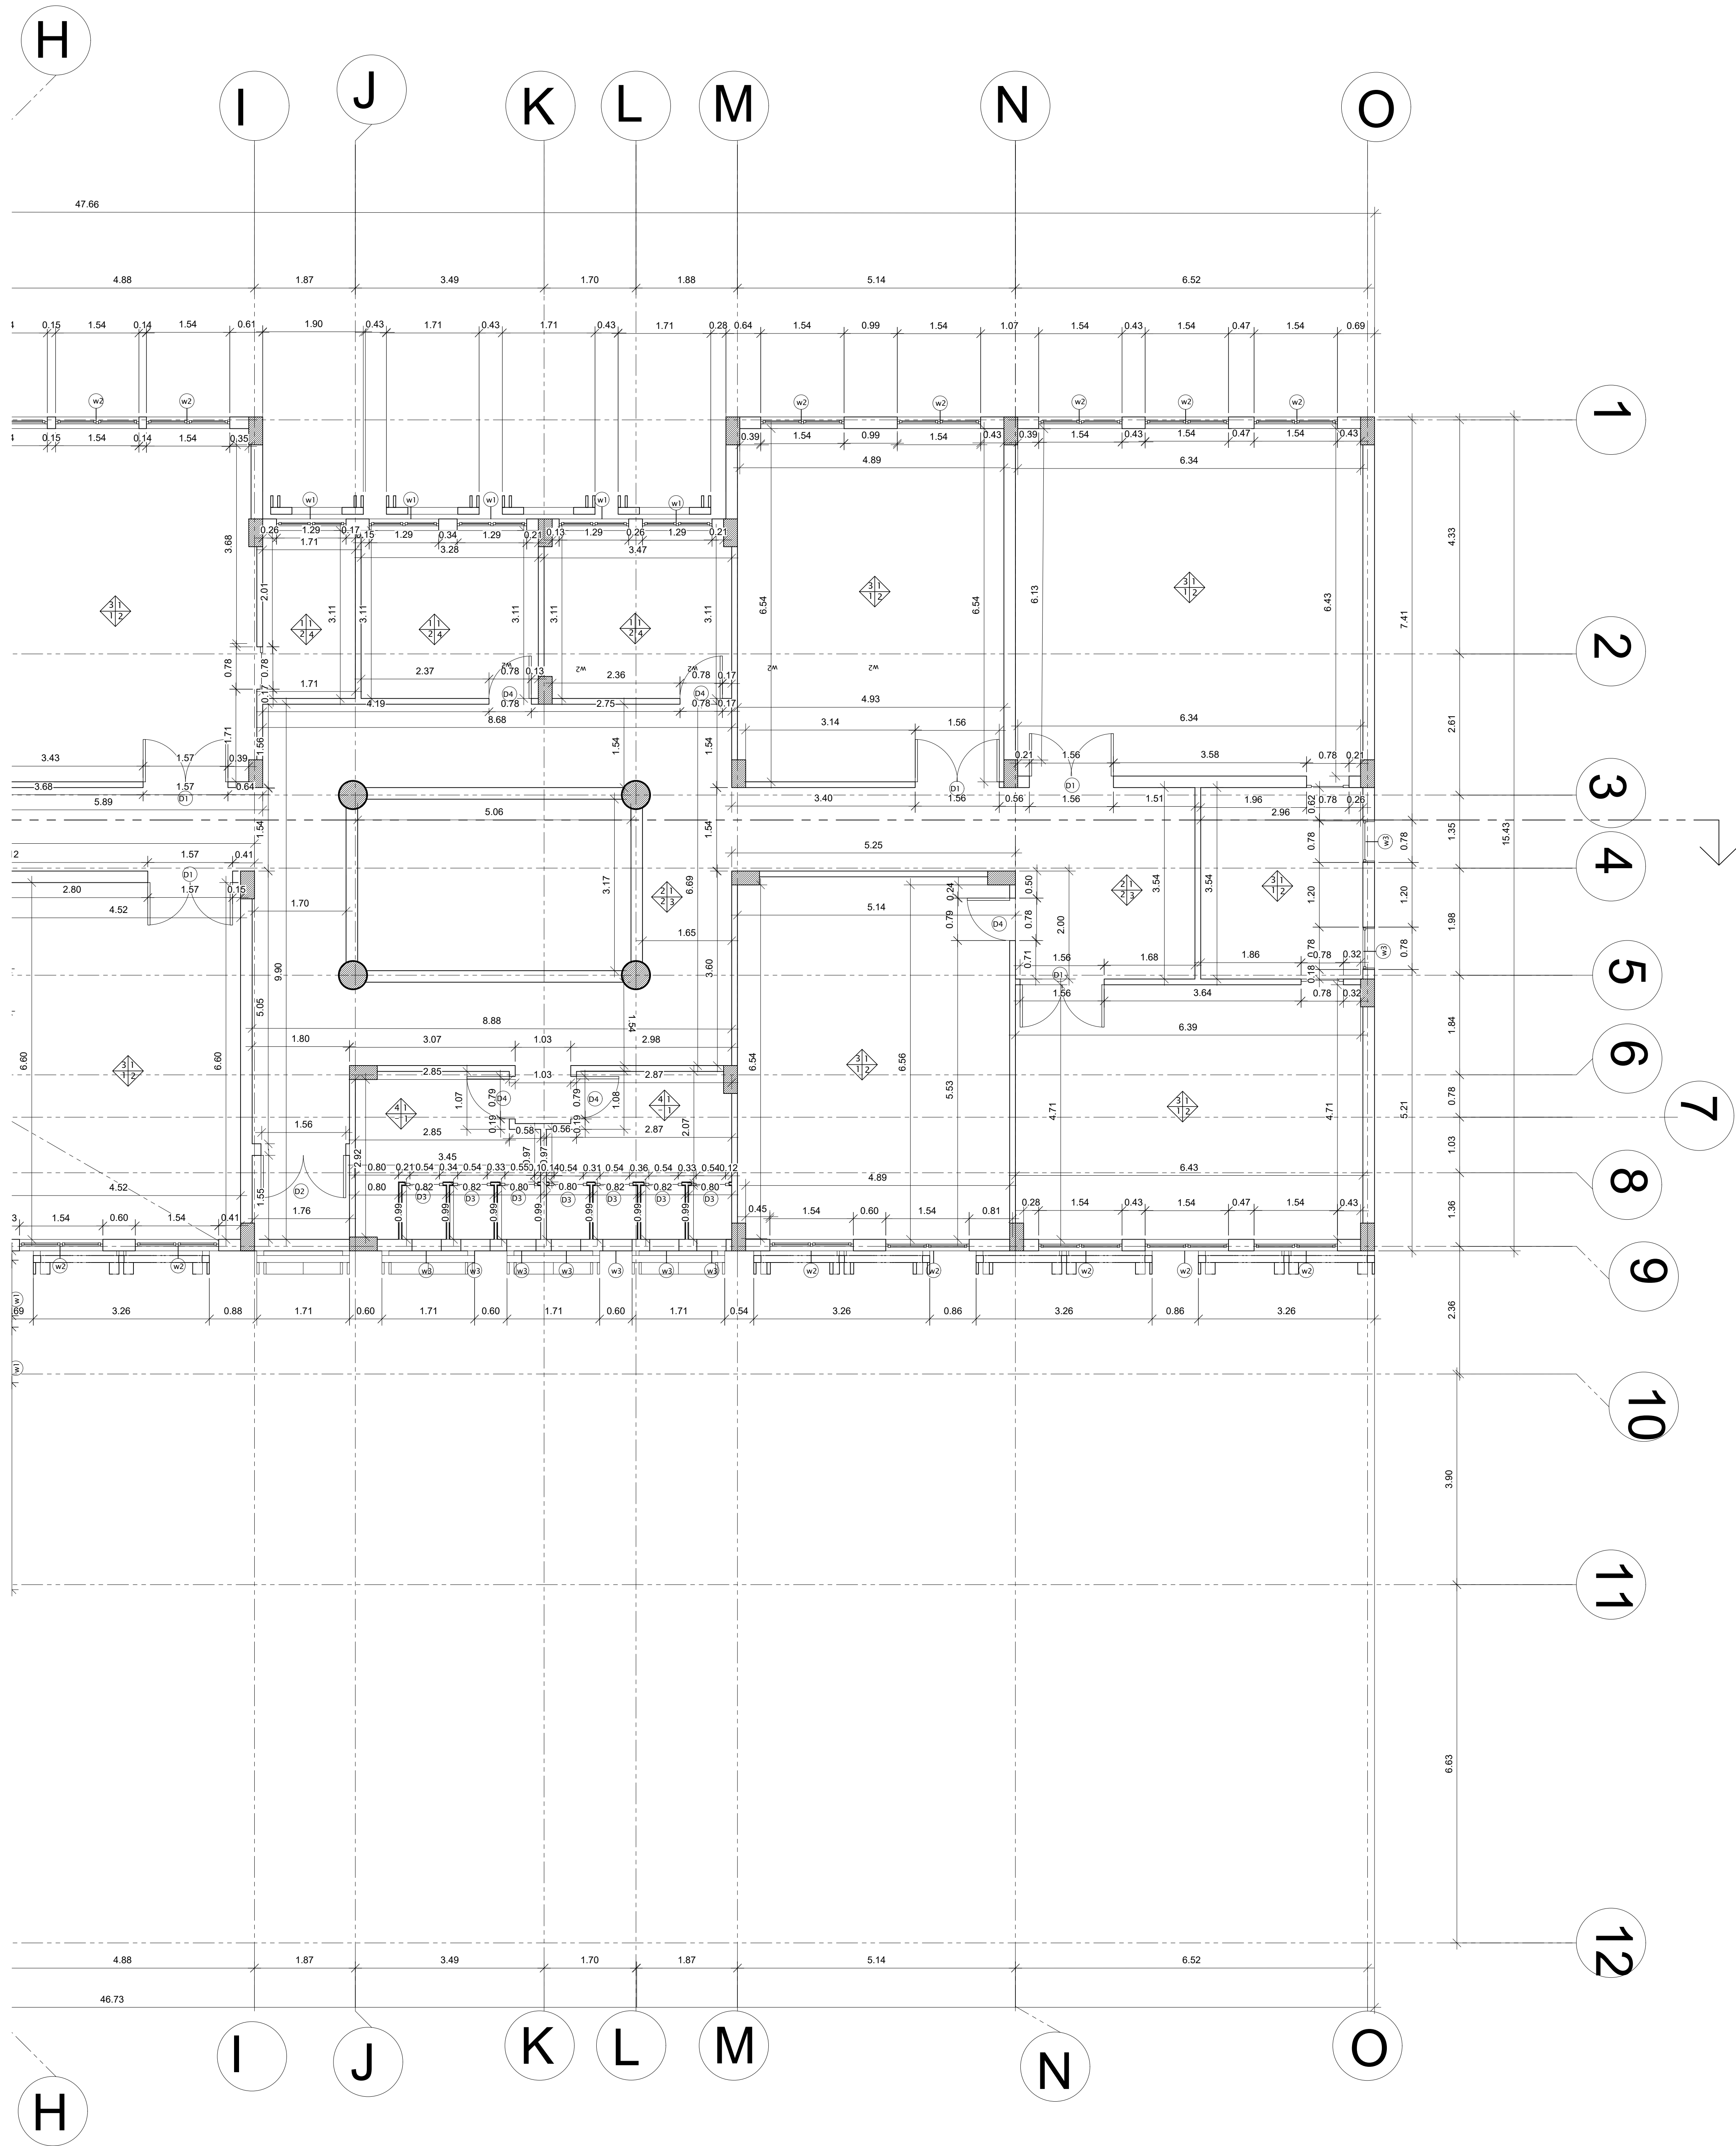

NORTH

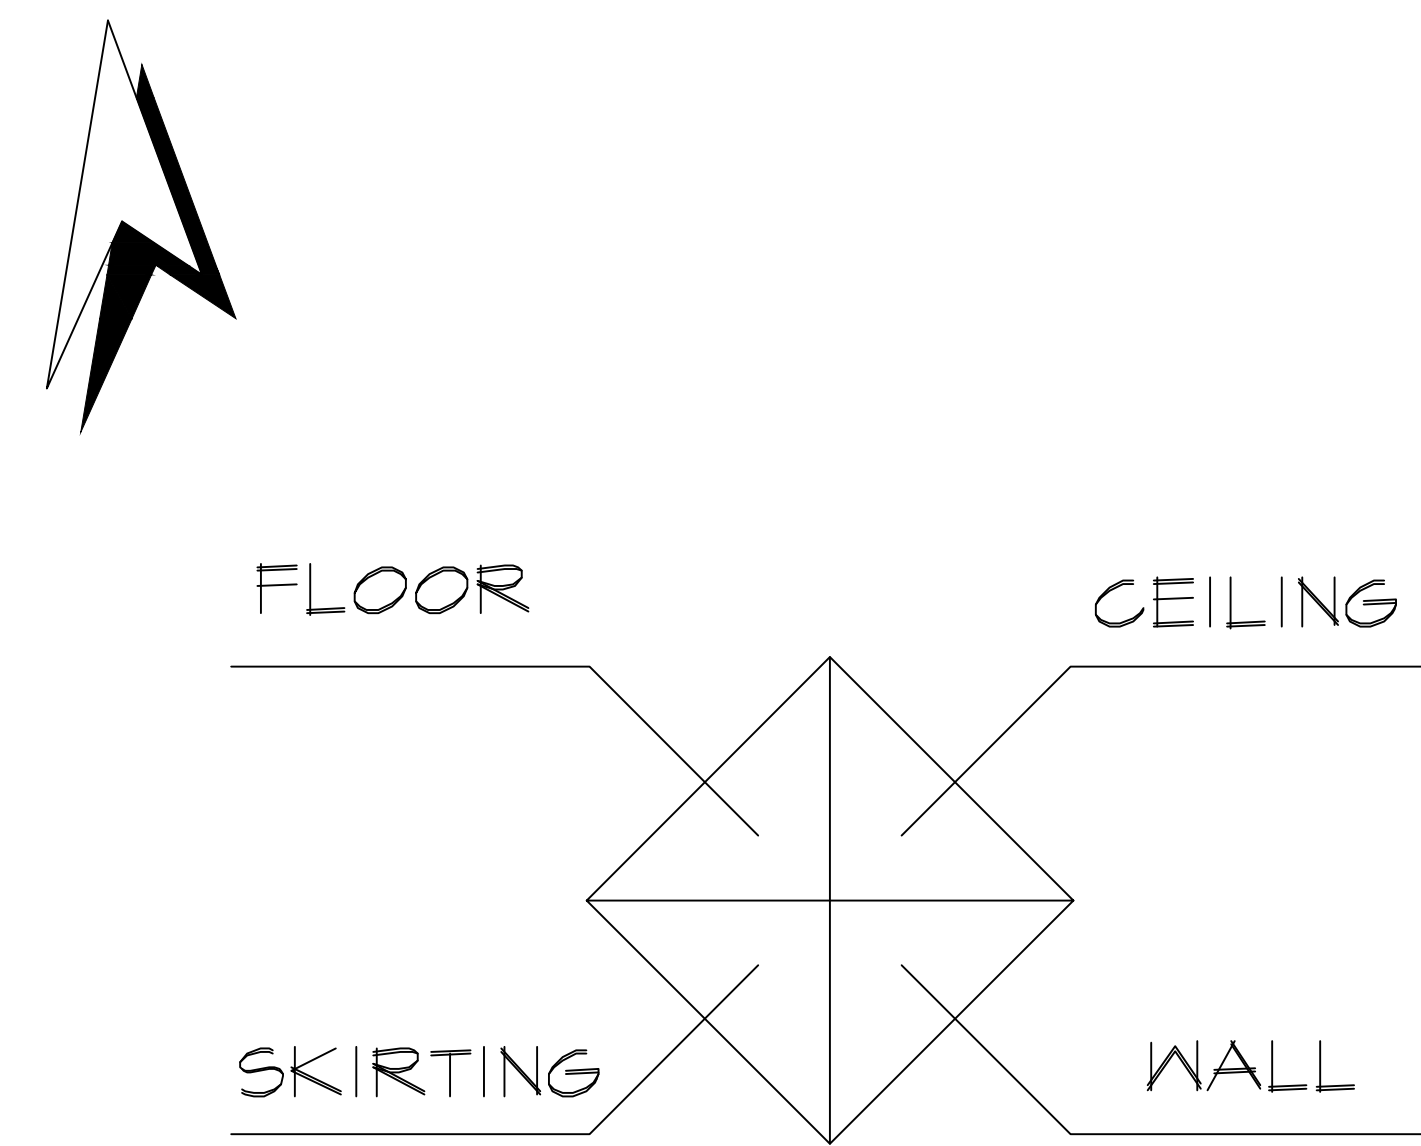

Door schedule				
type mark	count	width	Height	Description
D1	14	1.70m	2.2m	hinged door two sides wooden laminated
D2	4	1.70m	2.2m	hinged door two sides aluminum and glass system
D3	13	0.60m	2.2m	hinged door one side contar clading suiting partitions
D4	16	0.90m	2.2m	hinged door one side wooden laminated

Window schedule					
type mark	count	width	Height	sill Height	Description
W1	14	1.2m	1.50m	1m	fixed one sidesaluminum and glass system
W2	18	1.7m	1.50m	1m	hinged two sides aluminum and glass system
W3	16	.06m	1m	1.4m	hinged one side aluminum and glass system

wall	
no.	Description
1	glossy porcelain ceramic tiles 40*40cm
2	antiviral multifunctional water paint green color
3	antiviral multifunctional water paint white color
4	wooden cladding 60cm

floor	
no.	Description
1	glossy porcelain ceramic tiles 40*40cm
2	granite tiles 40*40cm
3	vinyl anti-static rolls 3mm
4	ceramic tiles 40*40 cm


skirting	
no.	Description
1	ceramic 15cm
2	carrara marble cladding panels 2.2*0.1*0.1m


ceiling	
no.	Description
1	antiviral multifunctional water paint white color
2	gypsum board false ceiling acoustical absorption
3	halcyon acoustical absorption white color

Abdul rahman Ashraf


DR. MOHAMED AISAEED

GROUND FLOOR
SCALE 1:50

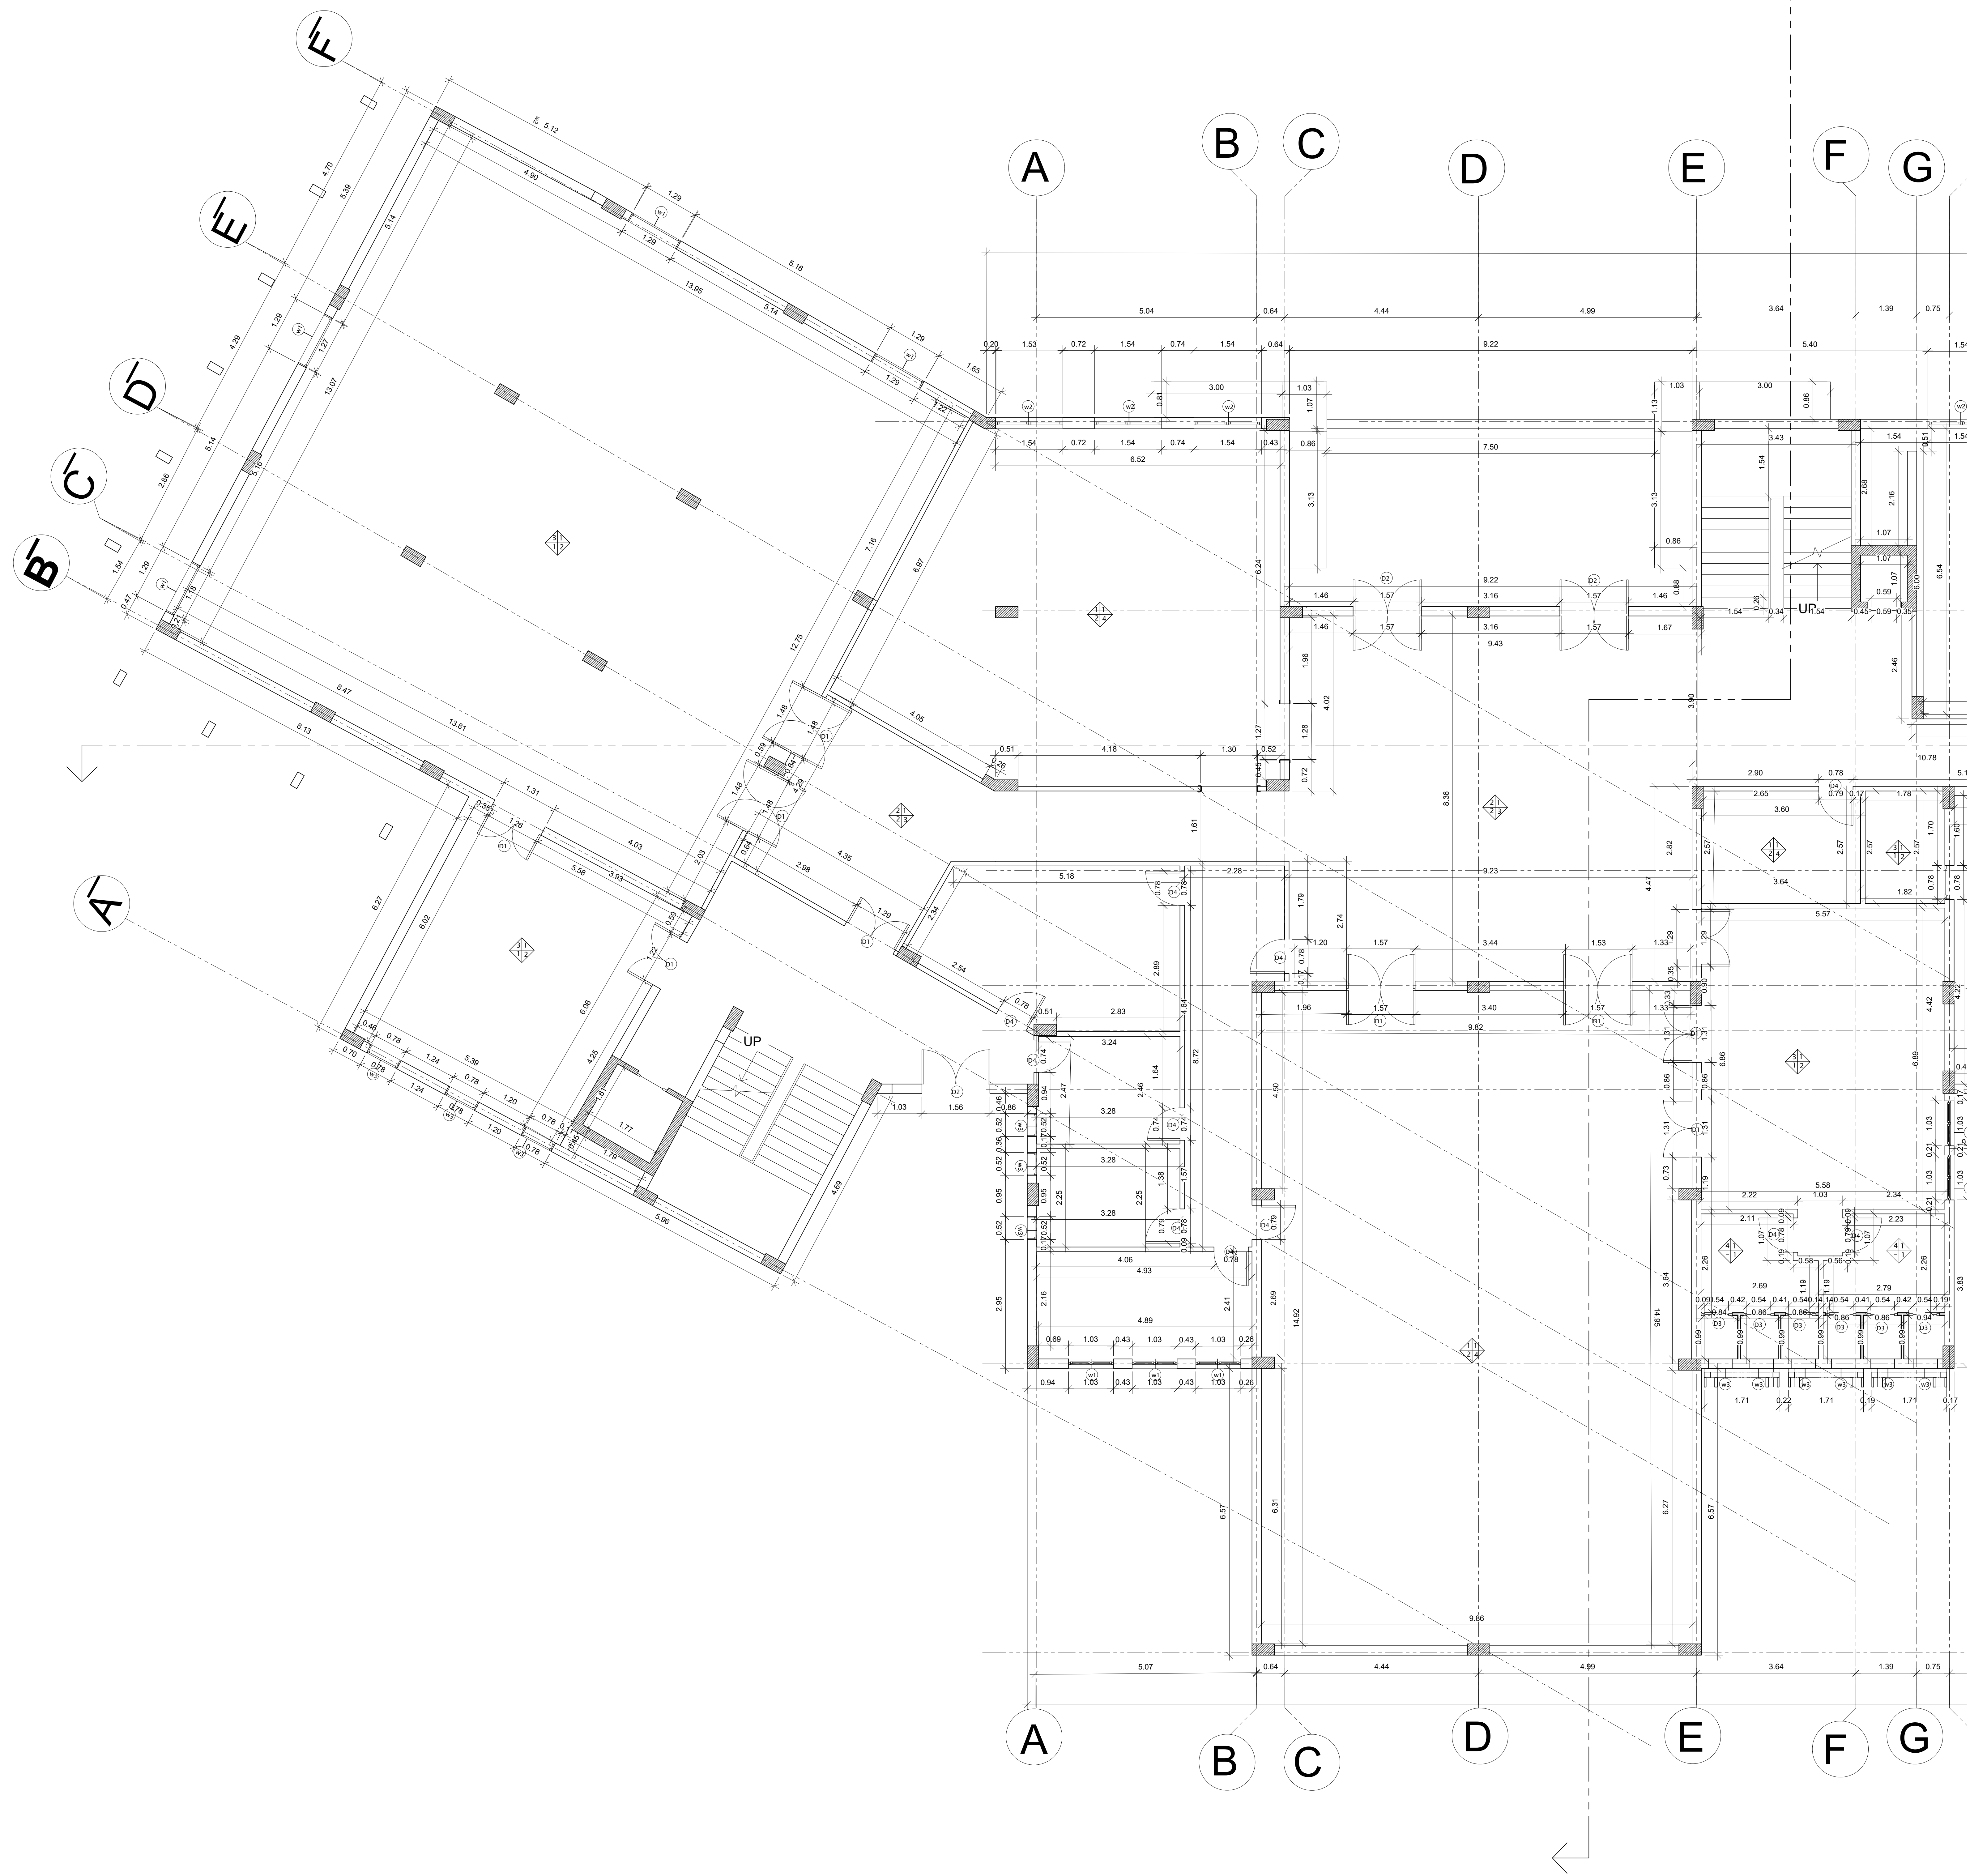

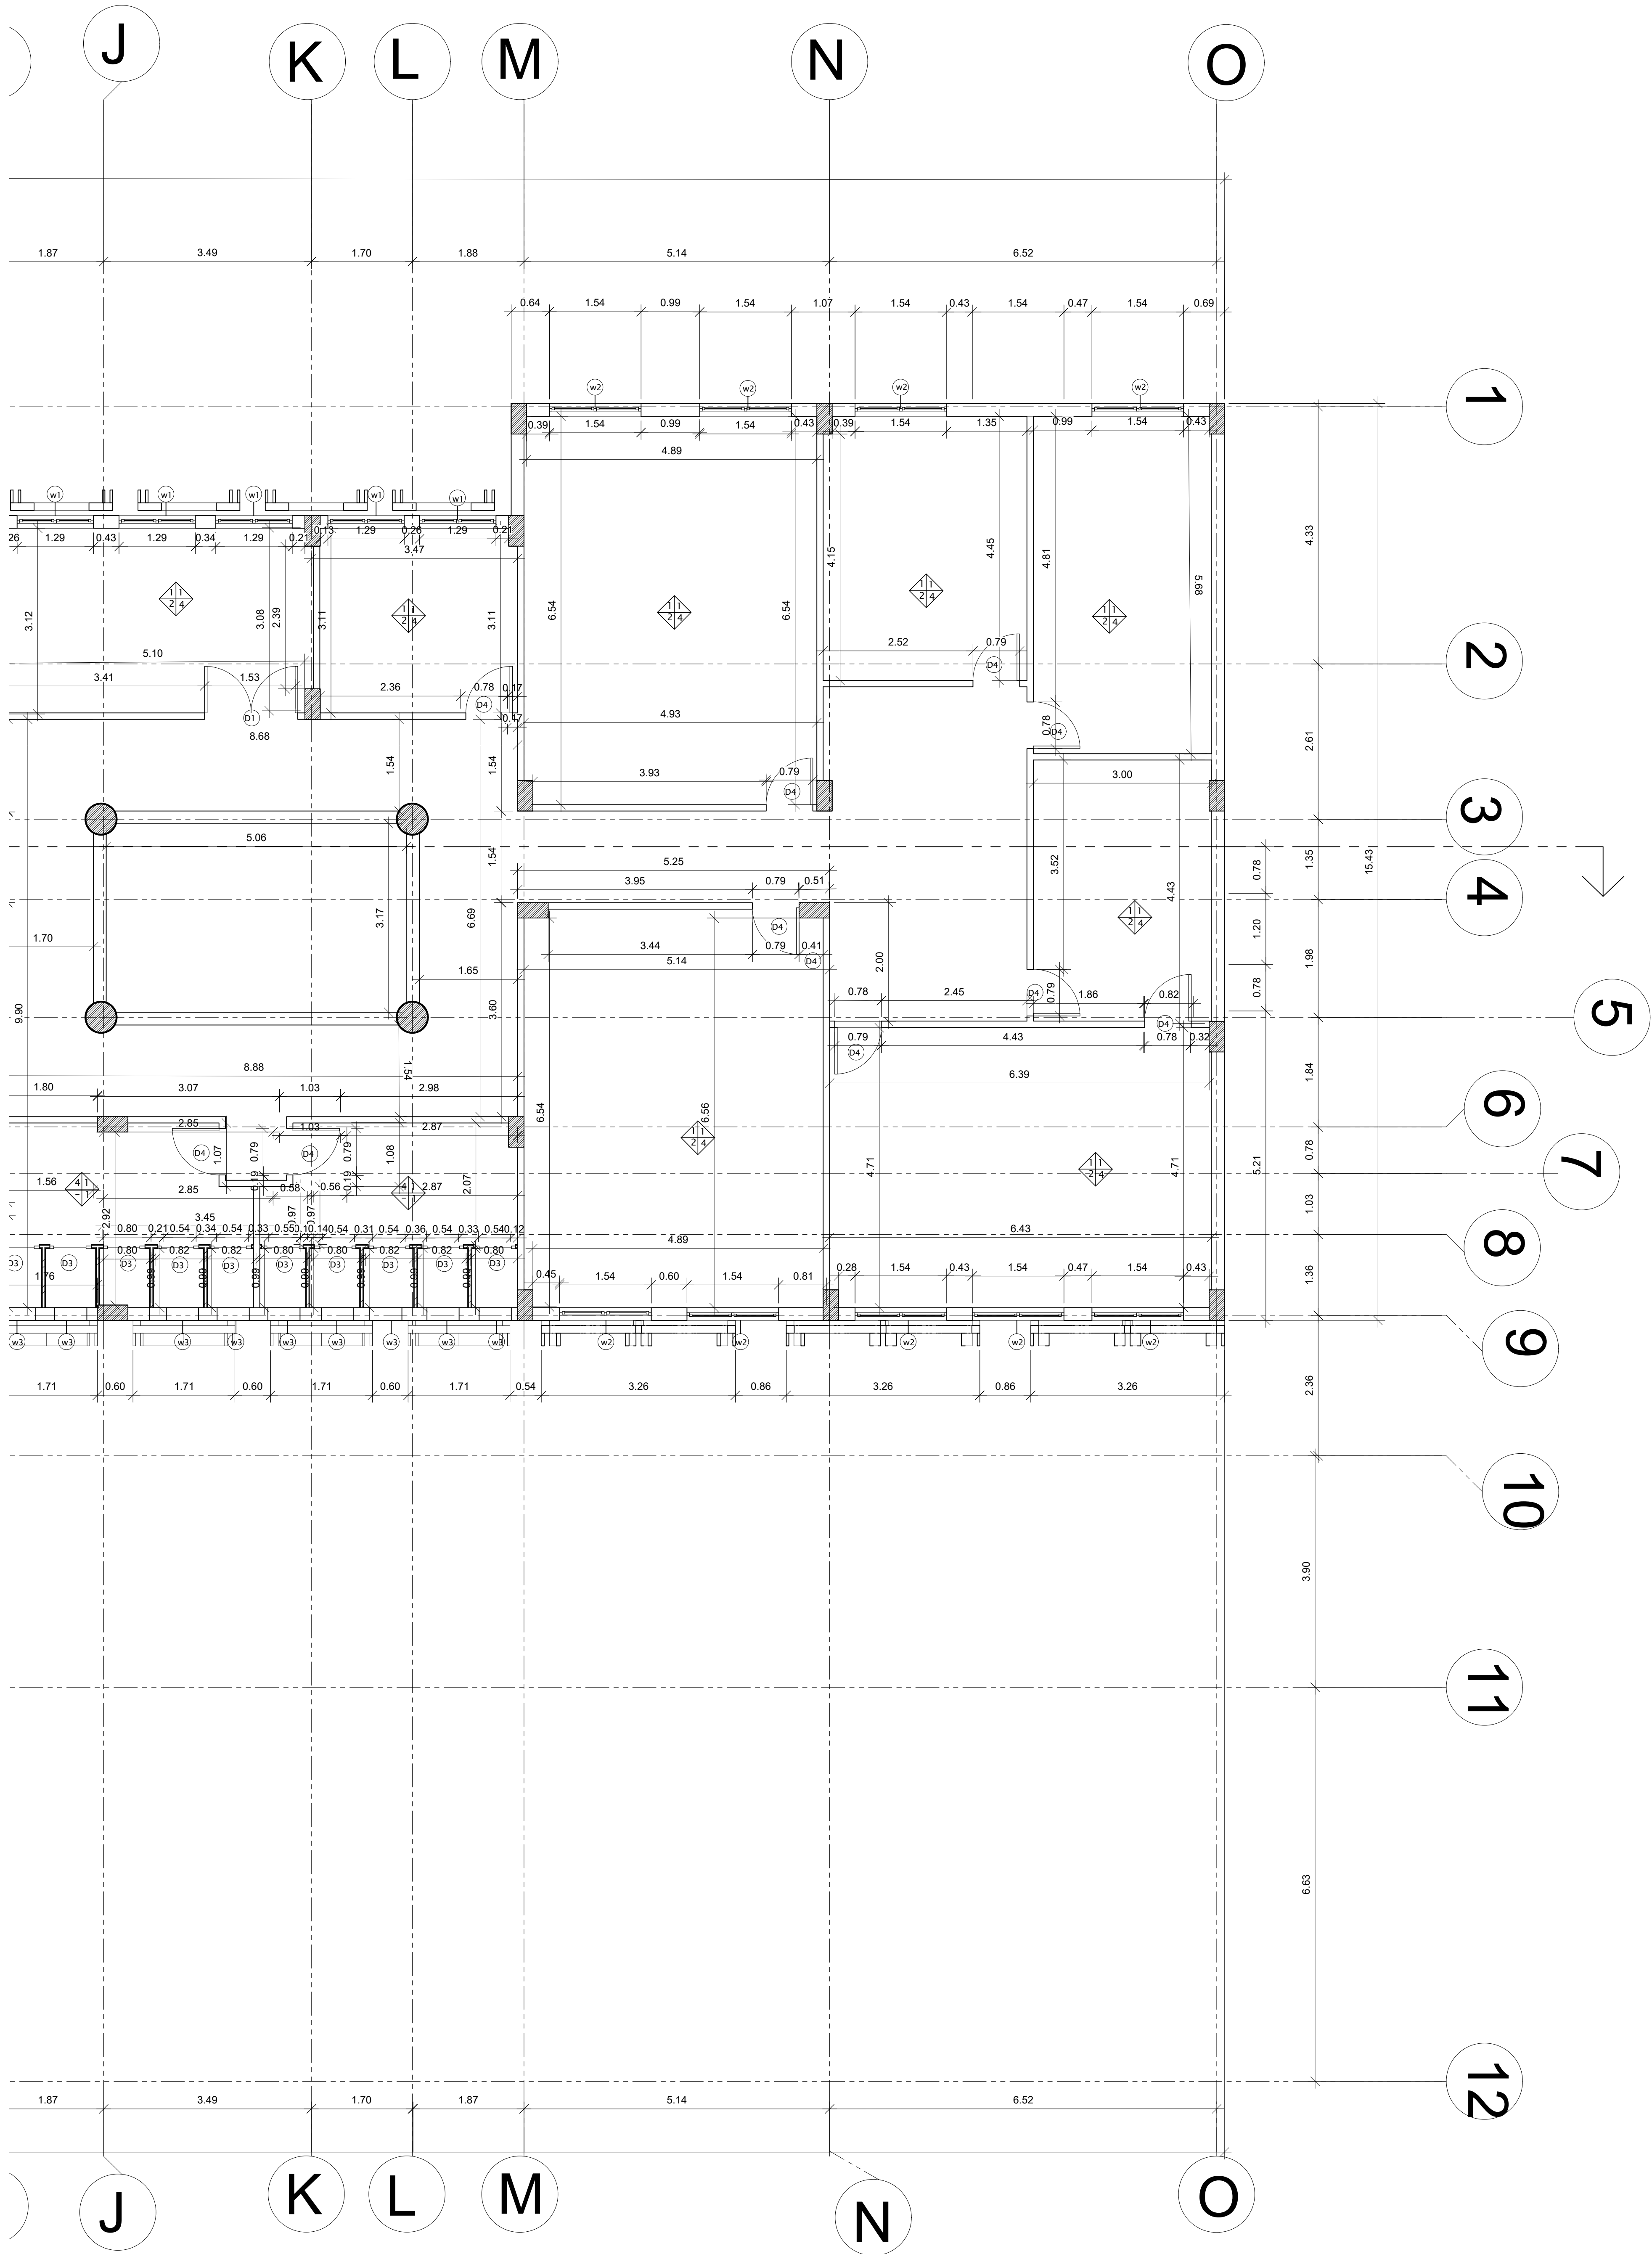

NORTH

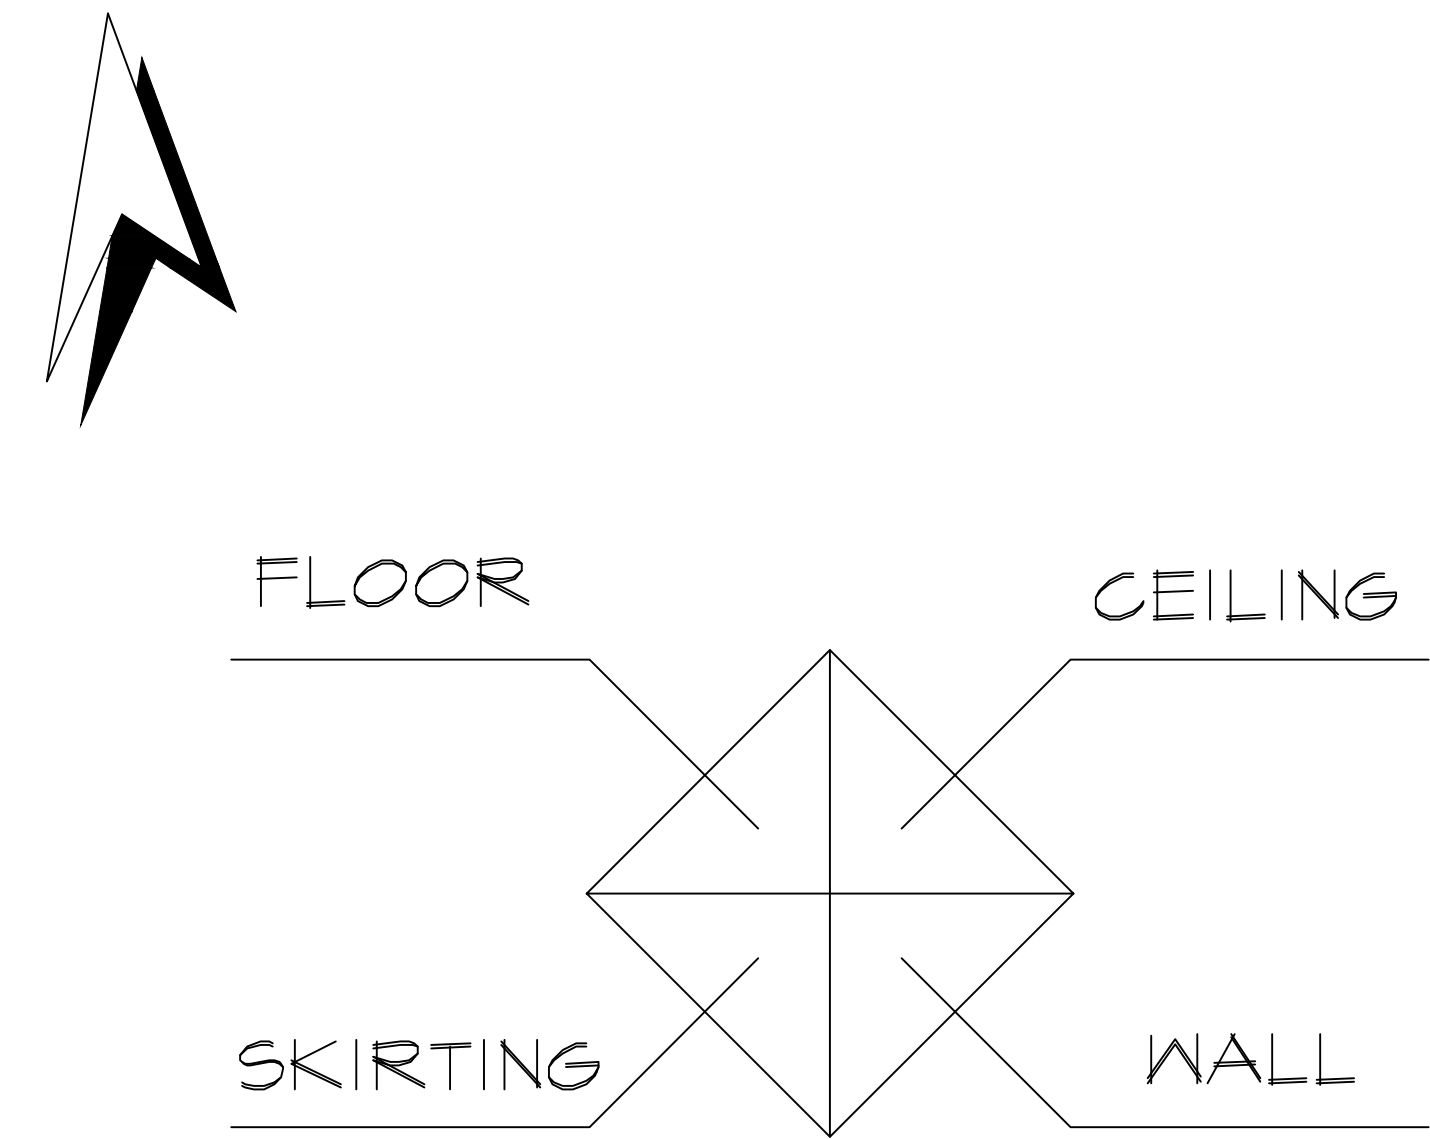

Door schedule				
type mark	count	width	Height	Description
D1	14	1.70m	2.2m	hinged door two sides wooden laminated
D2	4	1.70m	2.2m	hinged door two sides aluminum and glass system
D3	13	0.60m	2.2m	hinged door one side contar clading suiting partitions
D4	16	0.90m	2.2m	hinged door one side wooden laminated

Window schedule					
type mark	count	width	Height	sill Height	Description
W1	14	1.2m	1.50m	1m	fixed one sidesaluminum and glass system
W2	18	1.7m	1.50m	1m	hinged two sides aluminum and glass system
W3	16	.06m	1m	1.4m	hinged one side aluminum and glass system

wall	
no.	Description
1	glossy porcelain ceramic tiles 40*40cm
2	antiviral multifunctional water paint green color
3	antiviral multifunctional water paint white color
4	wooden cladding 60cm

floor	
no.	Description
1	glossy porcelain ceramic tiles 40*40cm
2	granite tiles 40*40cm
3	vinyl anti-static rolls 3mm
4	ceramic tiles 40*40 cm


skirting	
no.	Description
1	ceramic 15cm
2	carrara marble cladding panels 2.2*0.1*0.1m


ceiling	
no.	Description
1	antiviral multifunctional water paint white color
2	gypsum board false ceiling acoustical absorption
3	halcyon acoustical absorption white color

Abdul rahman Ashraf

DR. MOHAMED AISAEED

GROUND FLOOR
SCALE 1:50


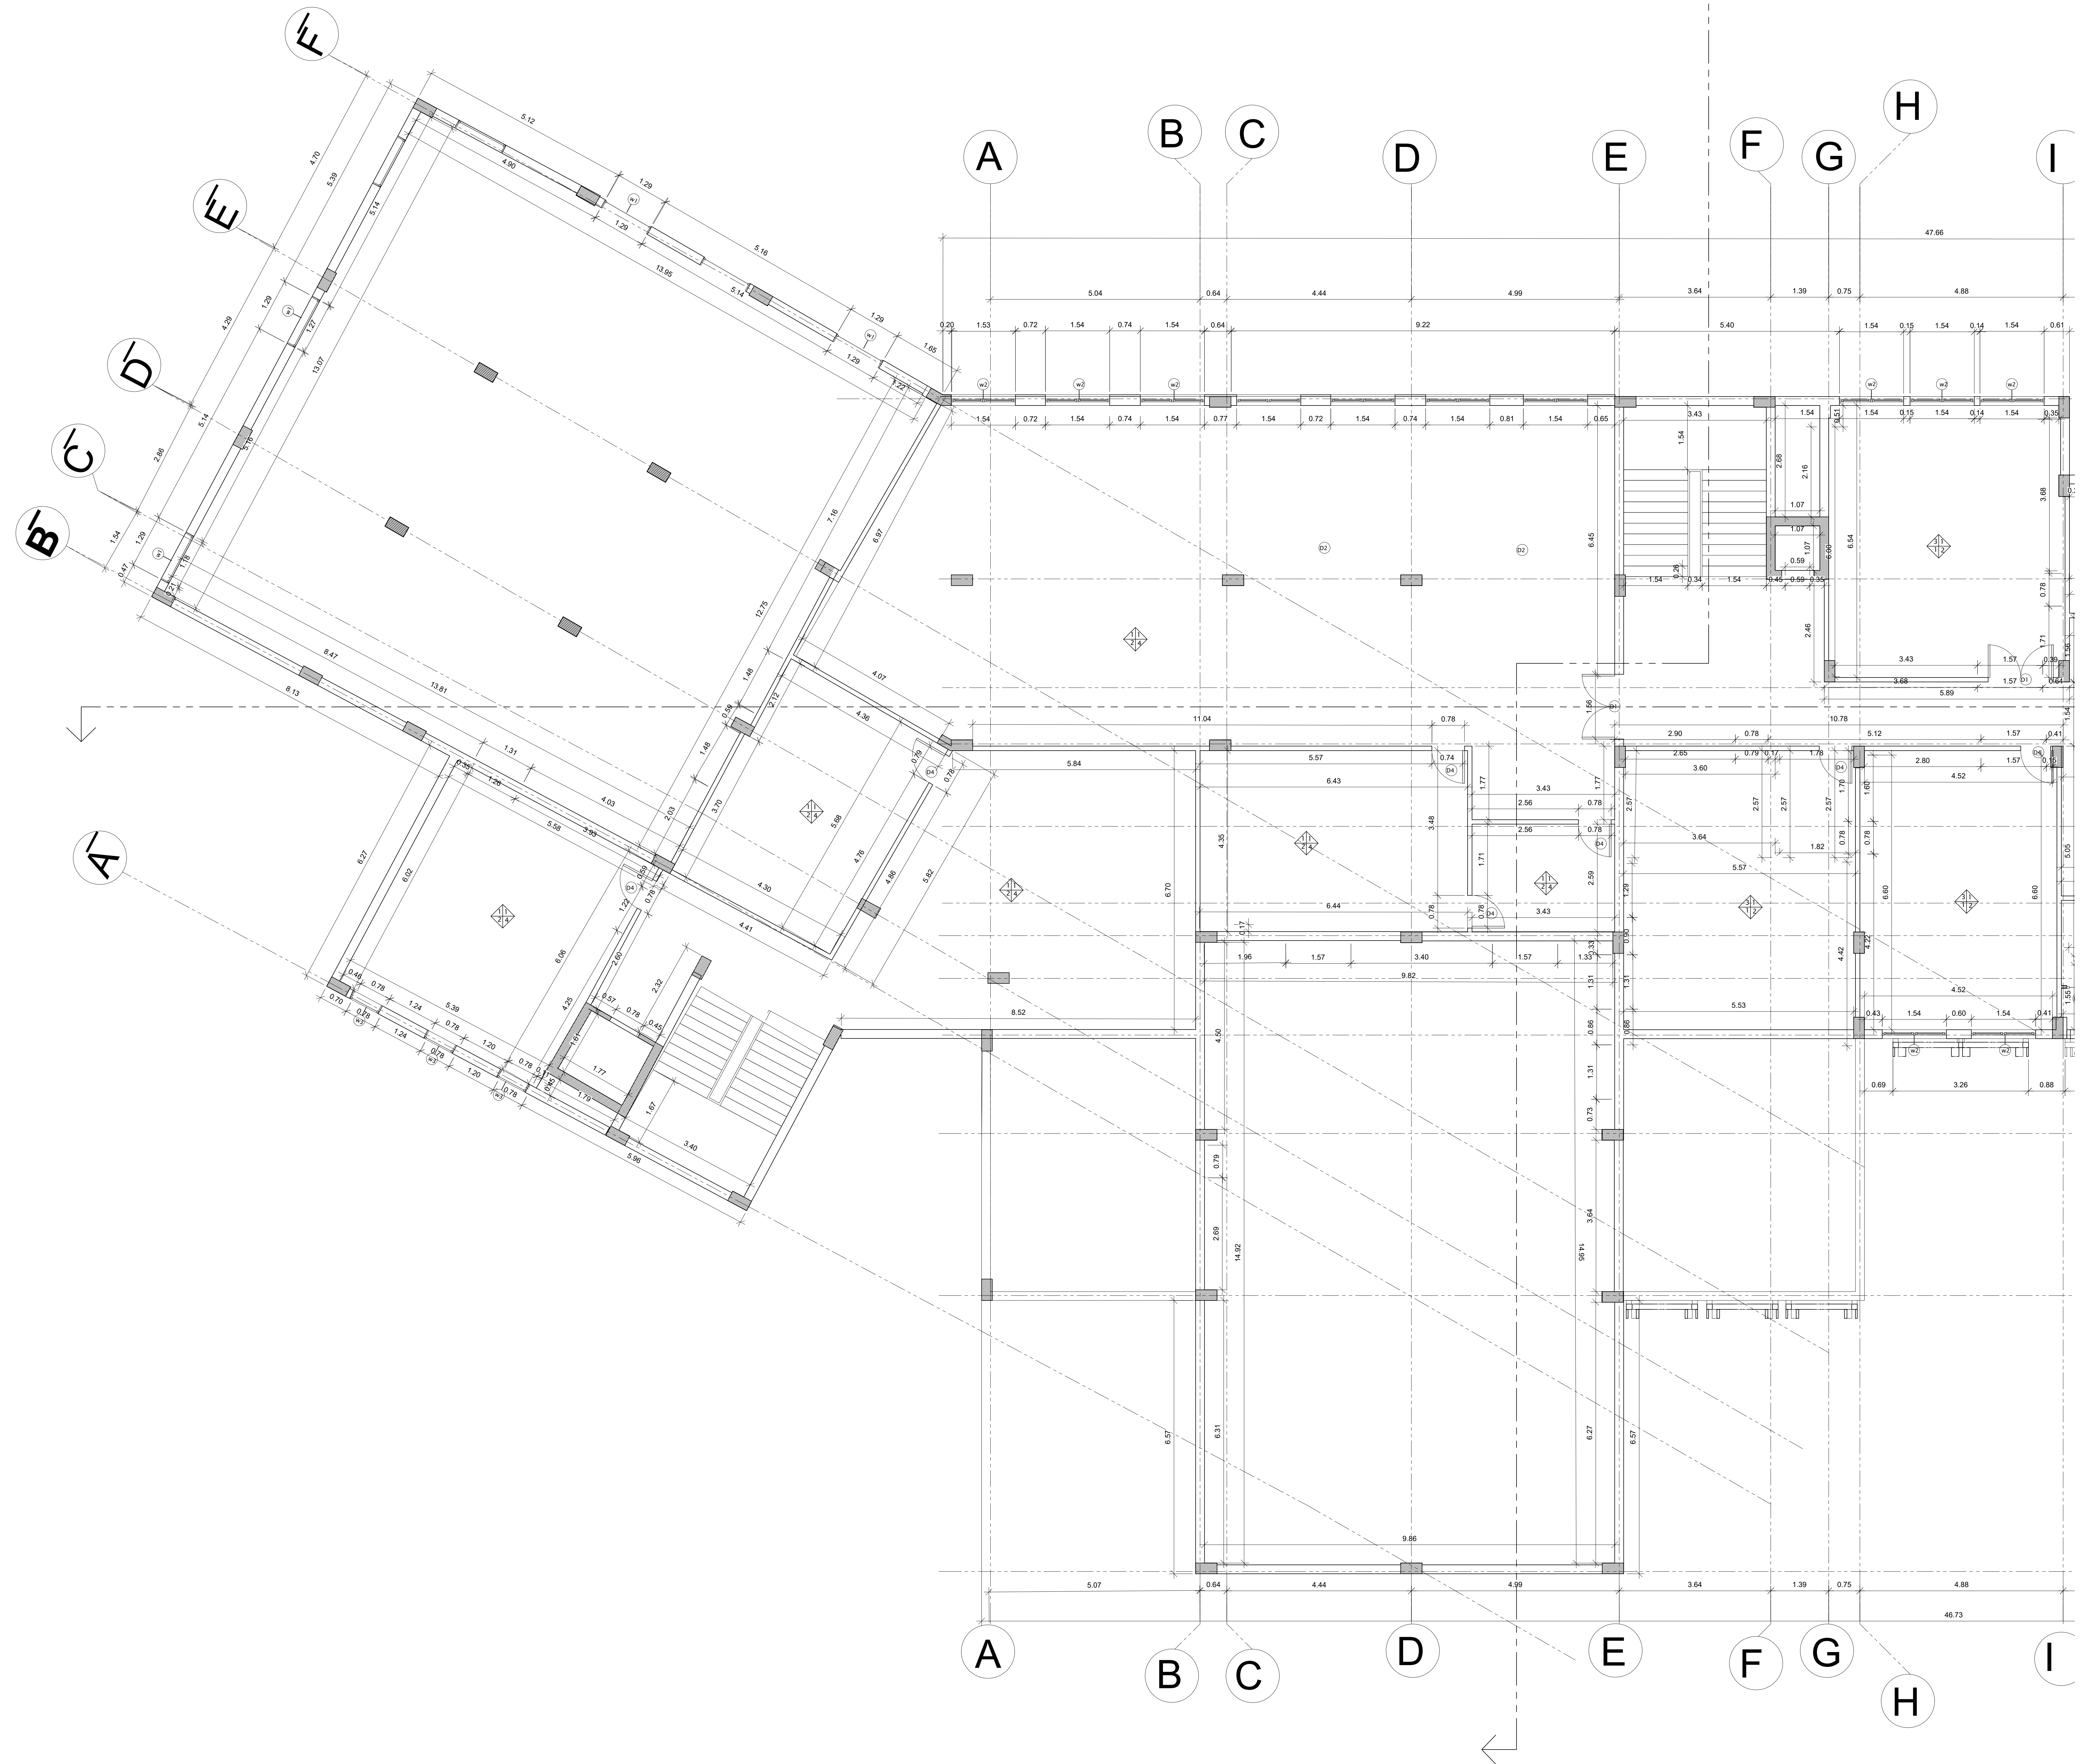





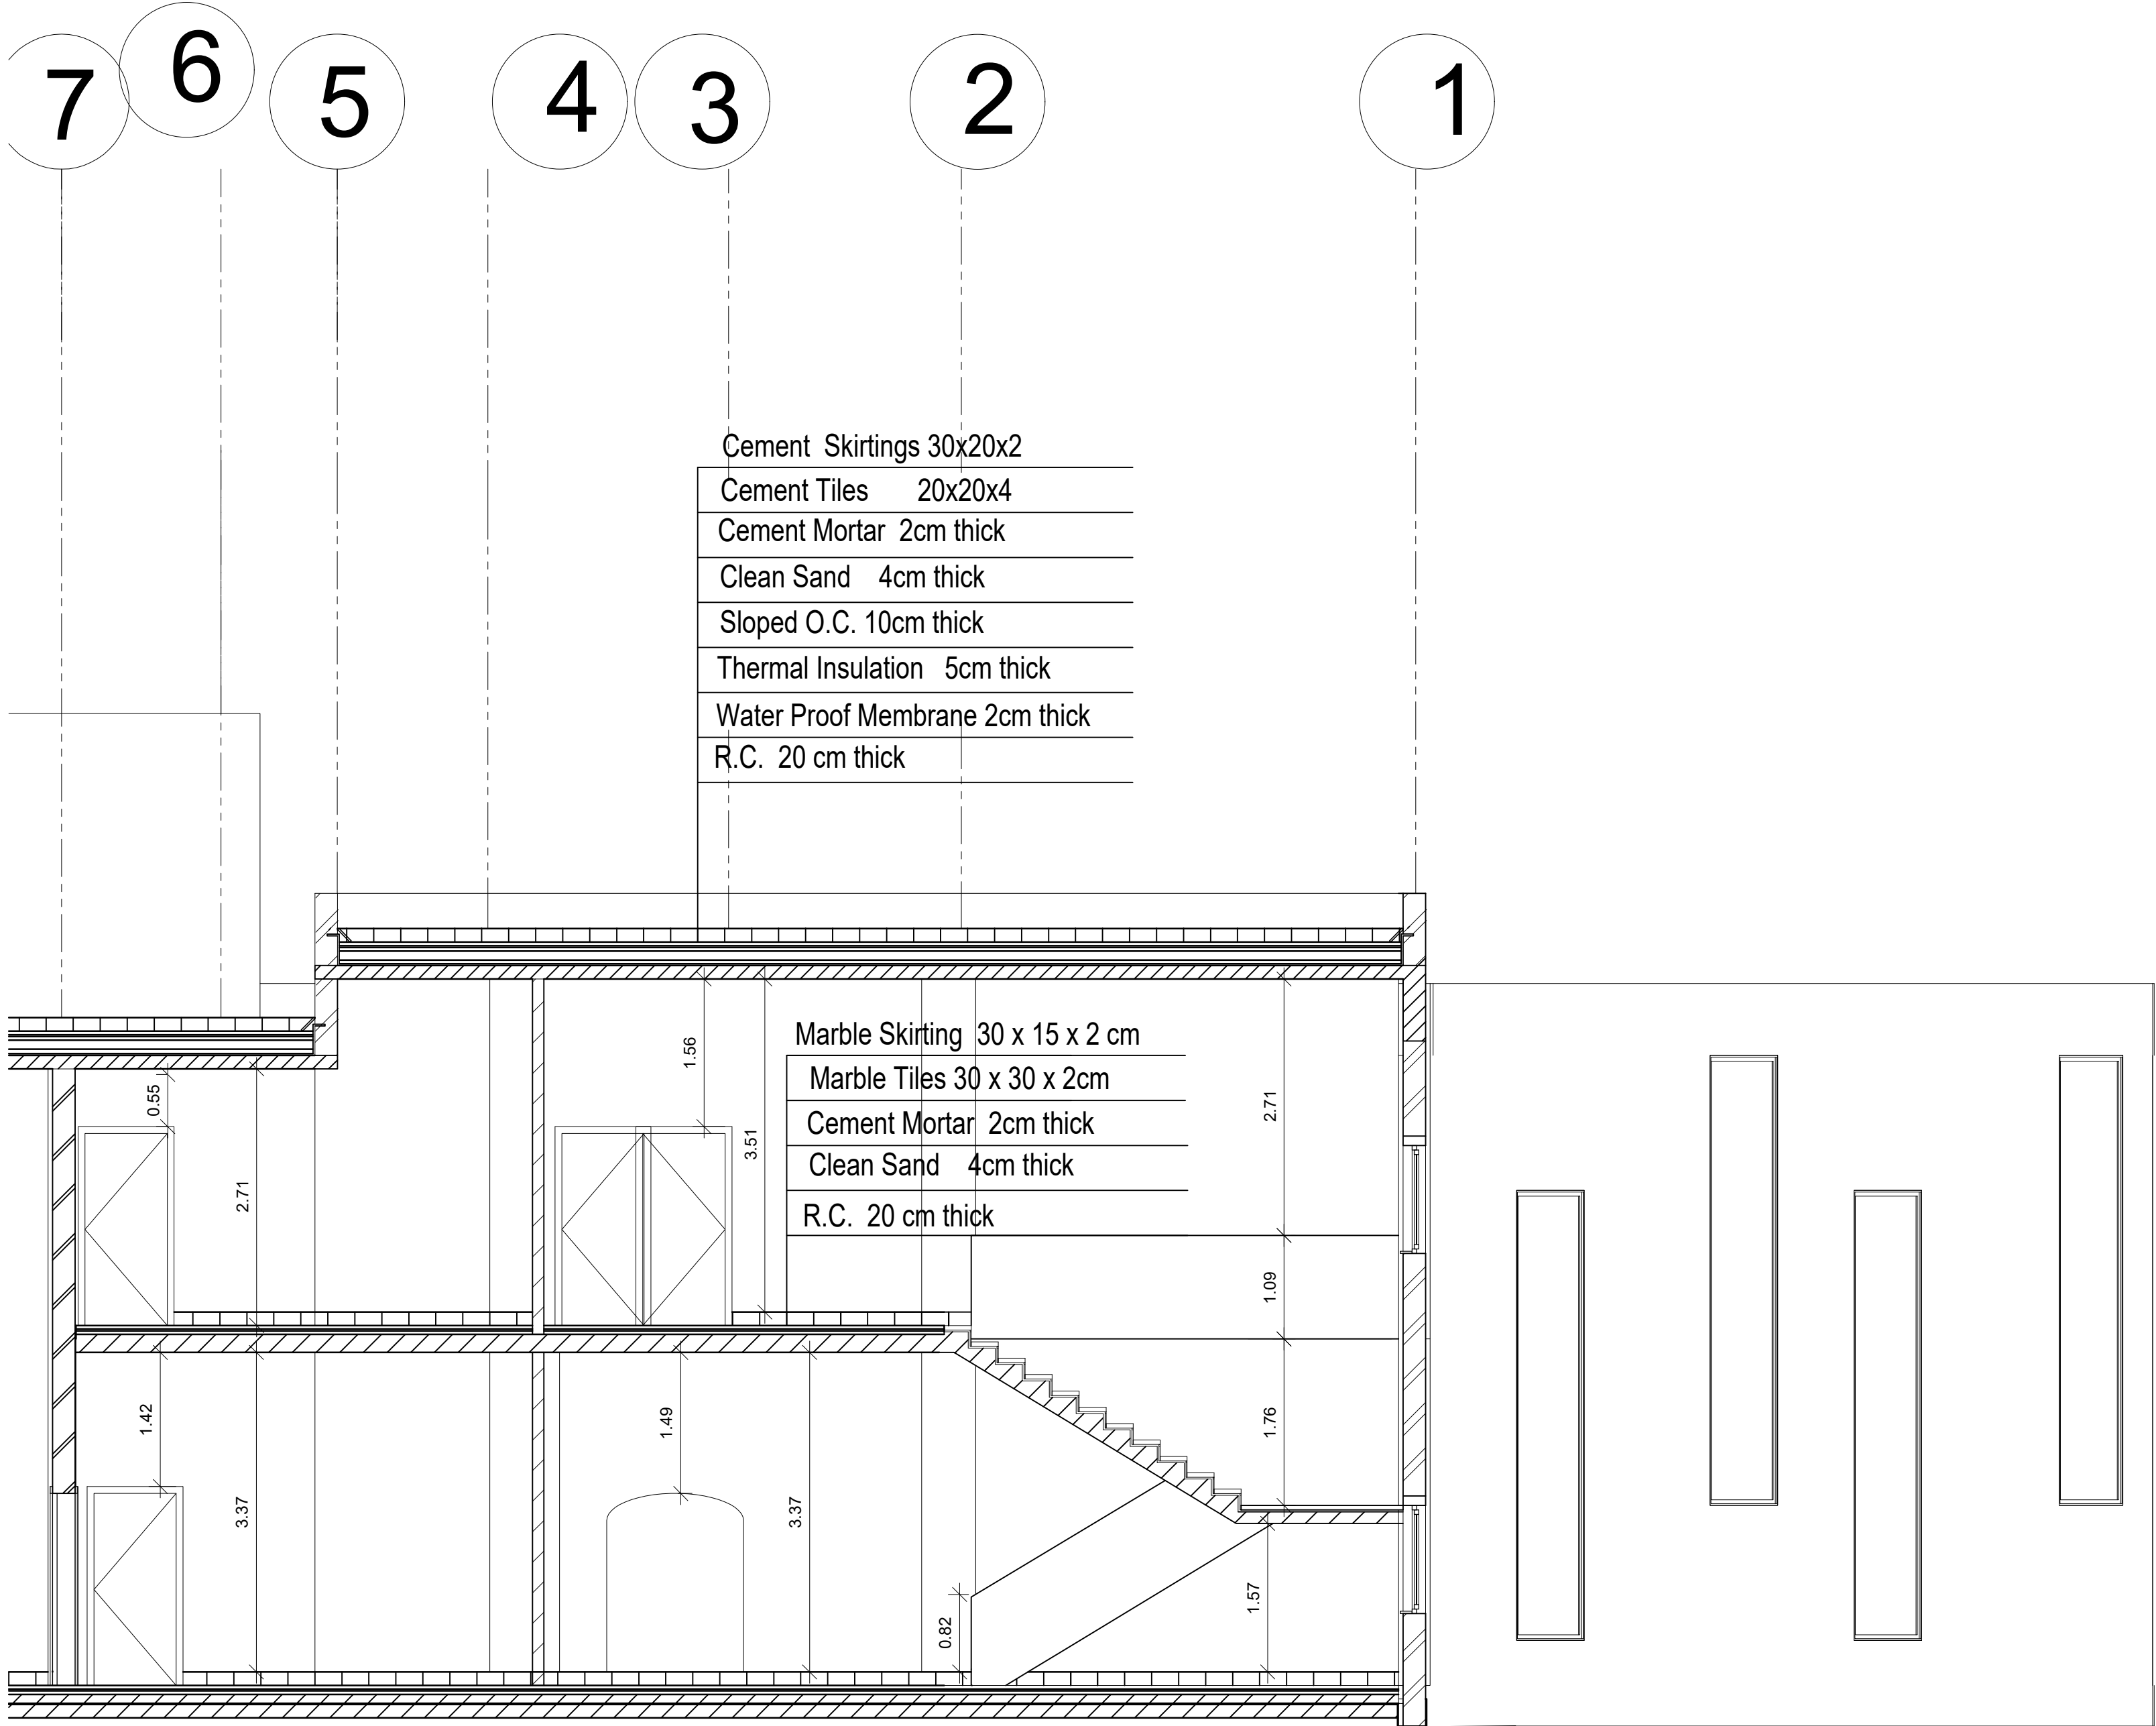


Cement Skirtings 30x20x2
Cement Tiles 20x20x4
Cement Mortar 2cm thick
Clean Sand 4cm thick
Sloped O.C. 10cm thick
Thermal Insulation 5cm thick
Water Proof Membrane 2cm thick
R.C. 20 cm thick

Cement Skirtings 30x20x2
Cement Tiles 20x20x4
Cement Mortar 2cm thick
Clean Sand 4cm thick
Sloped O.C. 10cm thick
Thermal Insulation 5cm thick
Water Proof Membrane 2cm thick
R.C. 20 cm thick

Marble Skirting 30 x 15 x 2 cm
Marble Tiles 30 x 30 x 2cm
Cement Mortar 2cm thick
Clean Sand 4cm thick
R.C. 20 cm thick

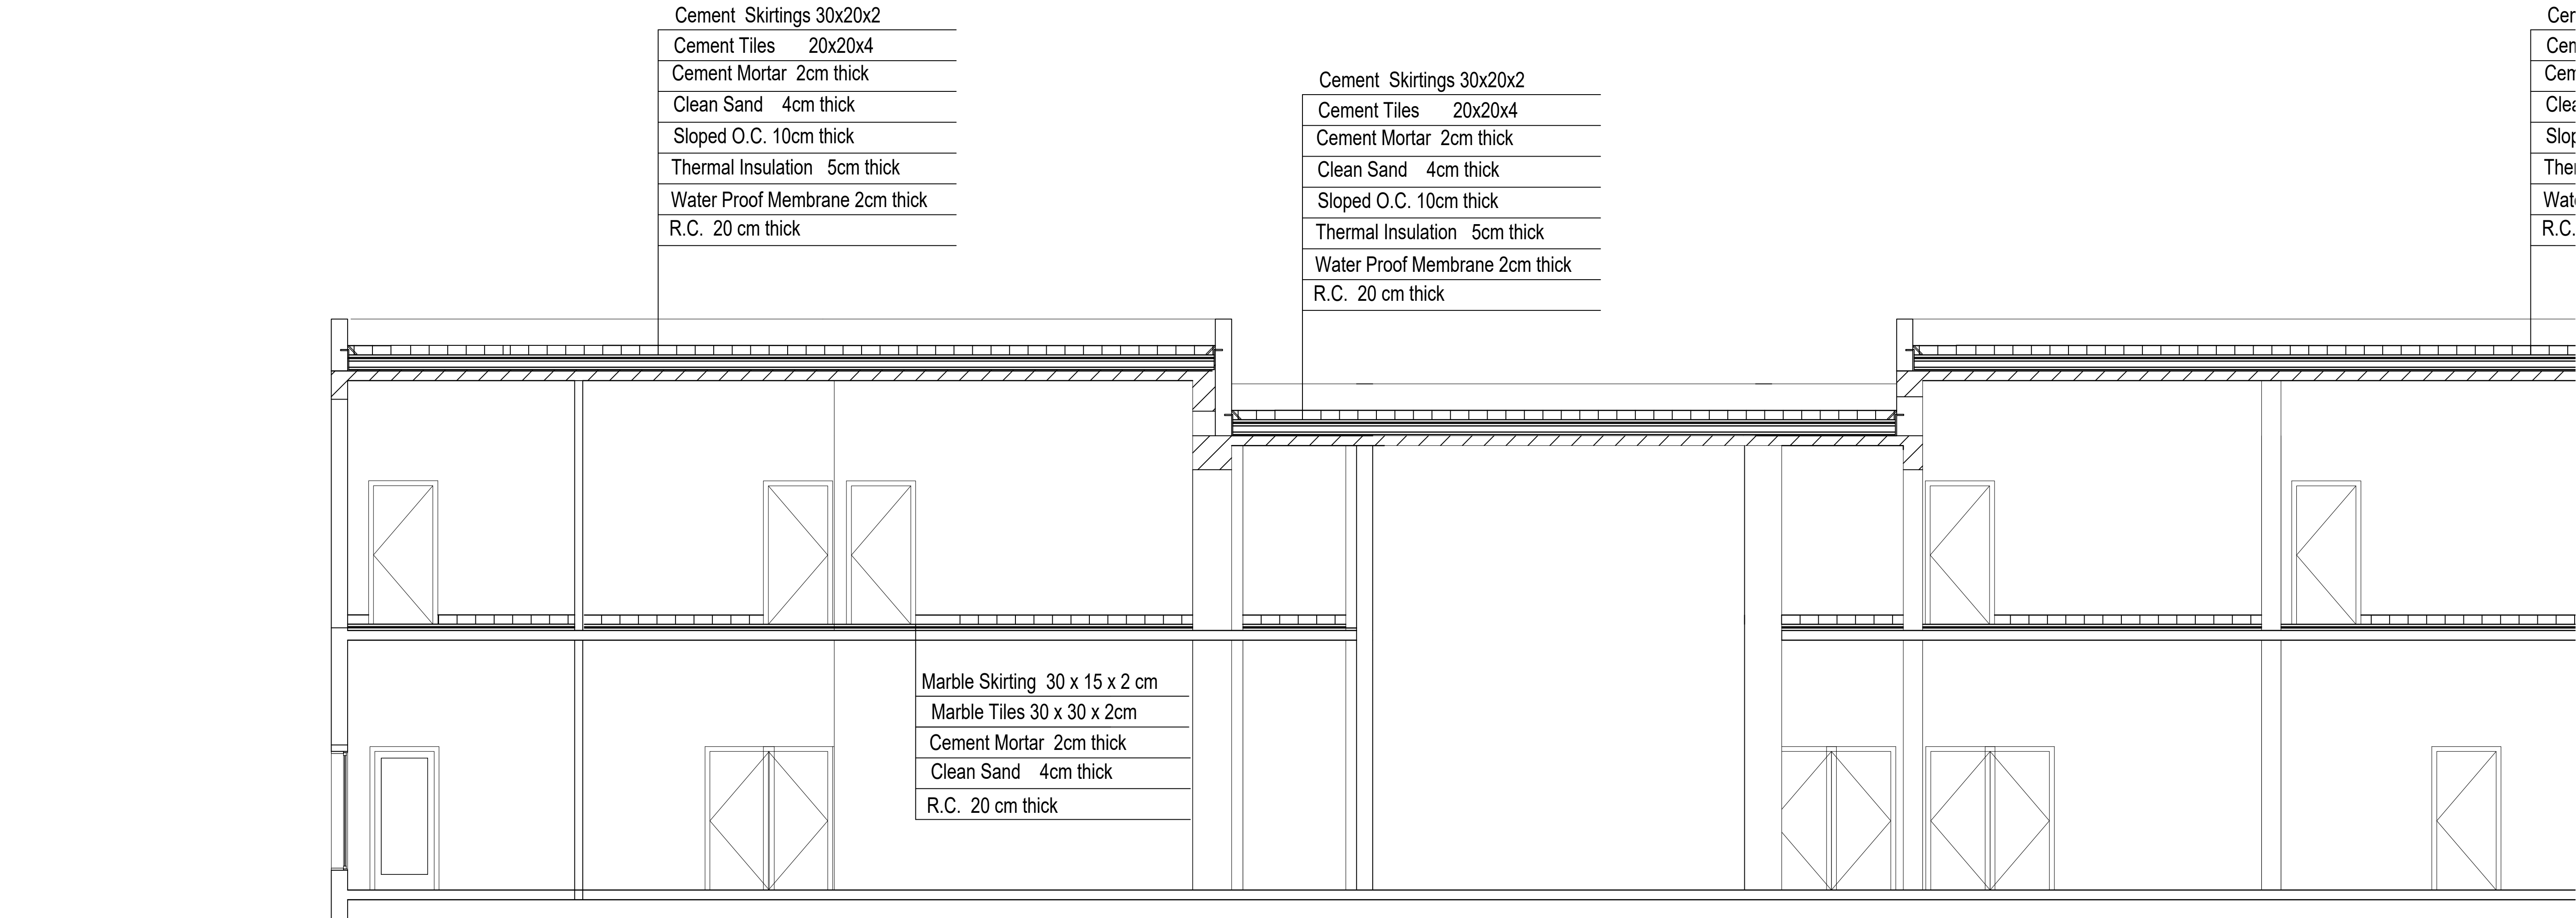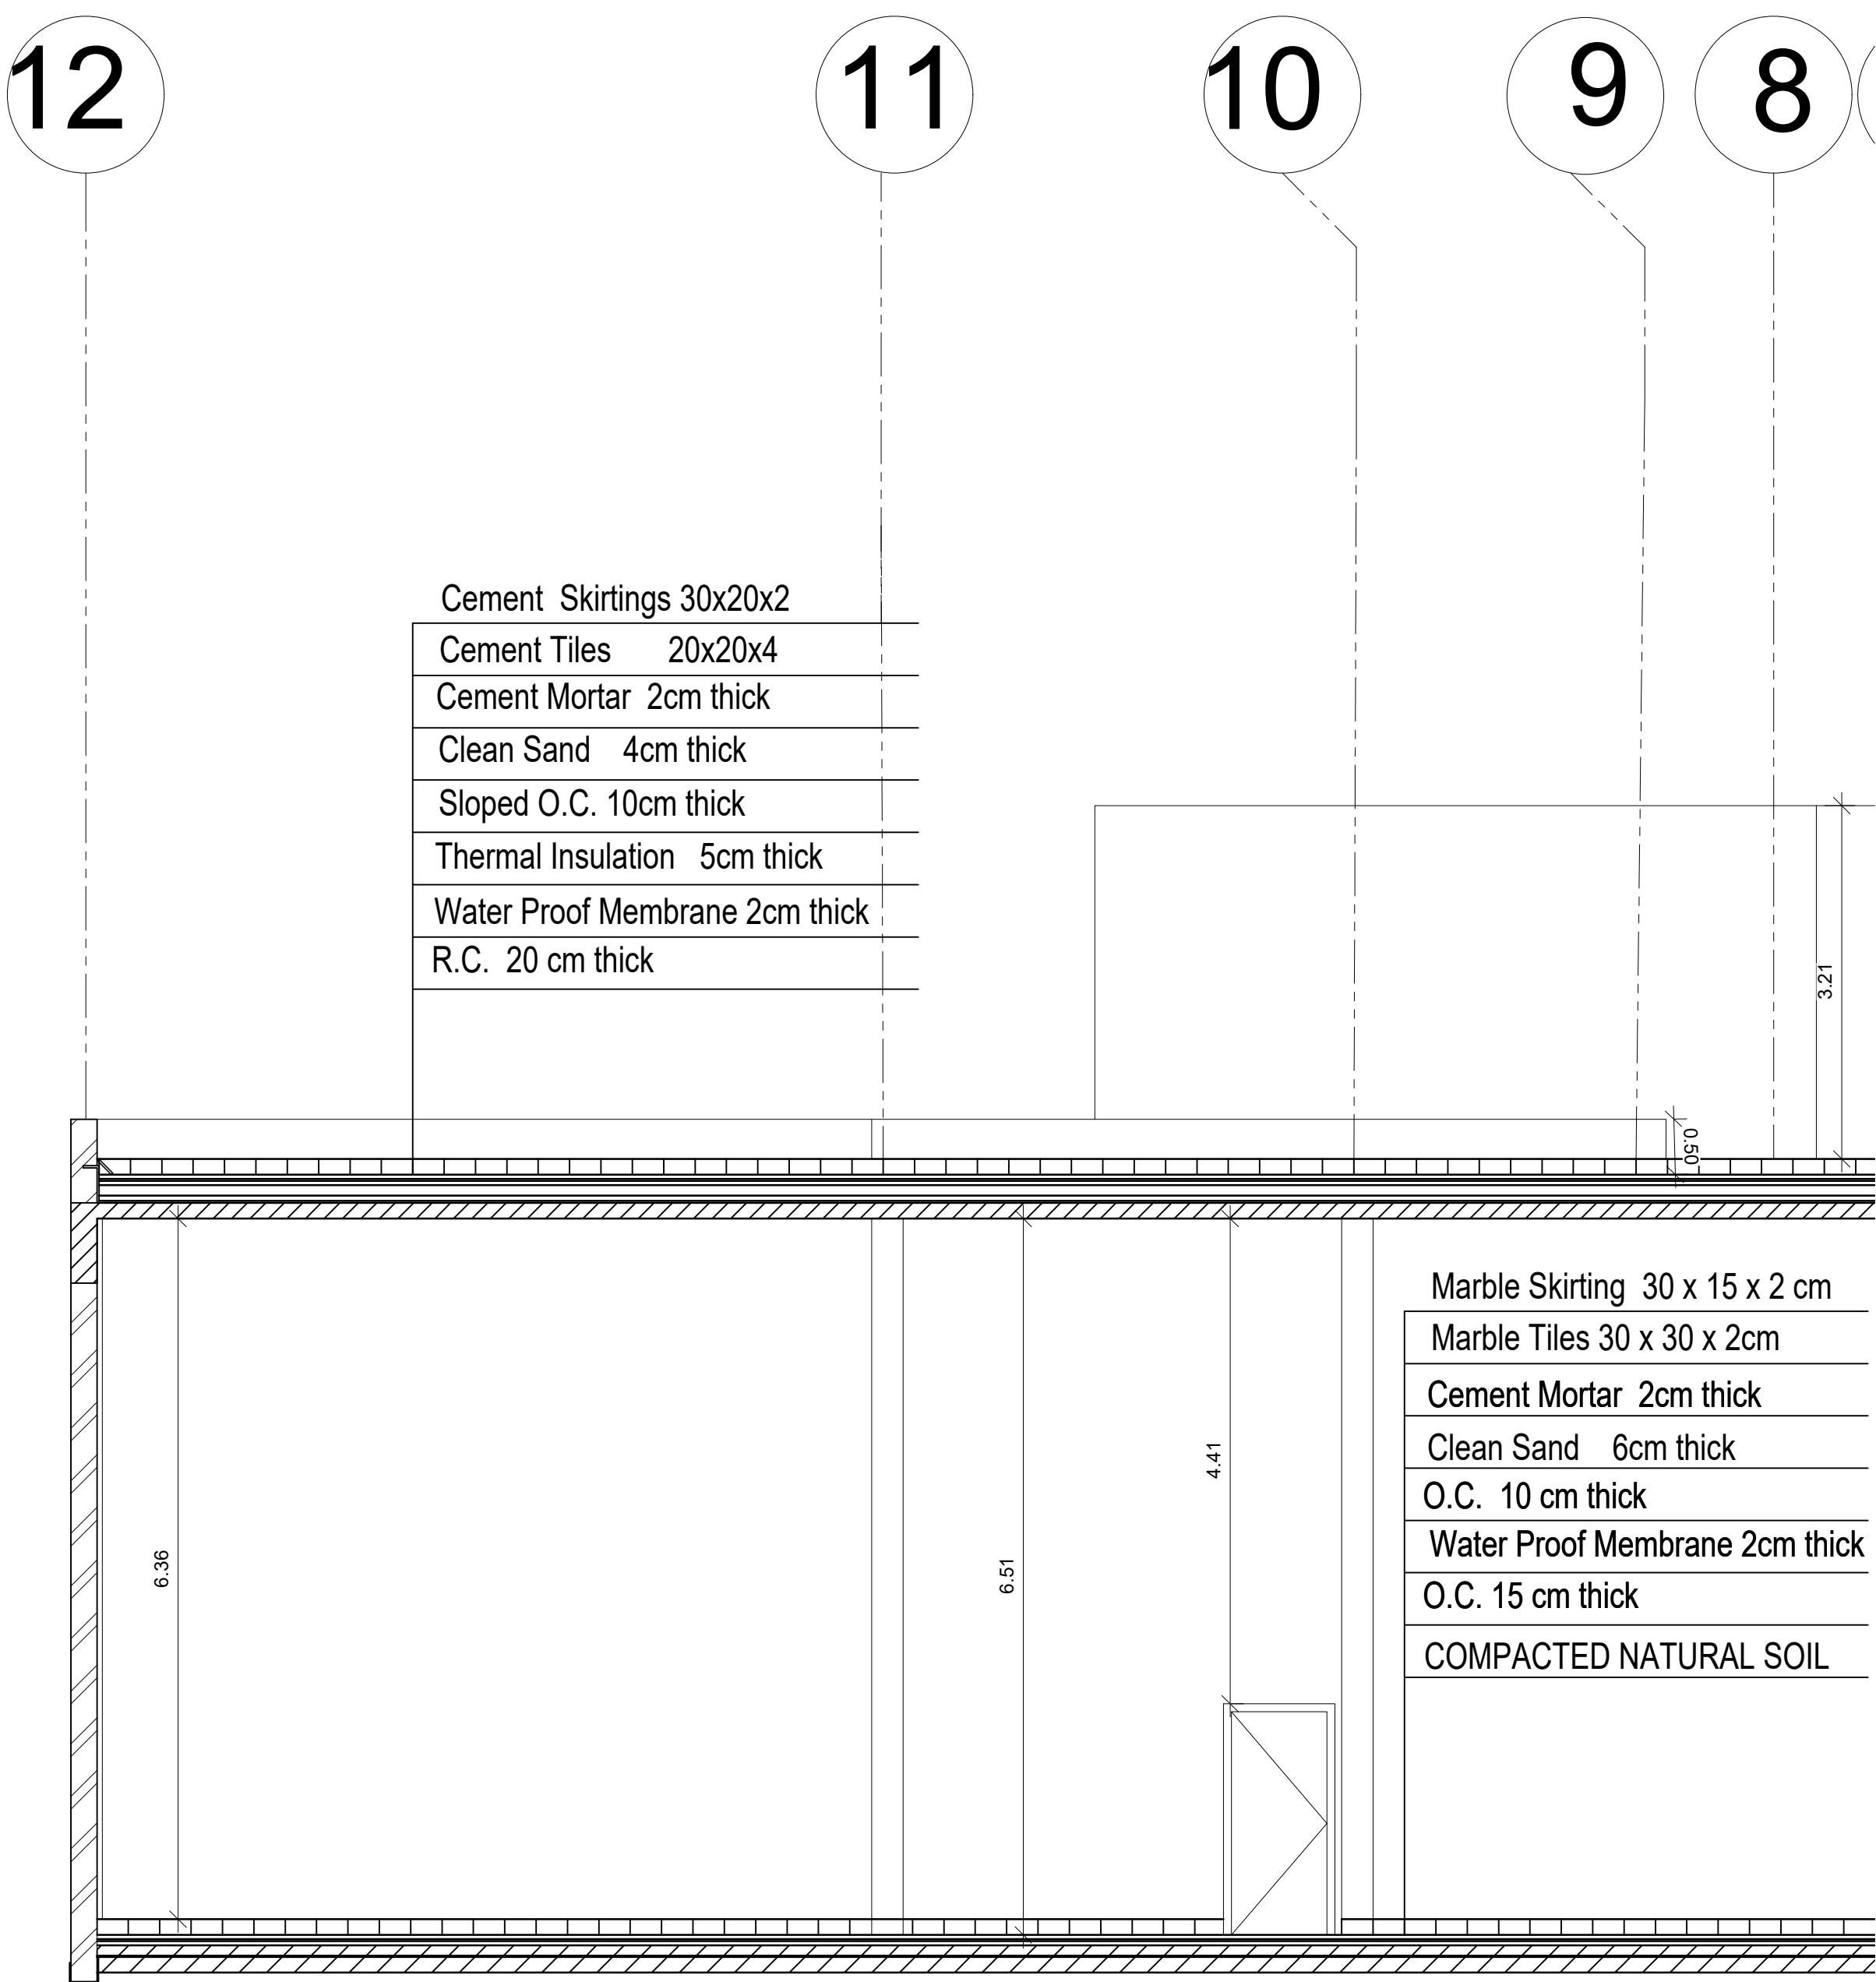

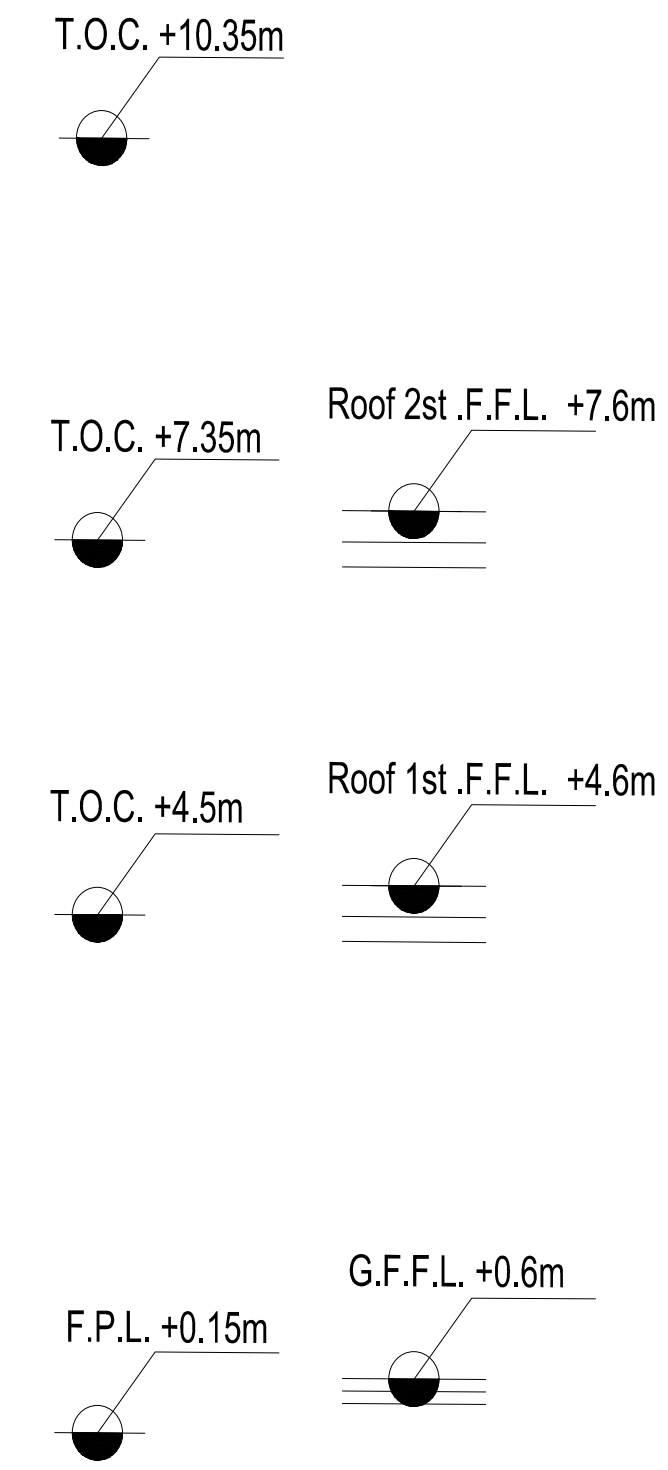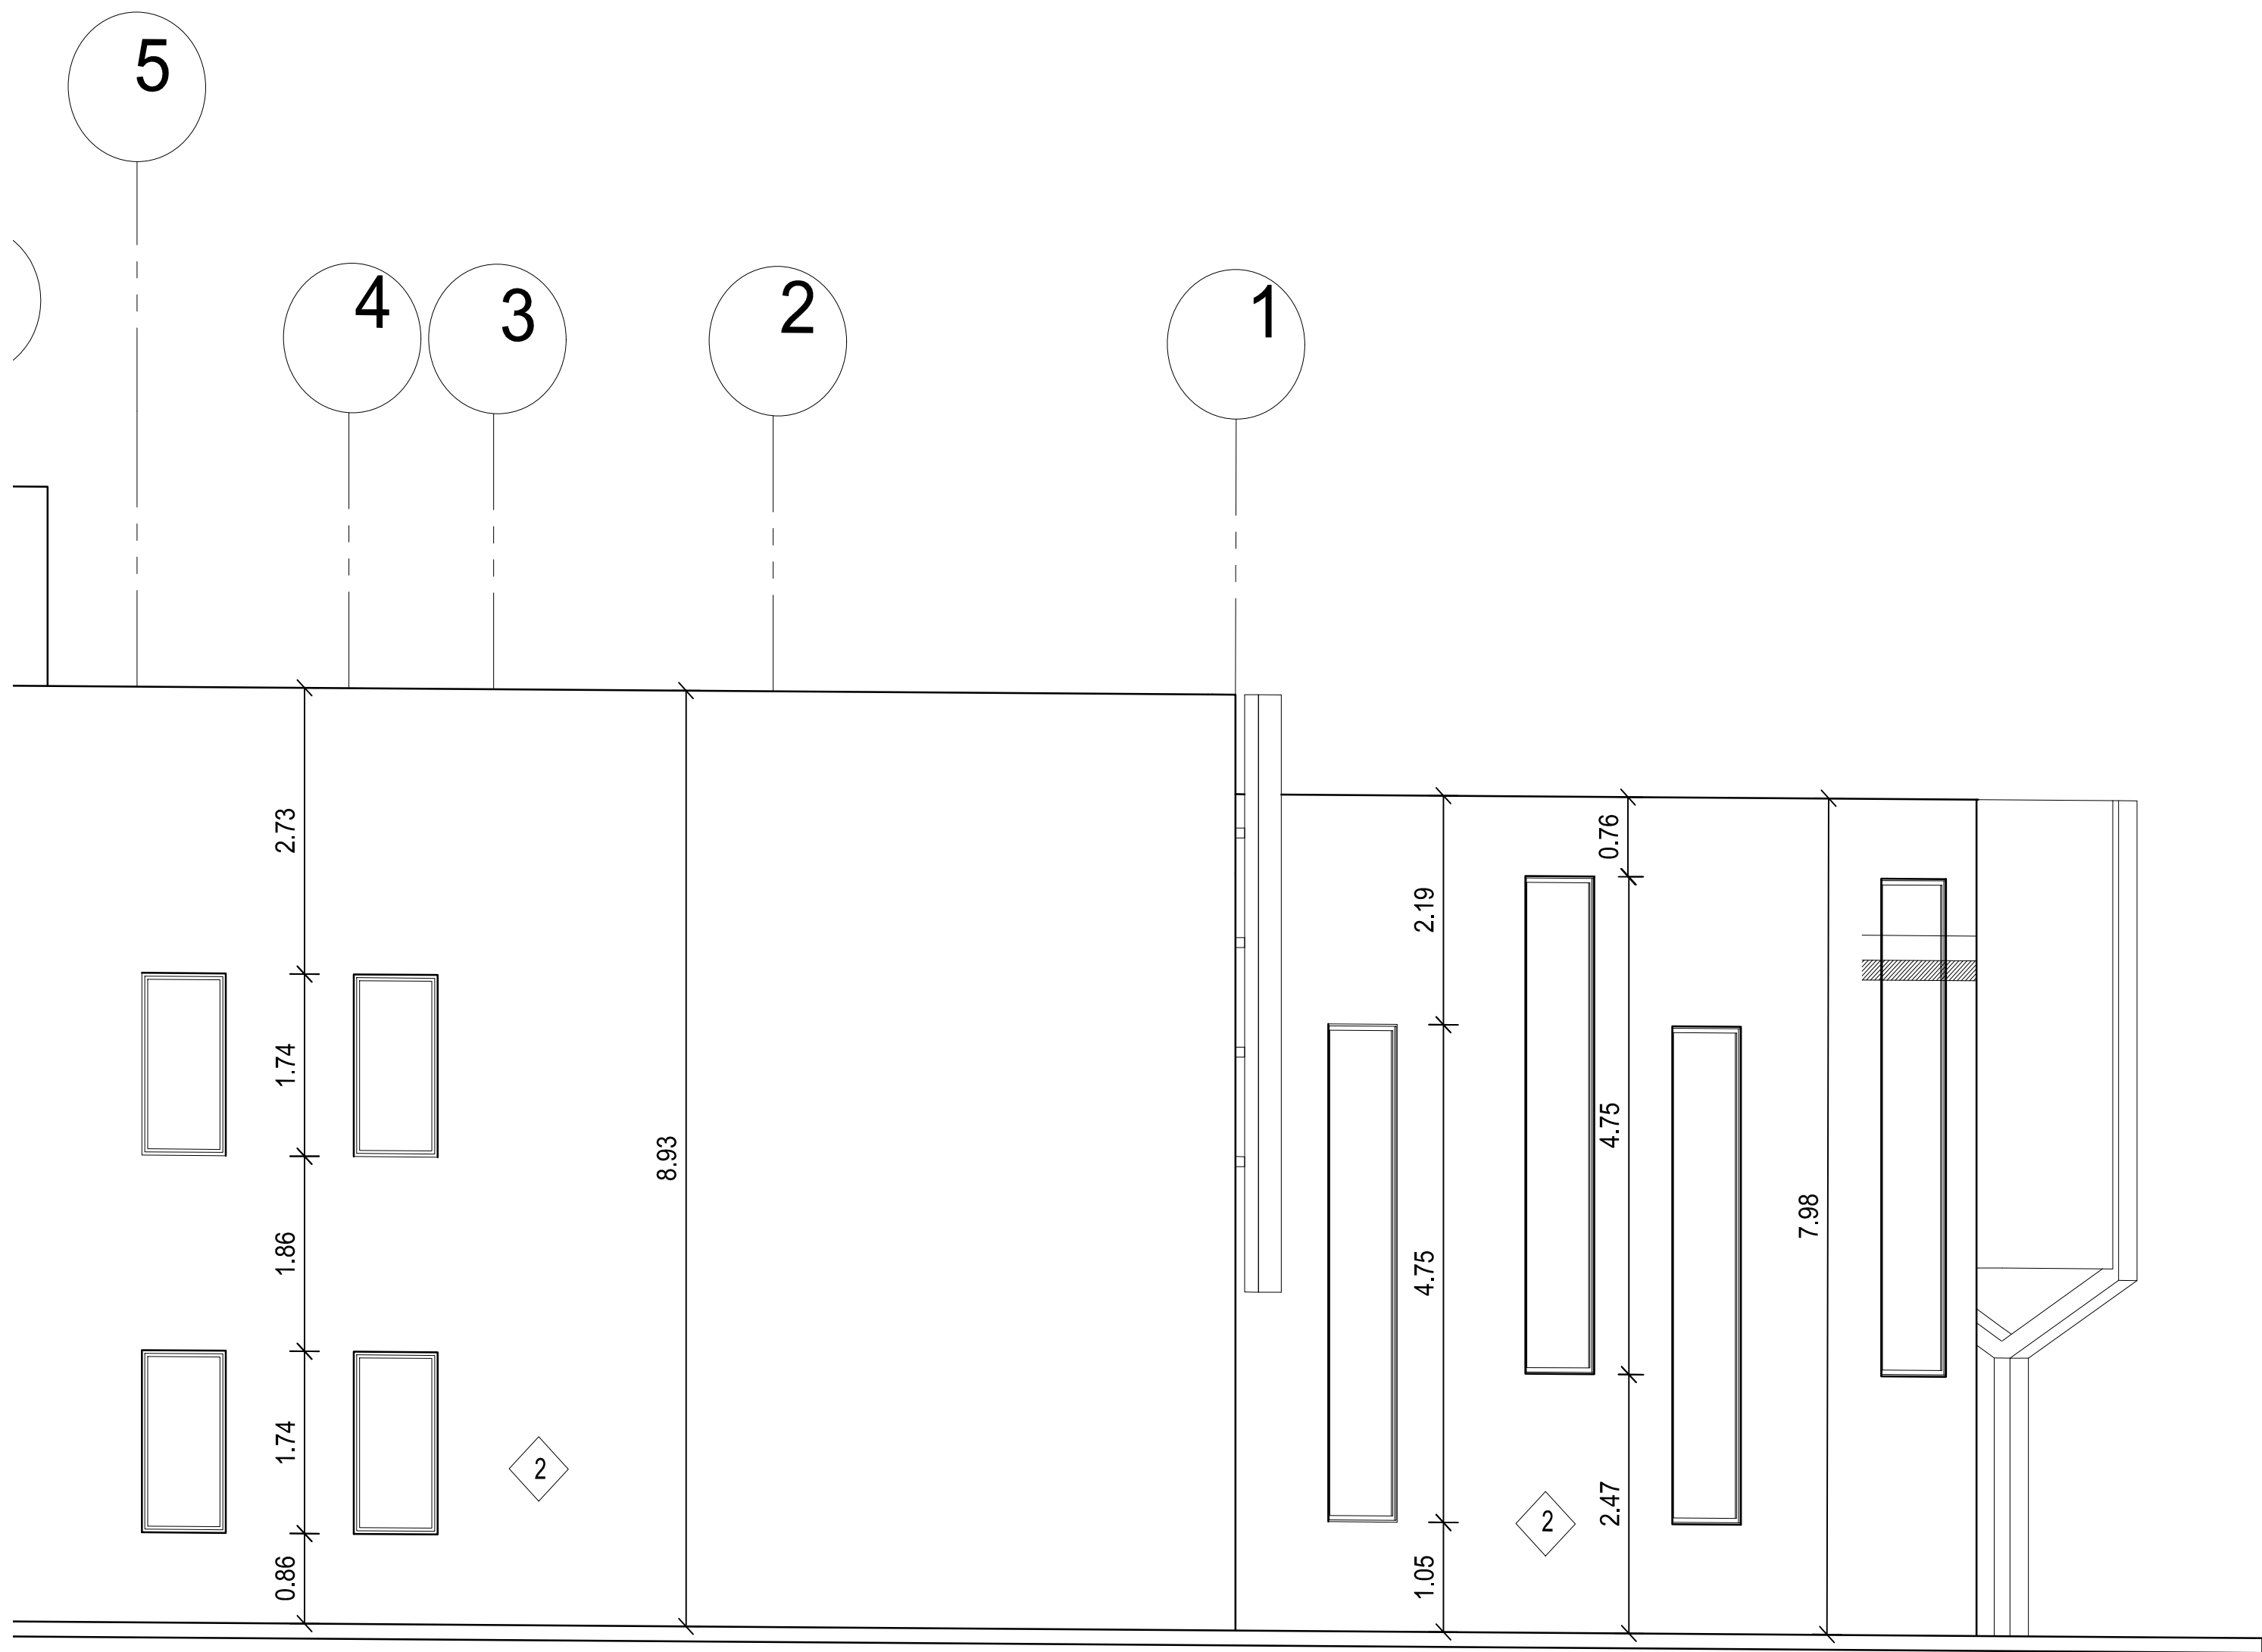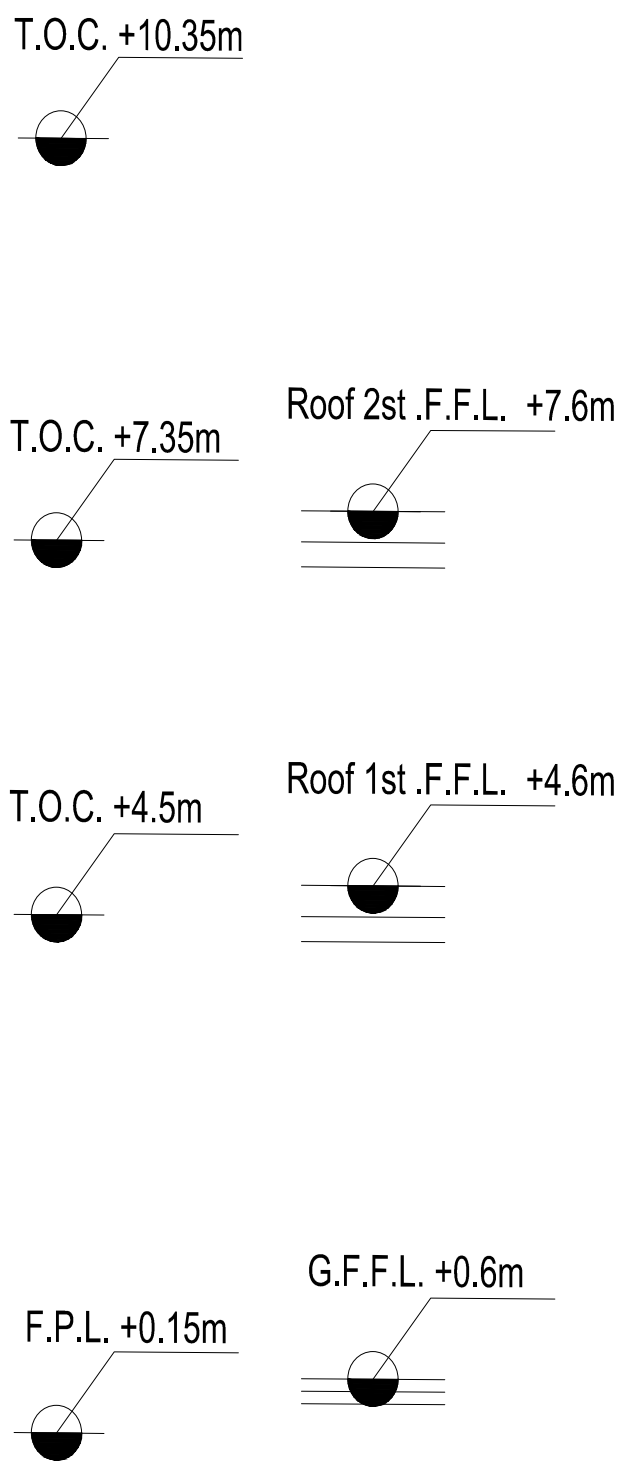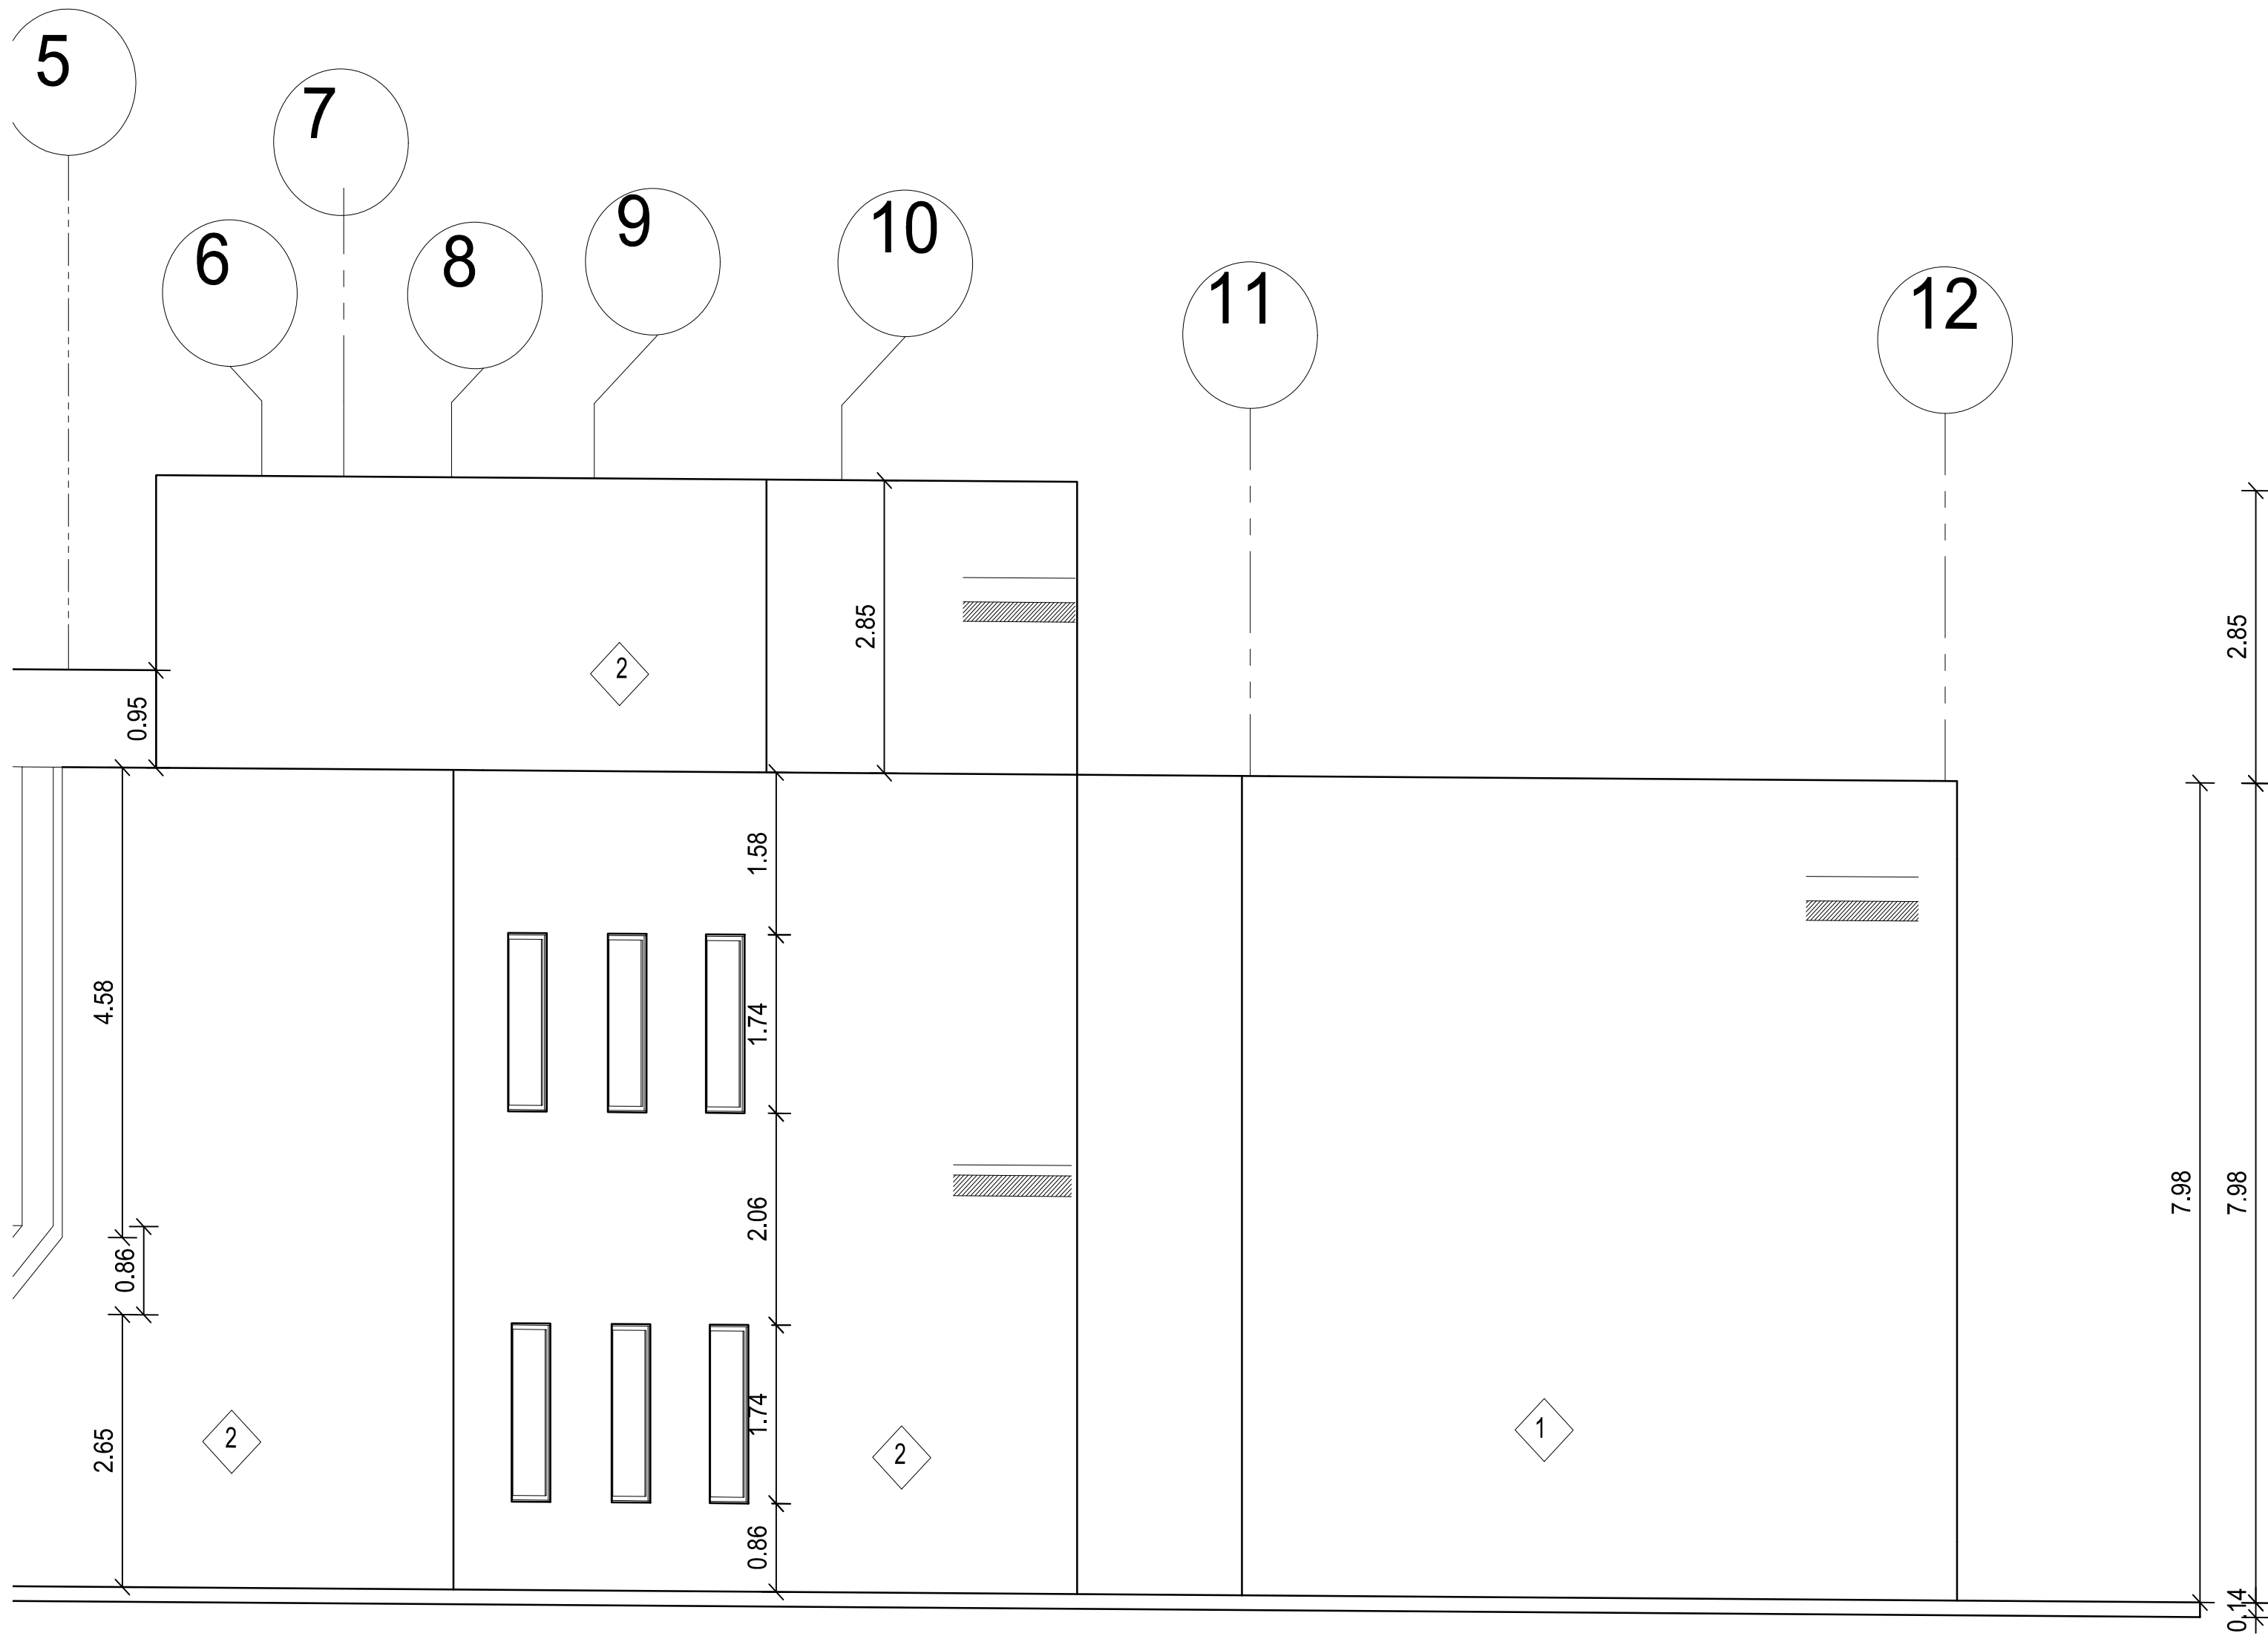

ABBREVIATIONS :

ABV.	DISCRIPTION
F.F.L.	FINISH FLOOR LEVEL
F.P.L.	FINISH PAVEMENT LEVEL
F.R.L.	FINISH ROAD LEVEL
T.O.C.	TOP OF CONCRETE
B.F.F.L.	BASEMENT FINISH FLOOR LEVEL
G.F.F.L.	GROUND FINISH FLOOR LEVEL
O.C.	ORDINARY CONCRETE
R.C.	REINFORCED CONCRETE
Thick.	THICKNESS





EXTERIOR WALLS





SYMBOL	DESCRIPTION
1	Paint Finish (Matte Plastic Paint)
2	Cementitious Textured Plaster
3	Wood Cladding (WPC Panels)

Abdul rahman Ashraf

DR. MOHAMED AISAEED

GROUND FLOOR
SCALE 1:50

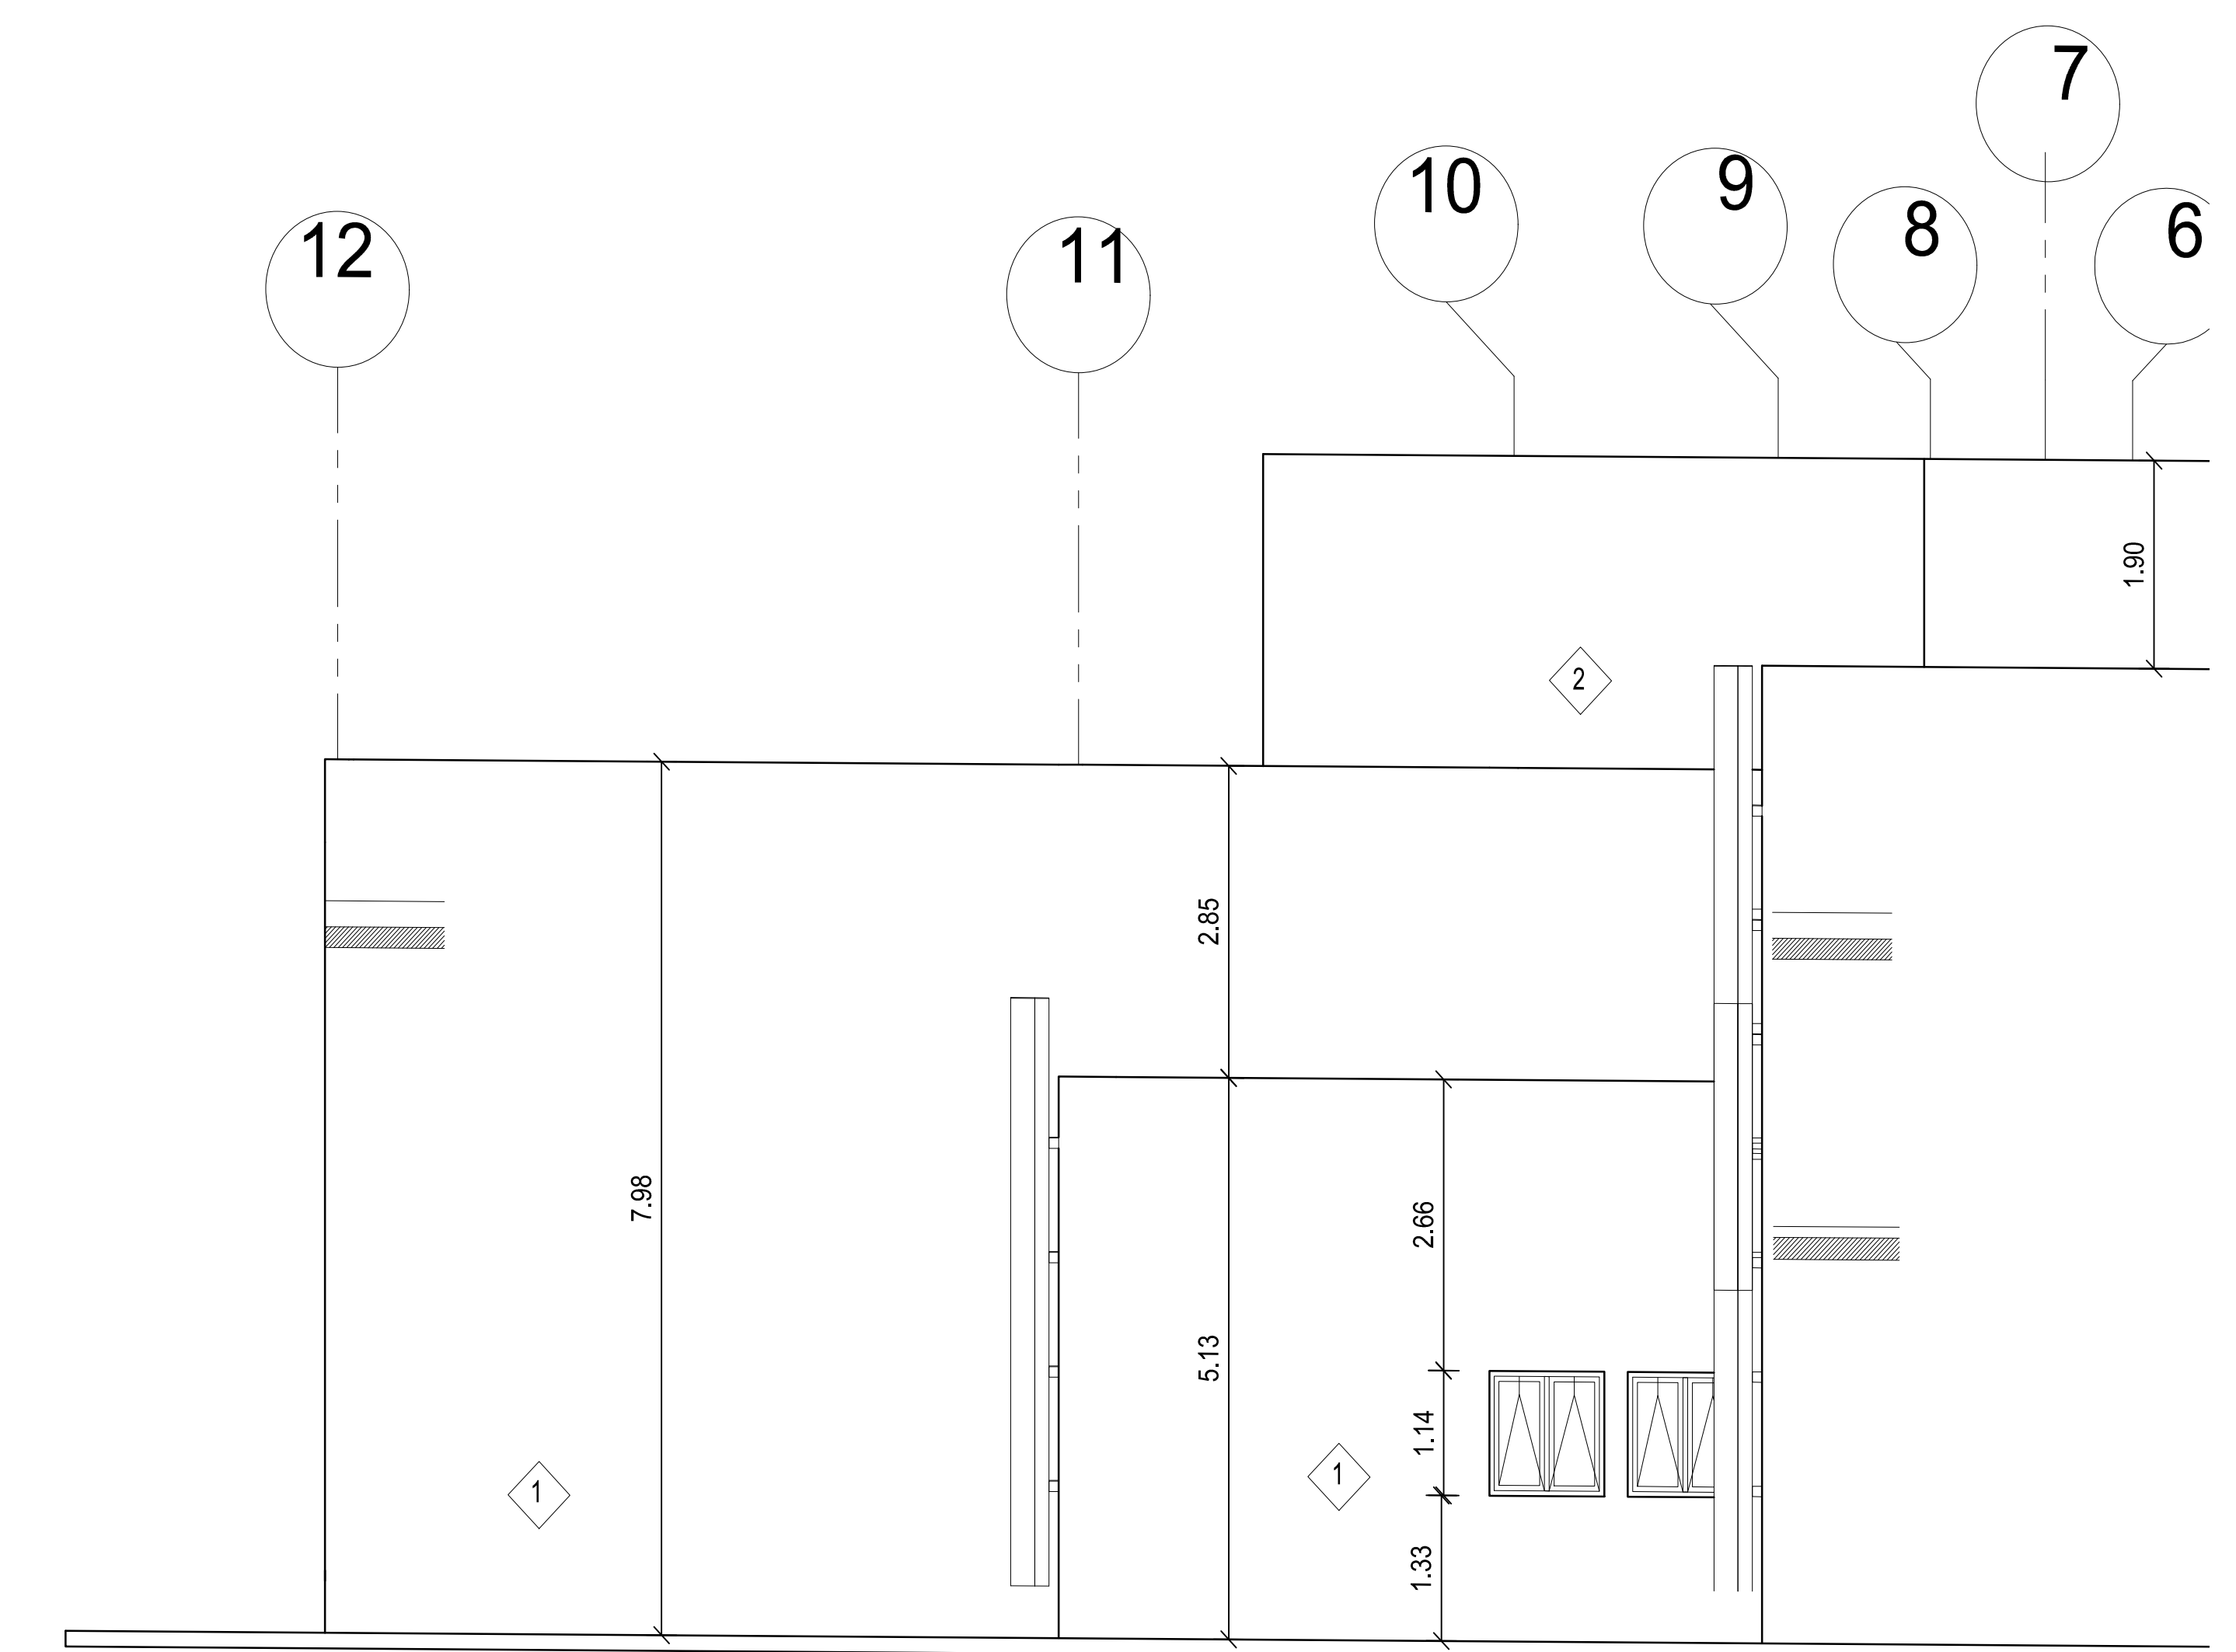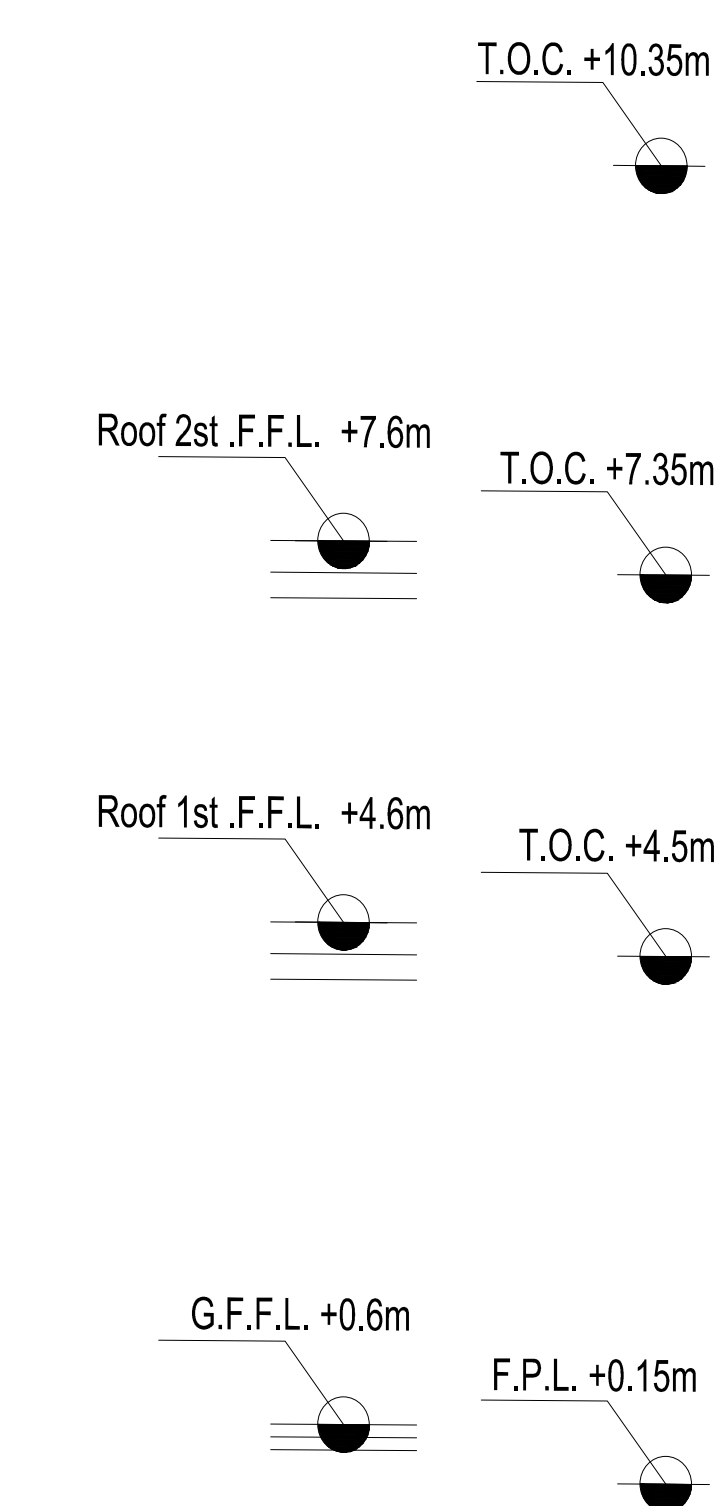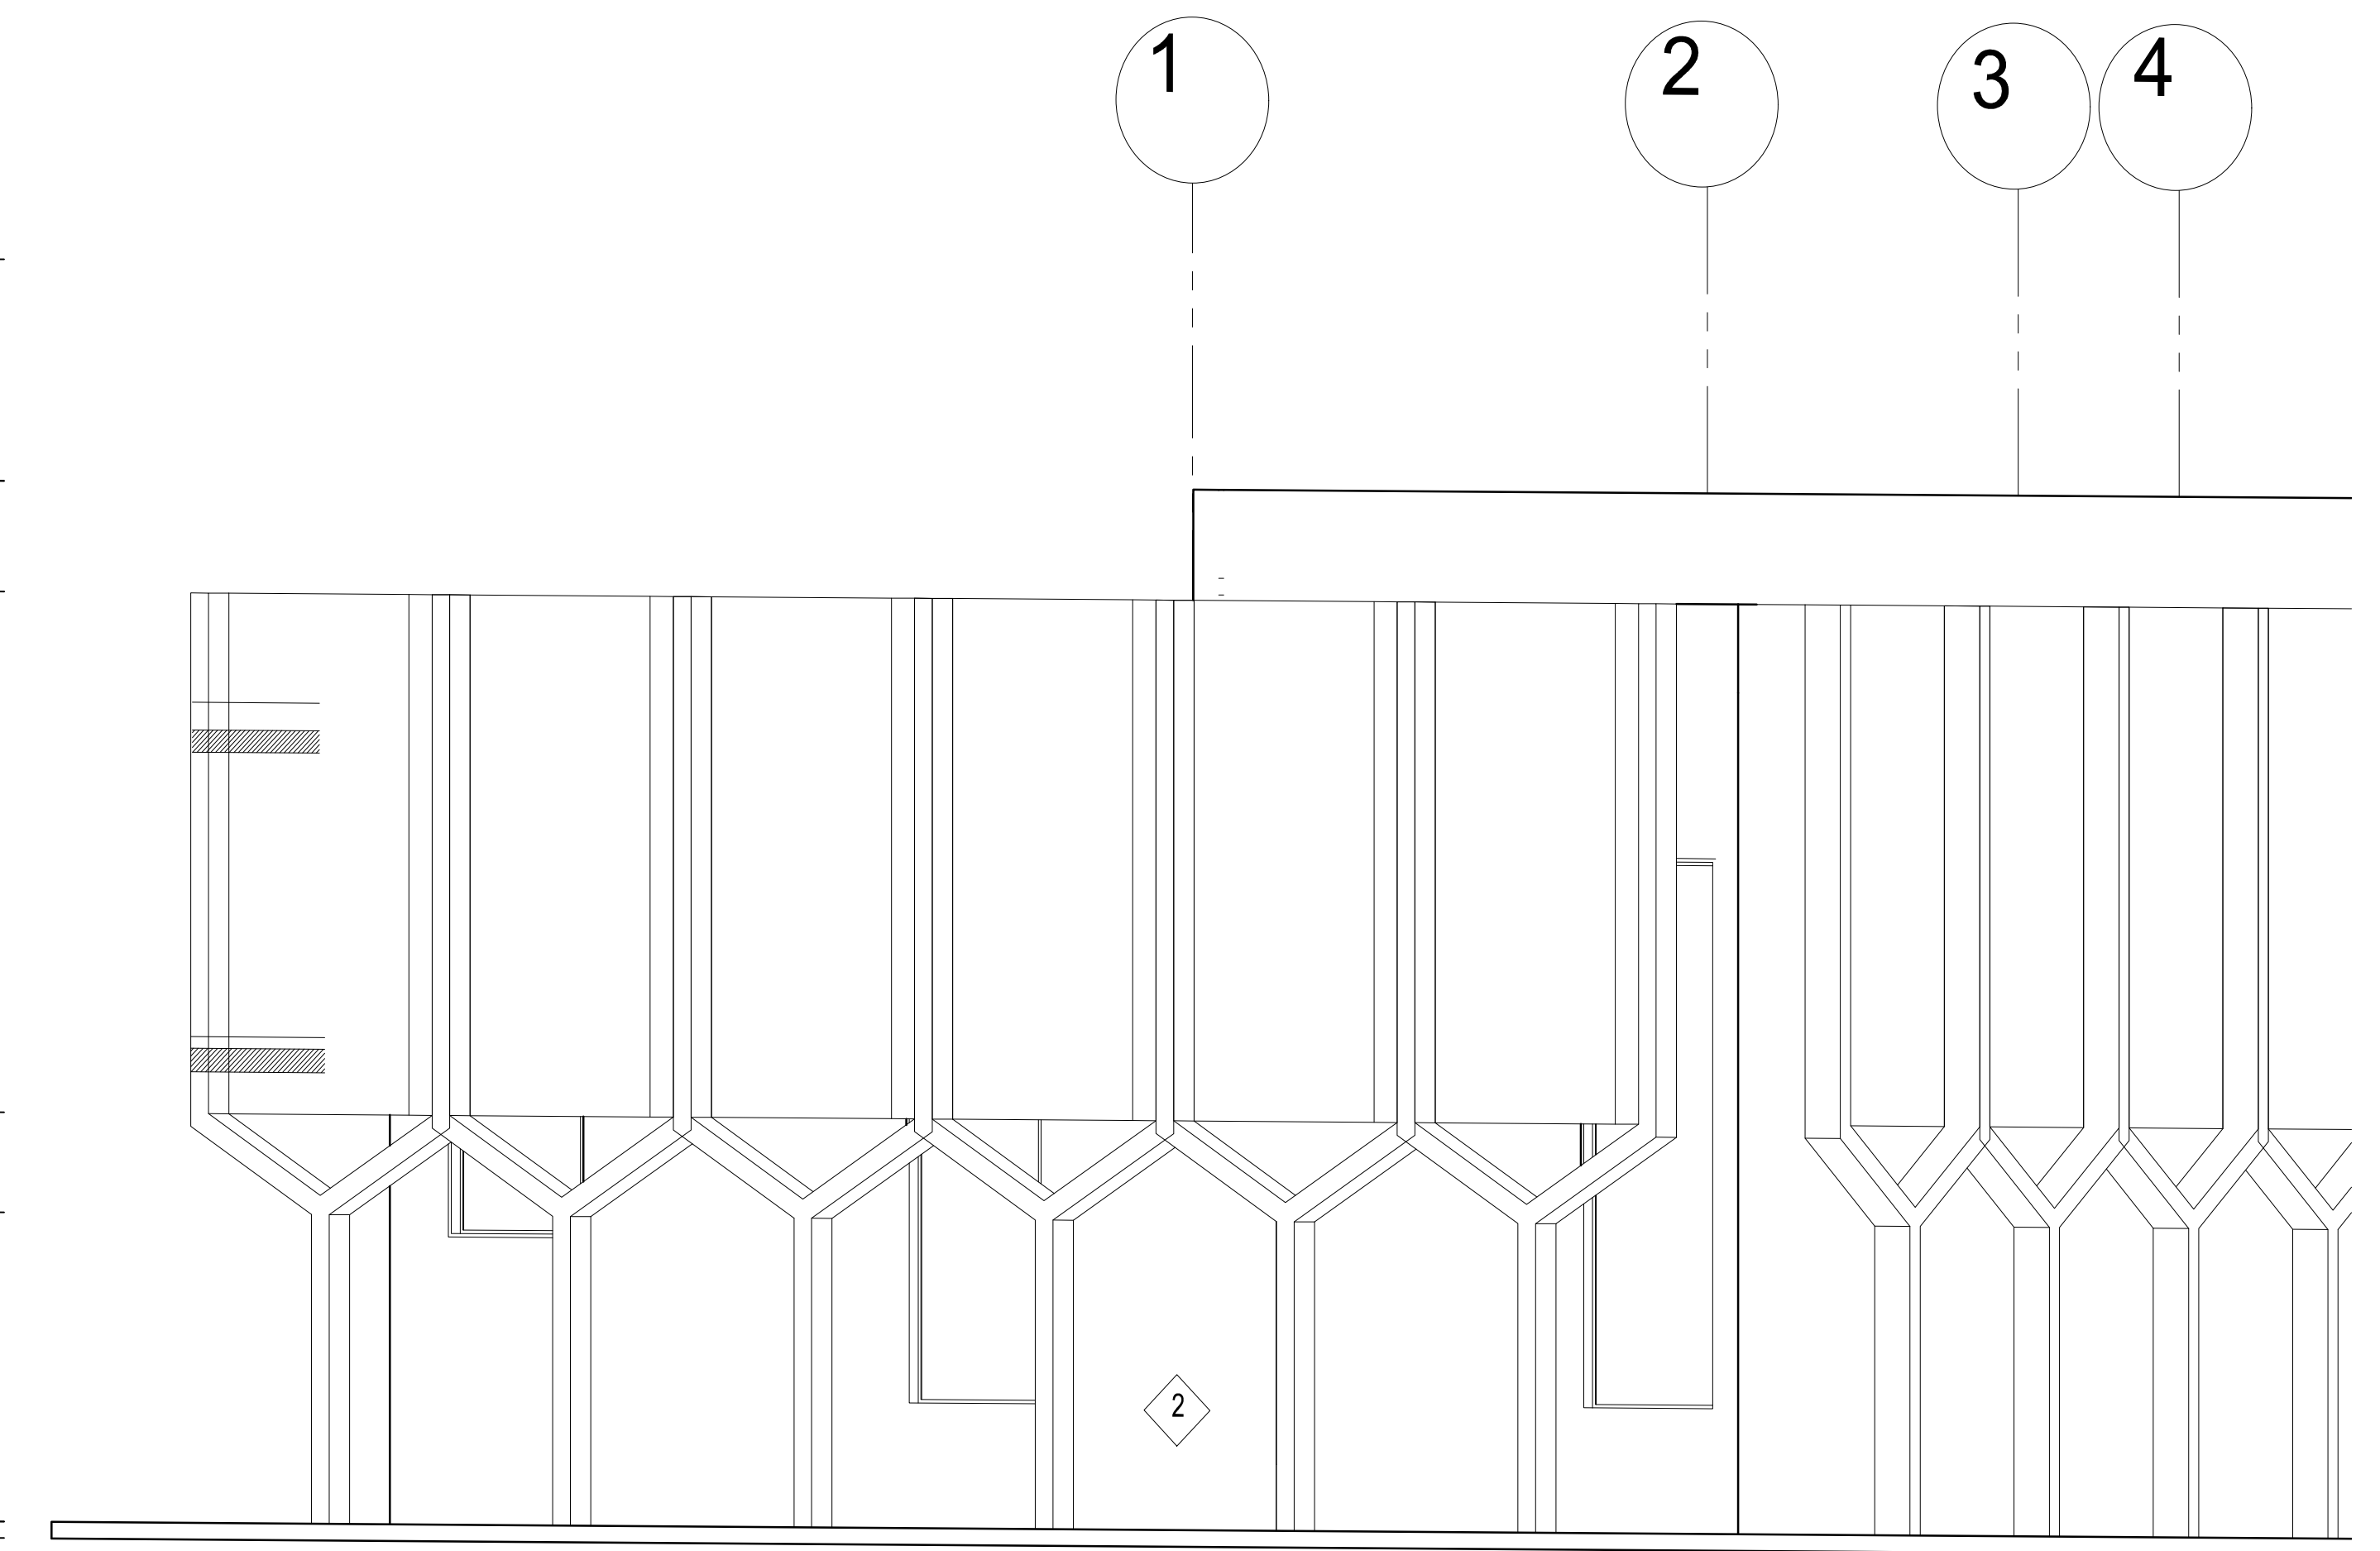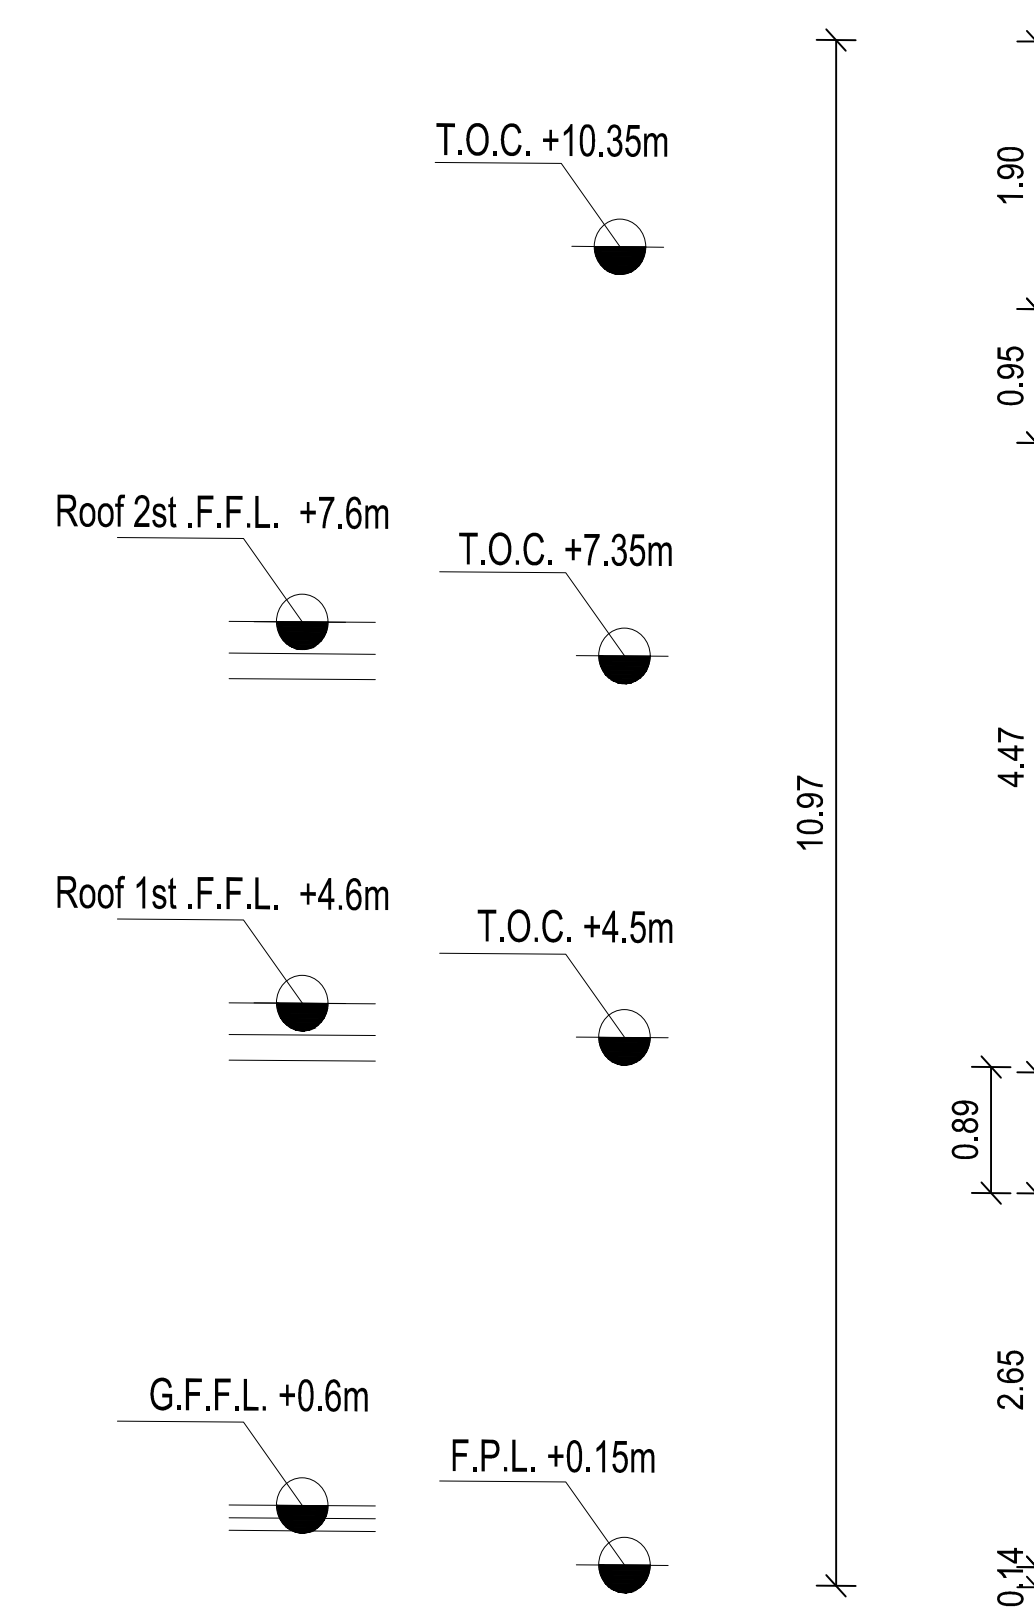

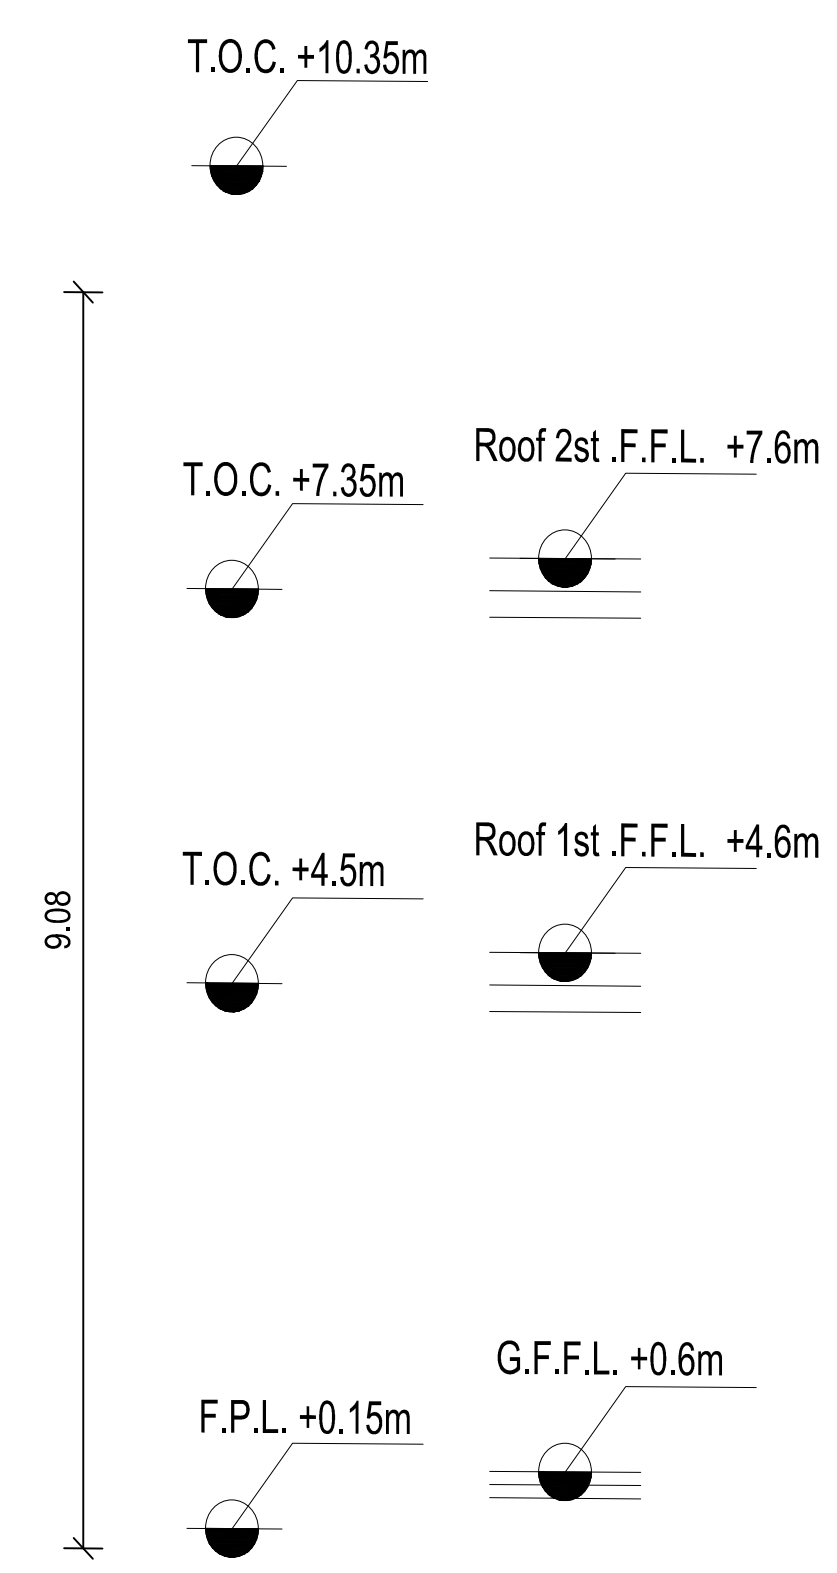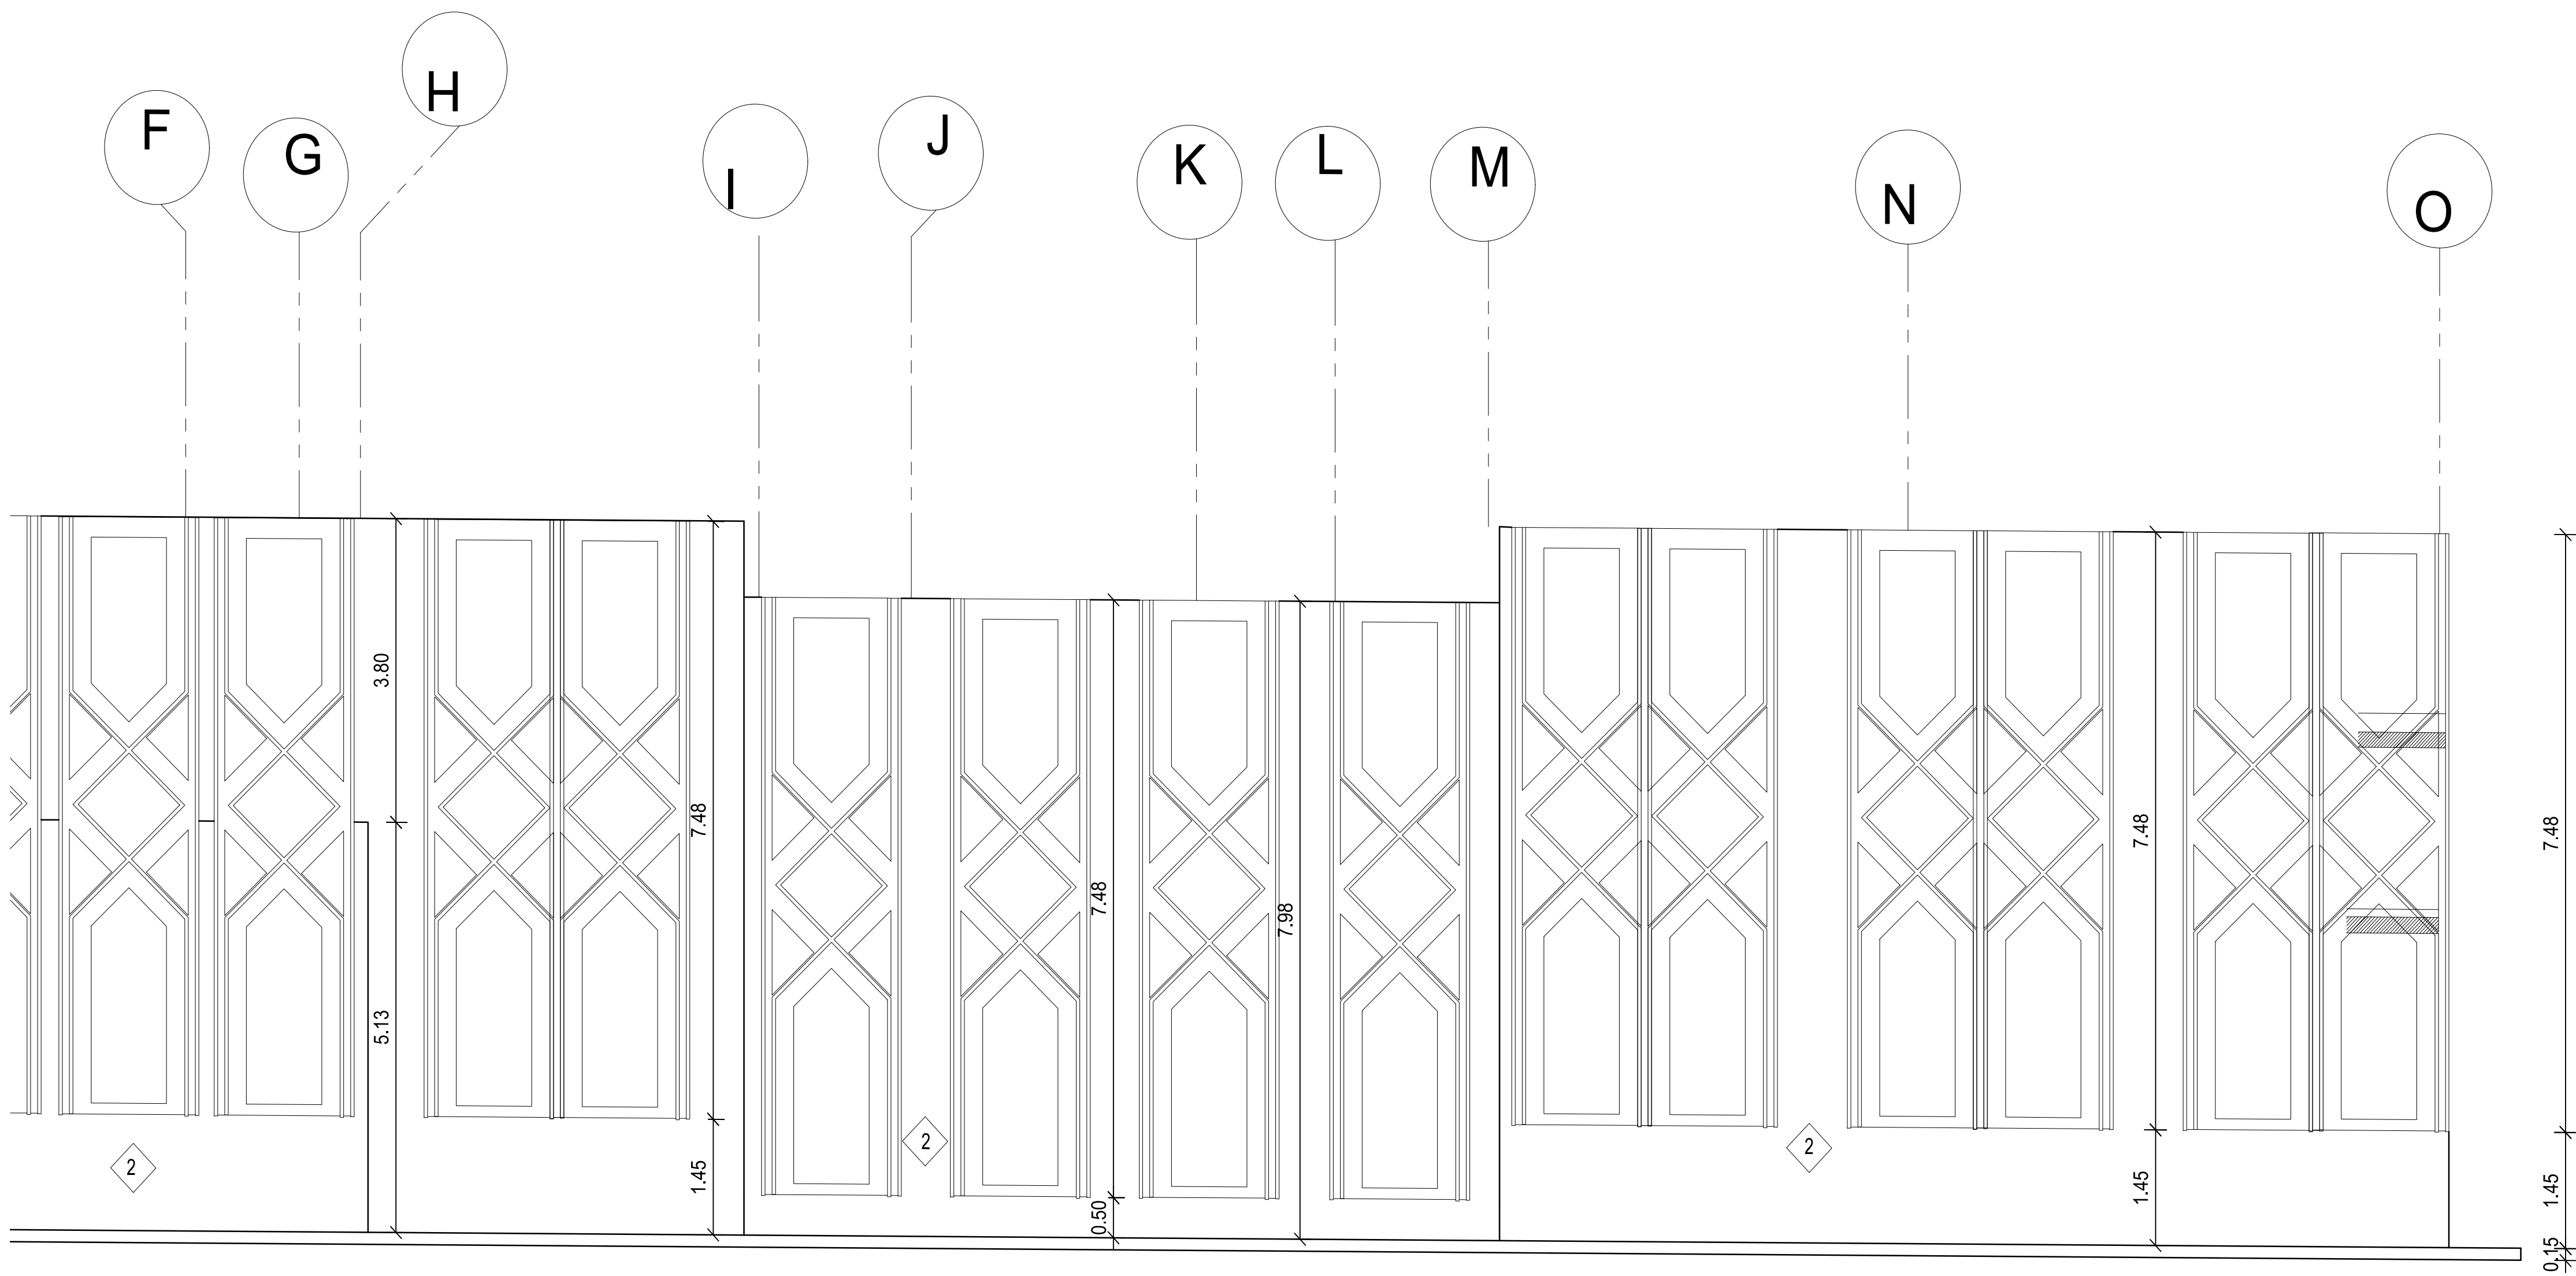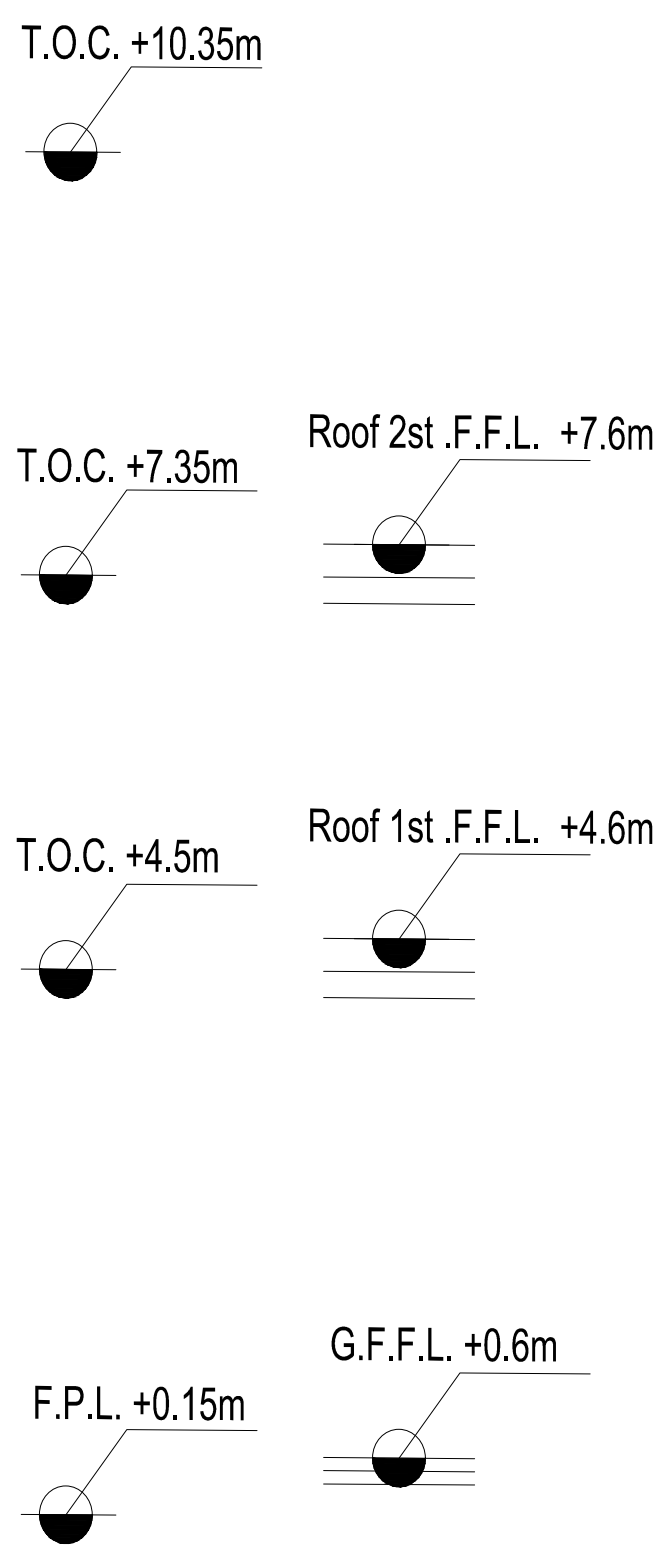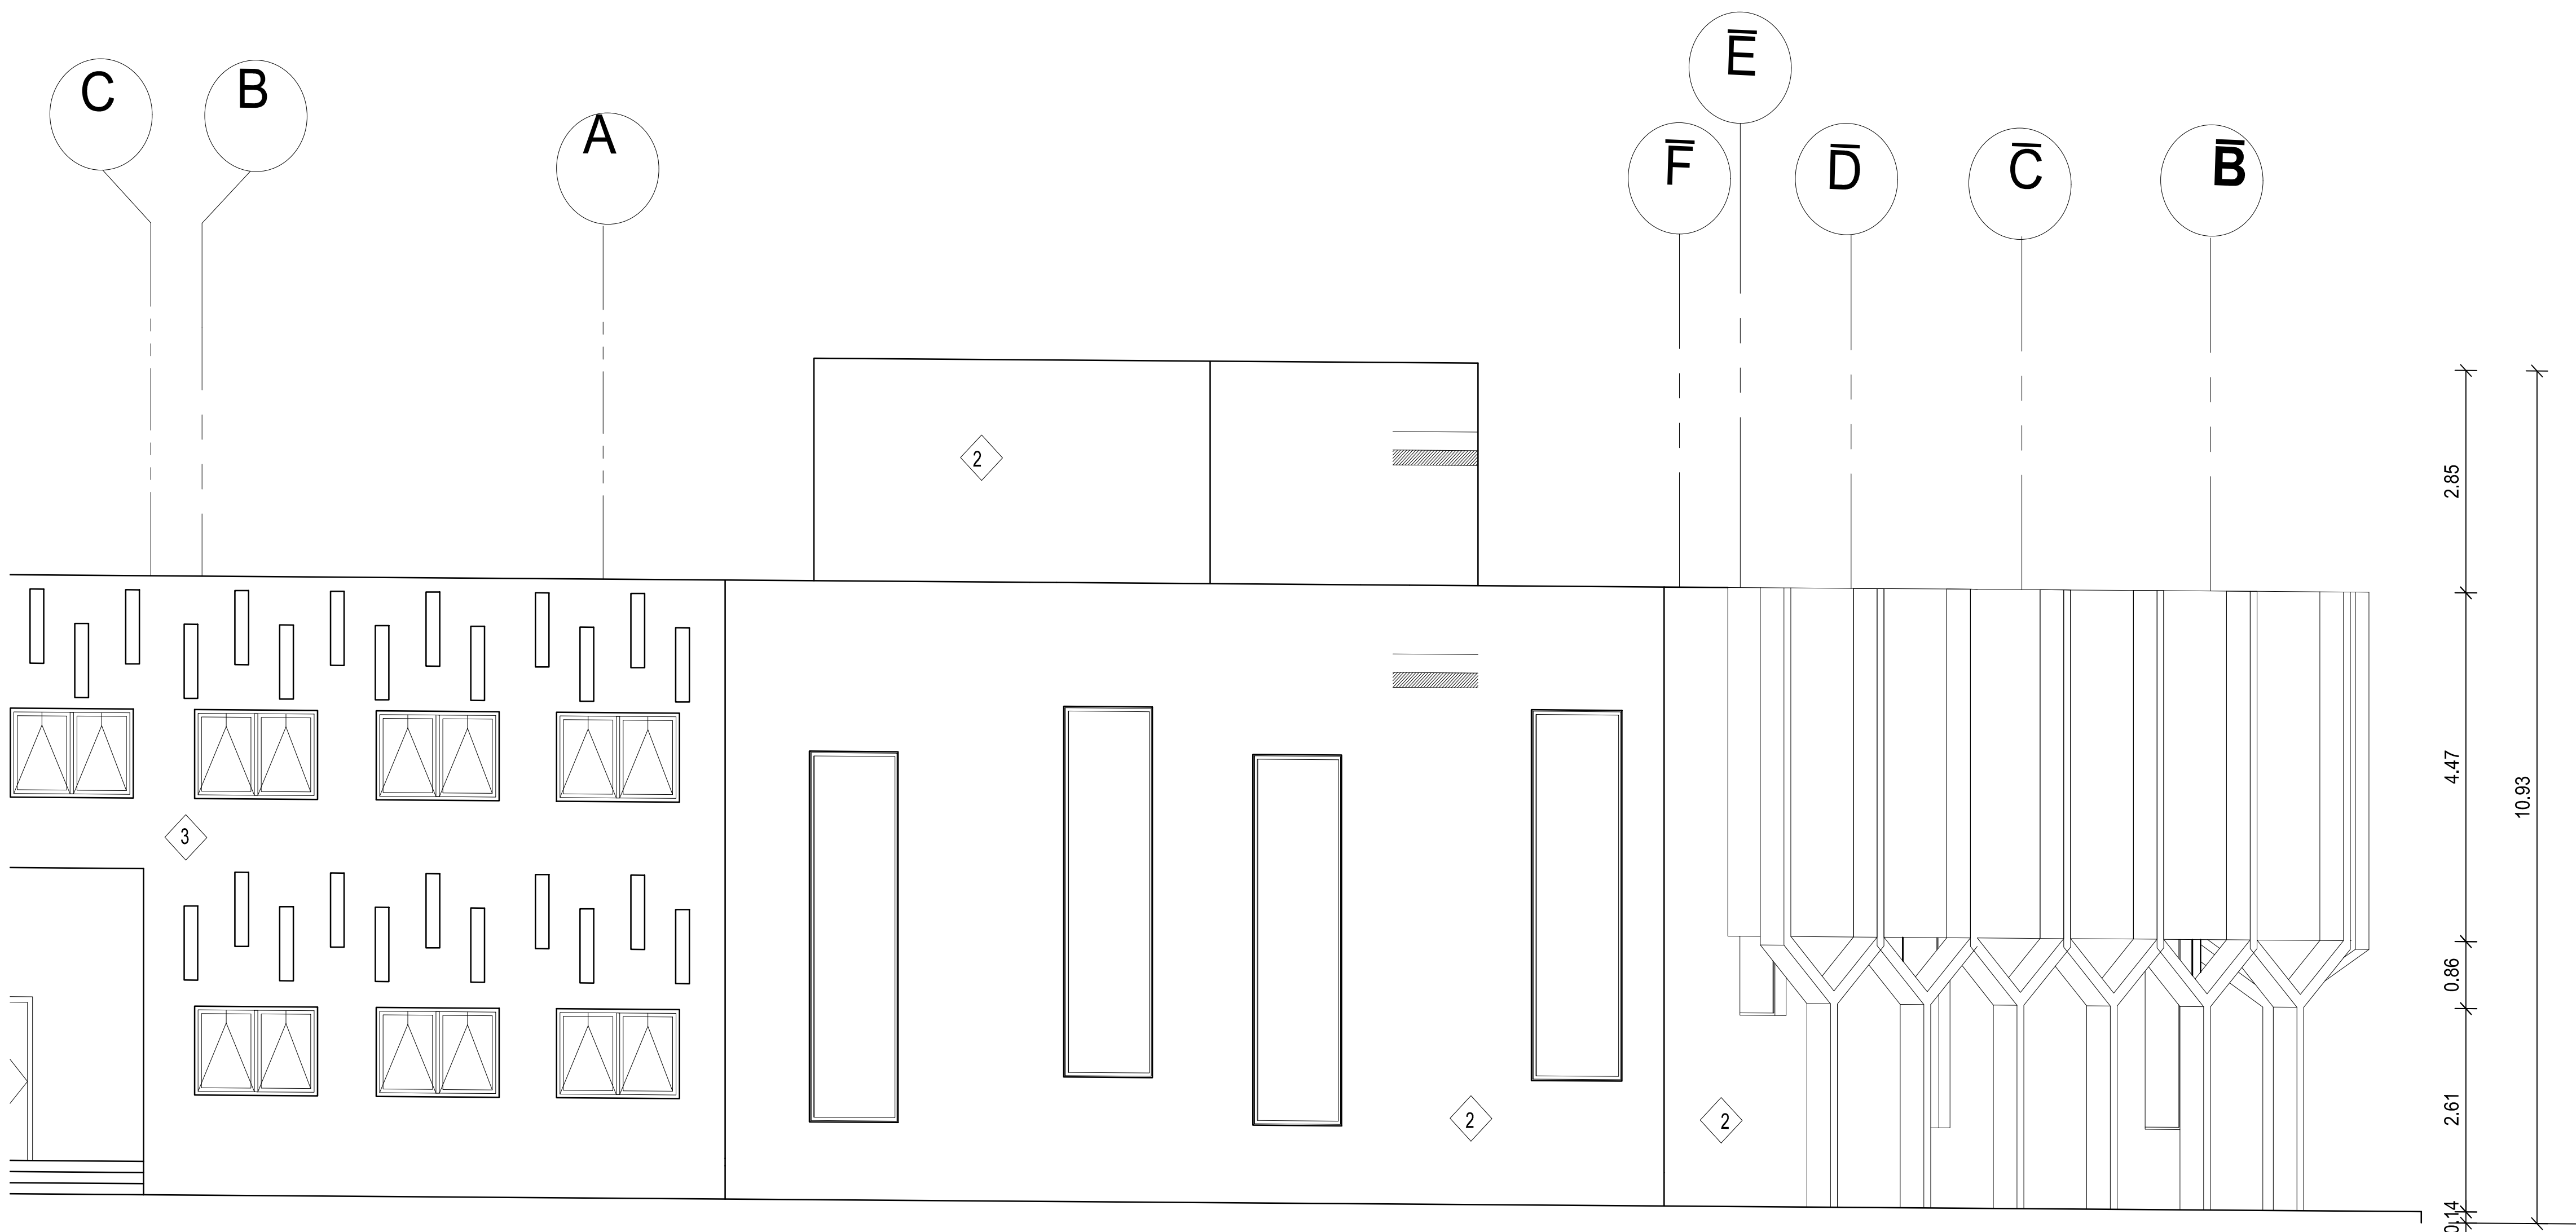

ABBREVIATIONS :

ABV.	DISCRIPTION
F.F.L.	FINISH FLOOR LEVEL
F.P.L.	FINISH PAVEMENT LEVEL
F.R.L.	FINISH ROAD LEVEL
T.O.C.	TOP OF CONCRETE
B.F.F.L.	BASEMENT FINISH FLOOR LEVEL
G.F.F.L.	GROUND FINISH FLOOR LEVEL
O.C.	ORDINARY CONCRETE
R.C.	REINFORCED CONCRETE
Thick.	THICKNESS



EXTERIOR WALLS


SYMBOL	DESCRIPTION
1	Paint Finish (Matte Plastic Paint)
2	Cementitious Textured Plaster
3	Wood Cladding (WPC Panels)

Abdul rahman Ashraf


DR. MOHAMED AISAEED

GROUND FLOOR
SCALE 1:50

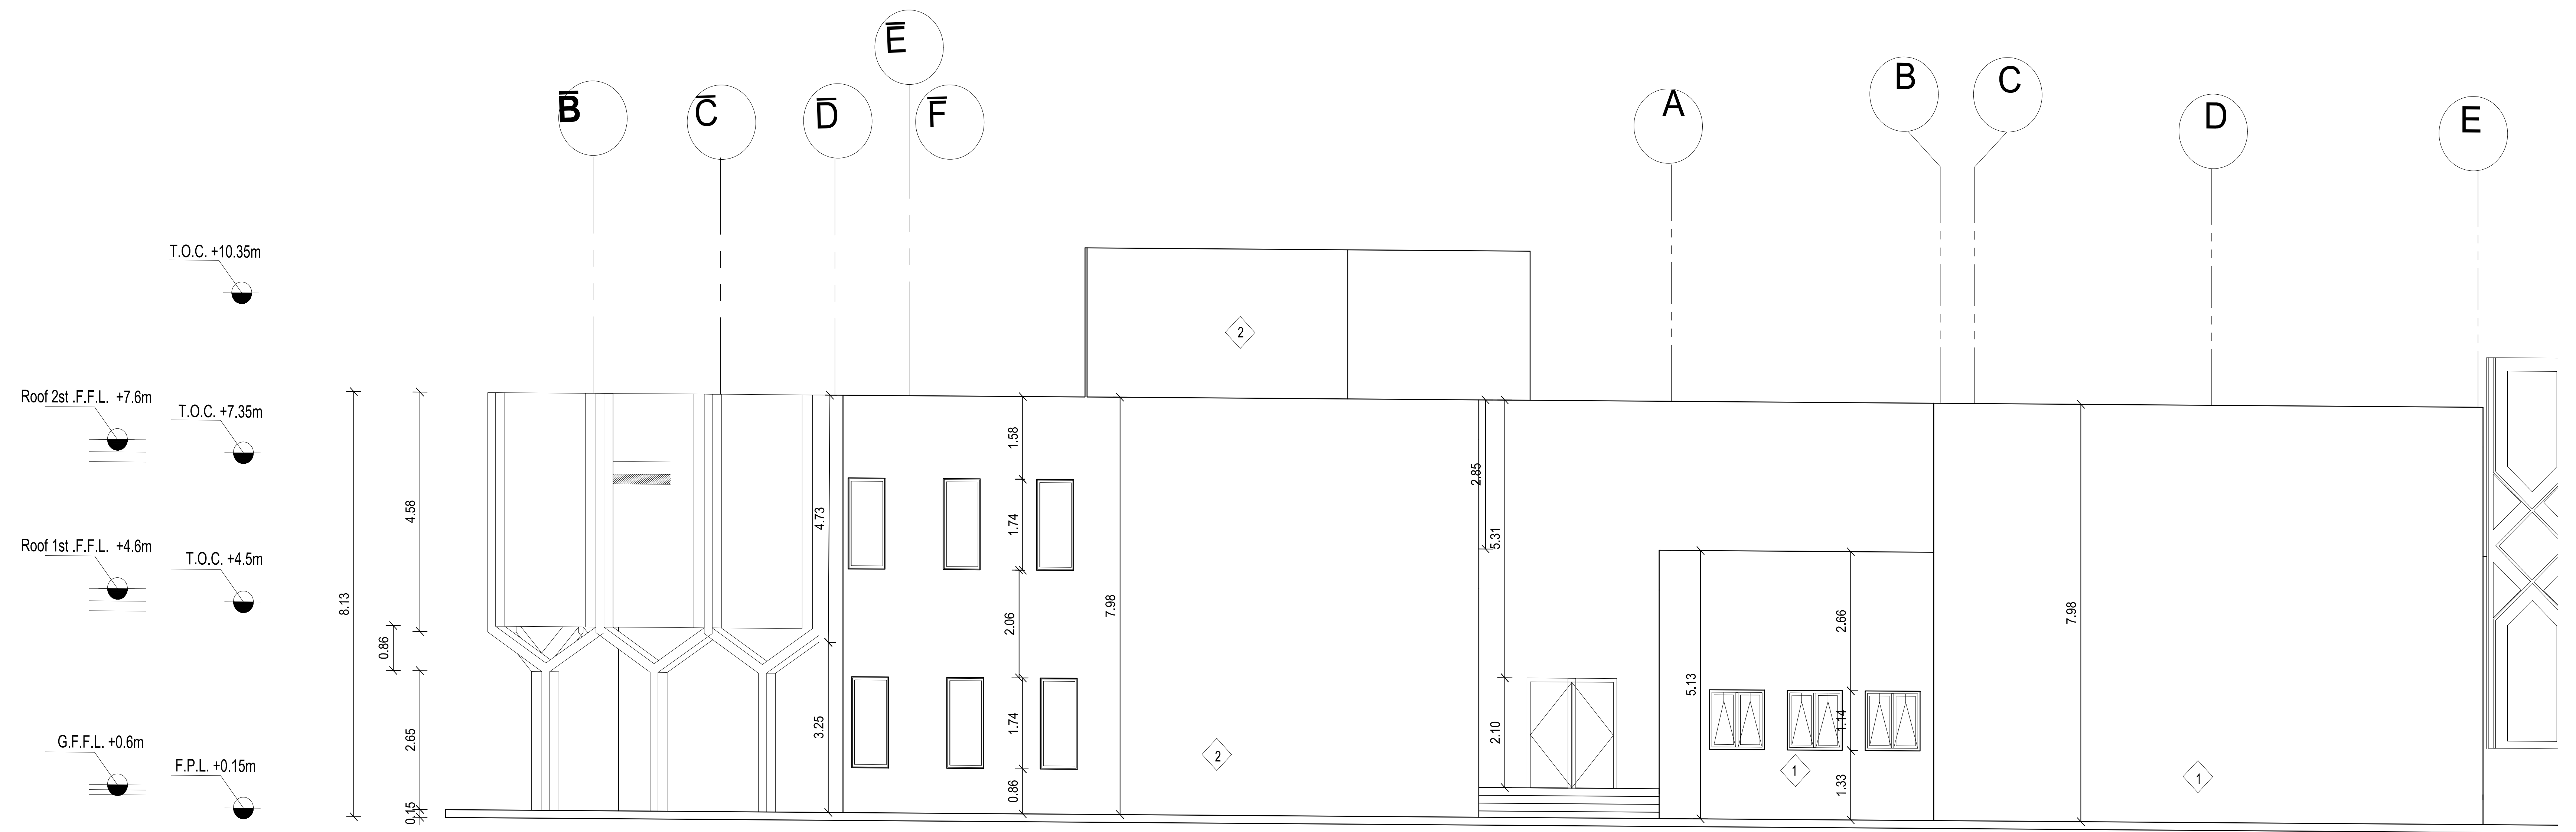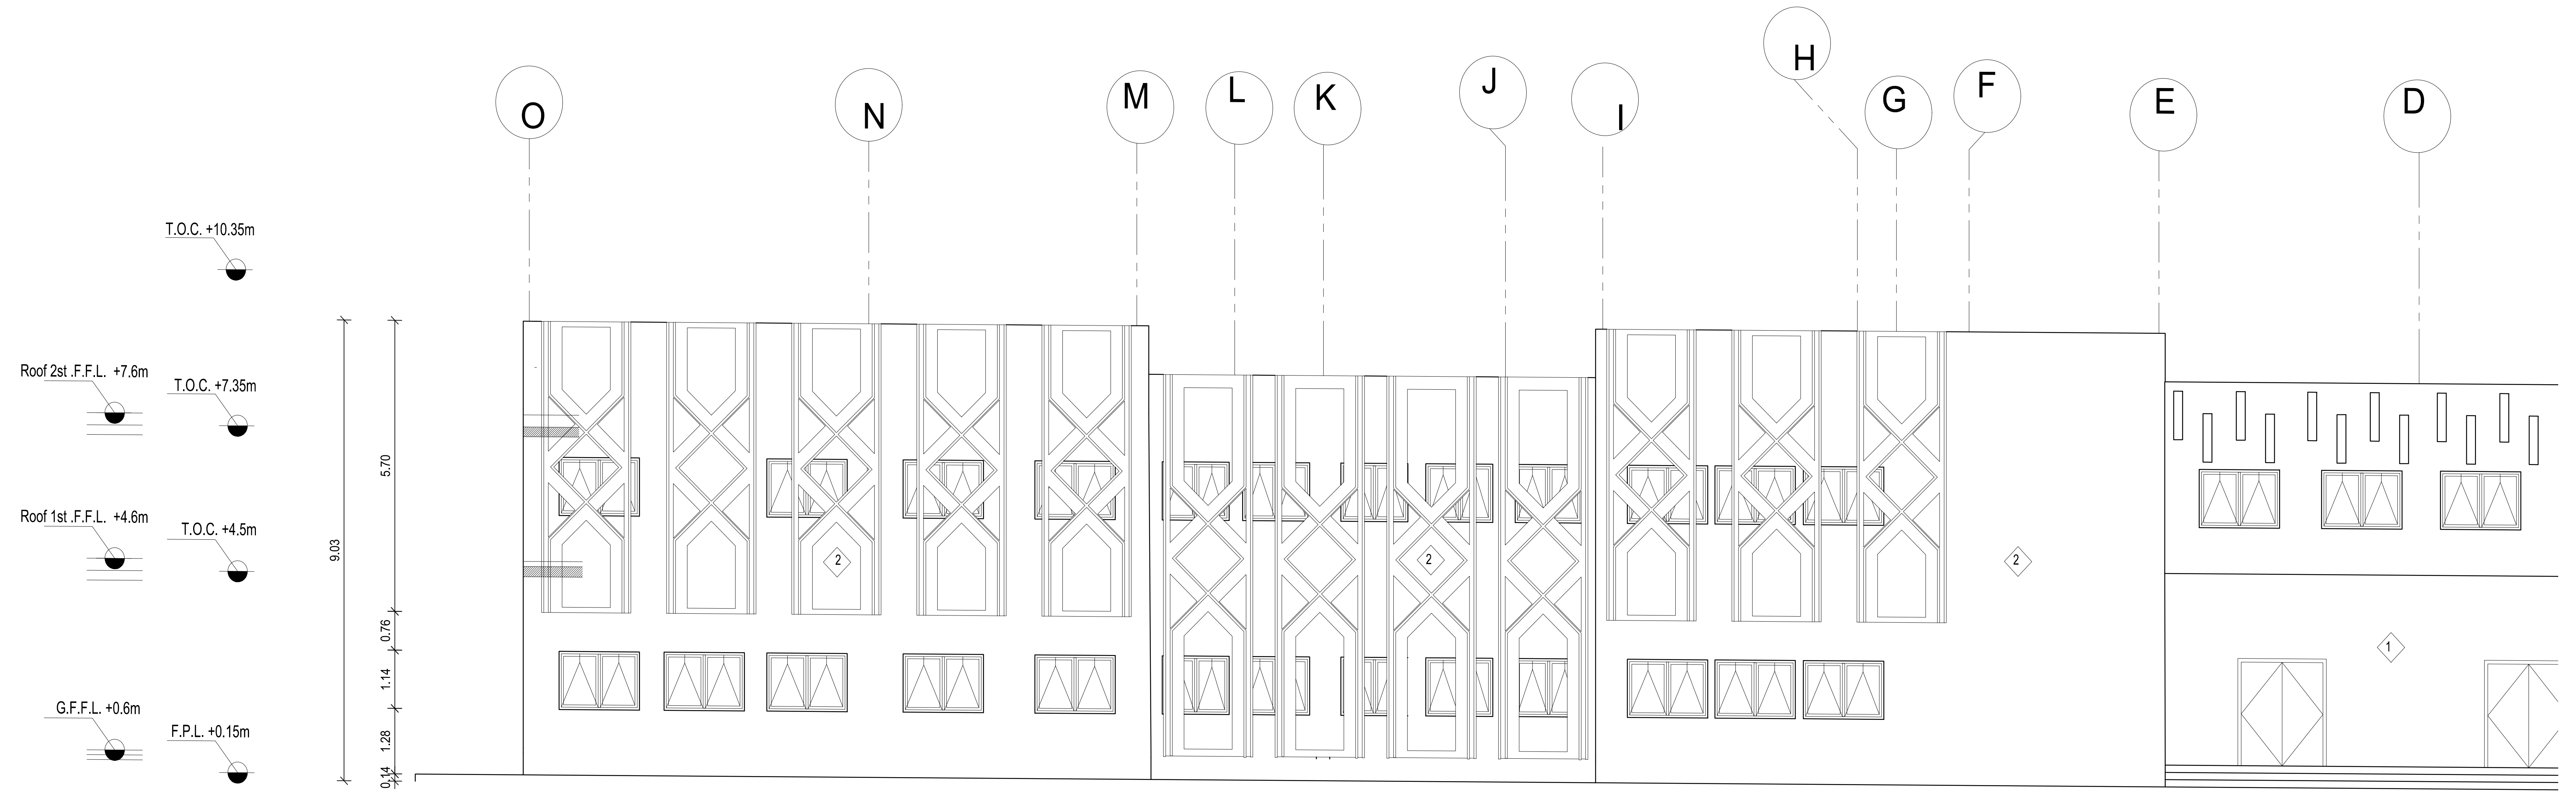

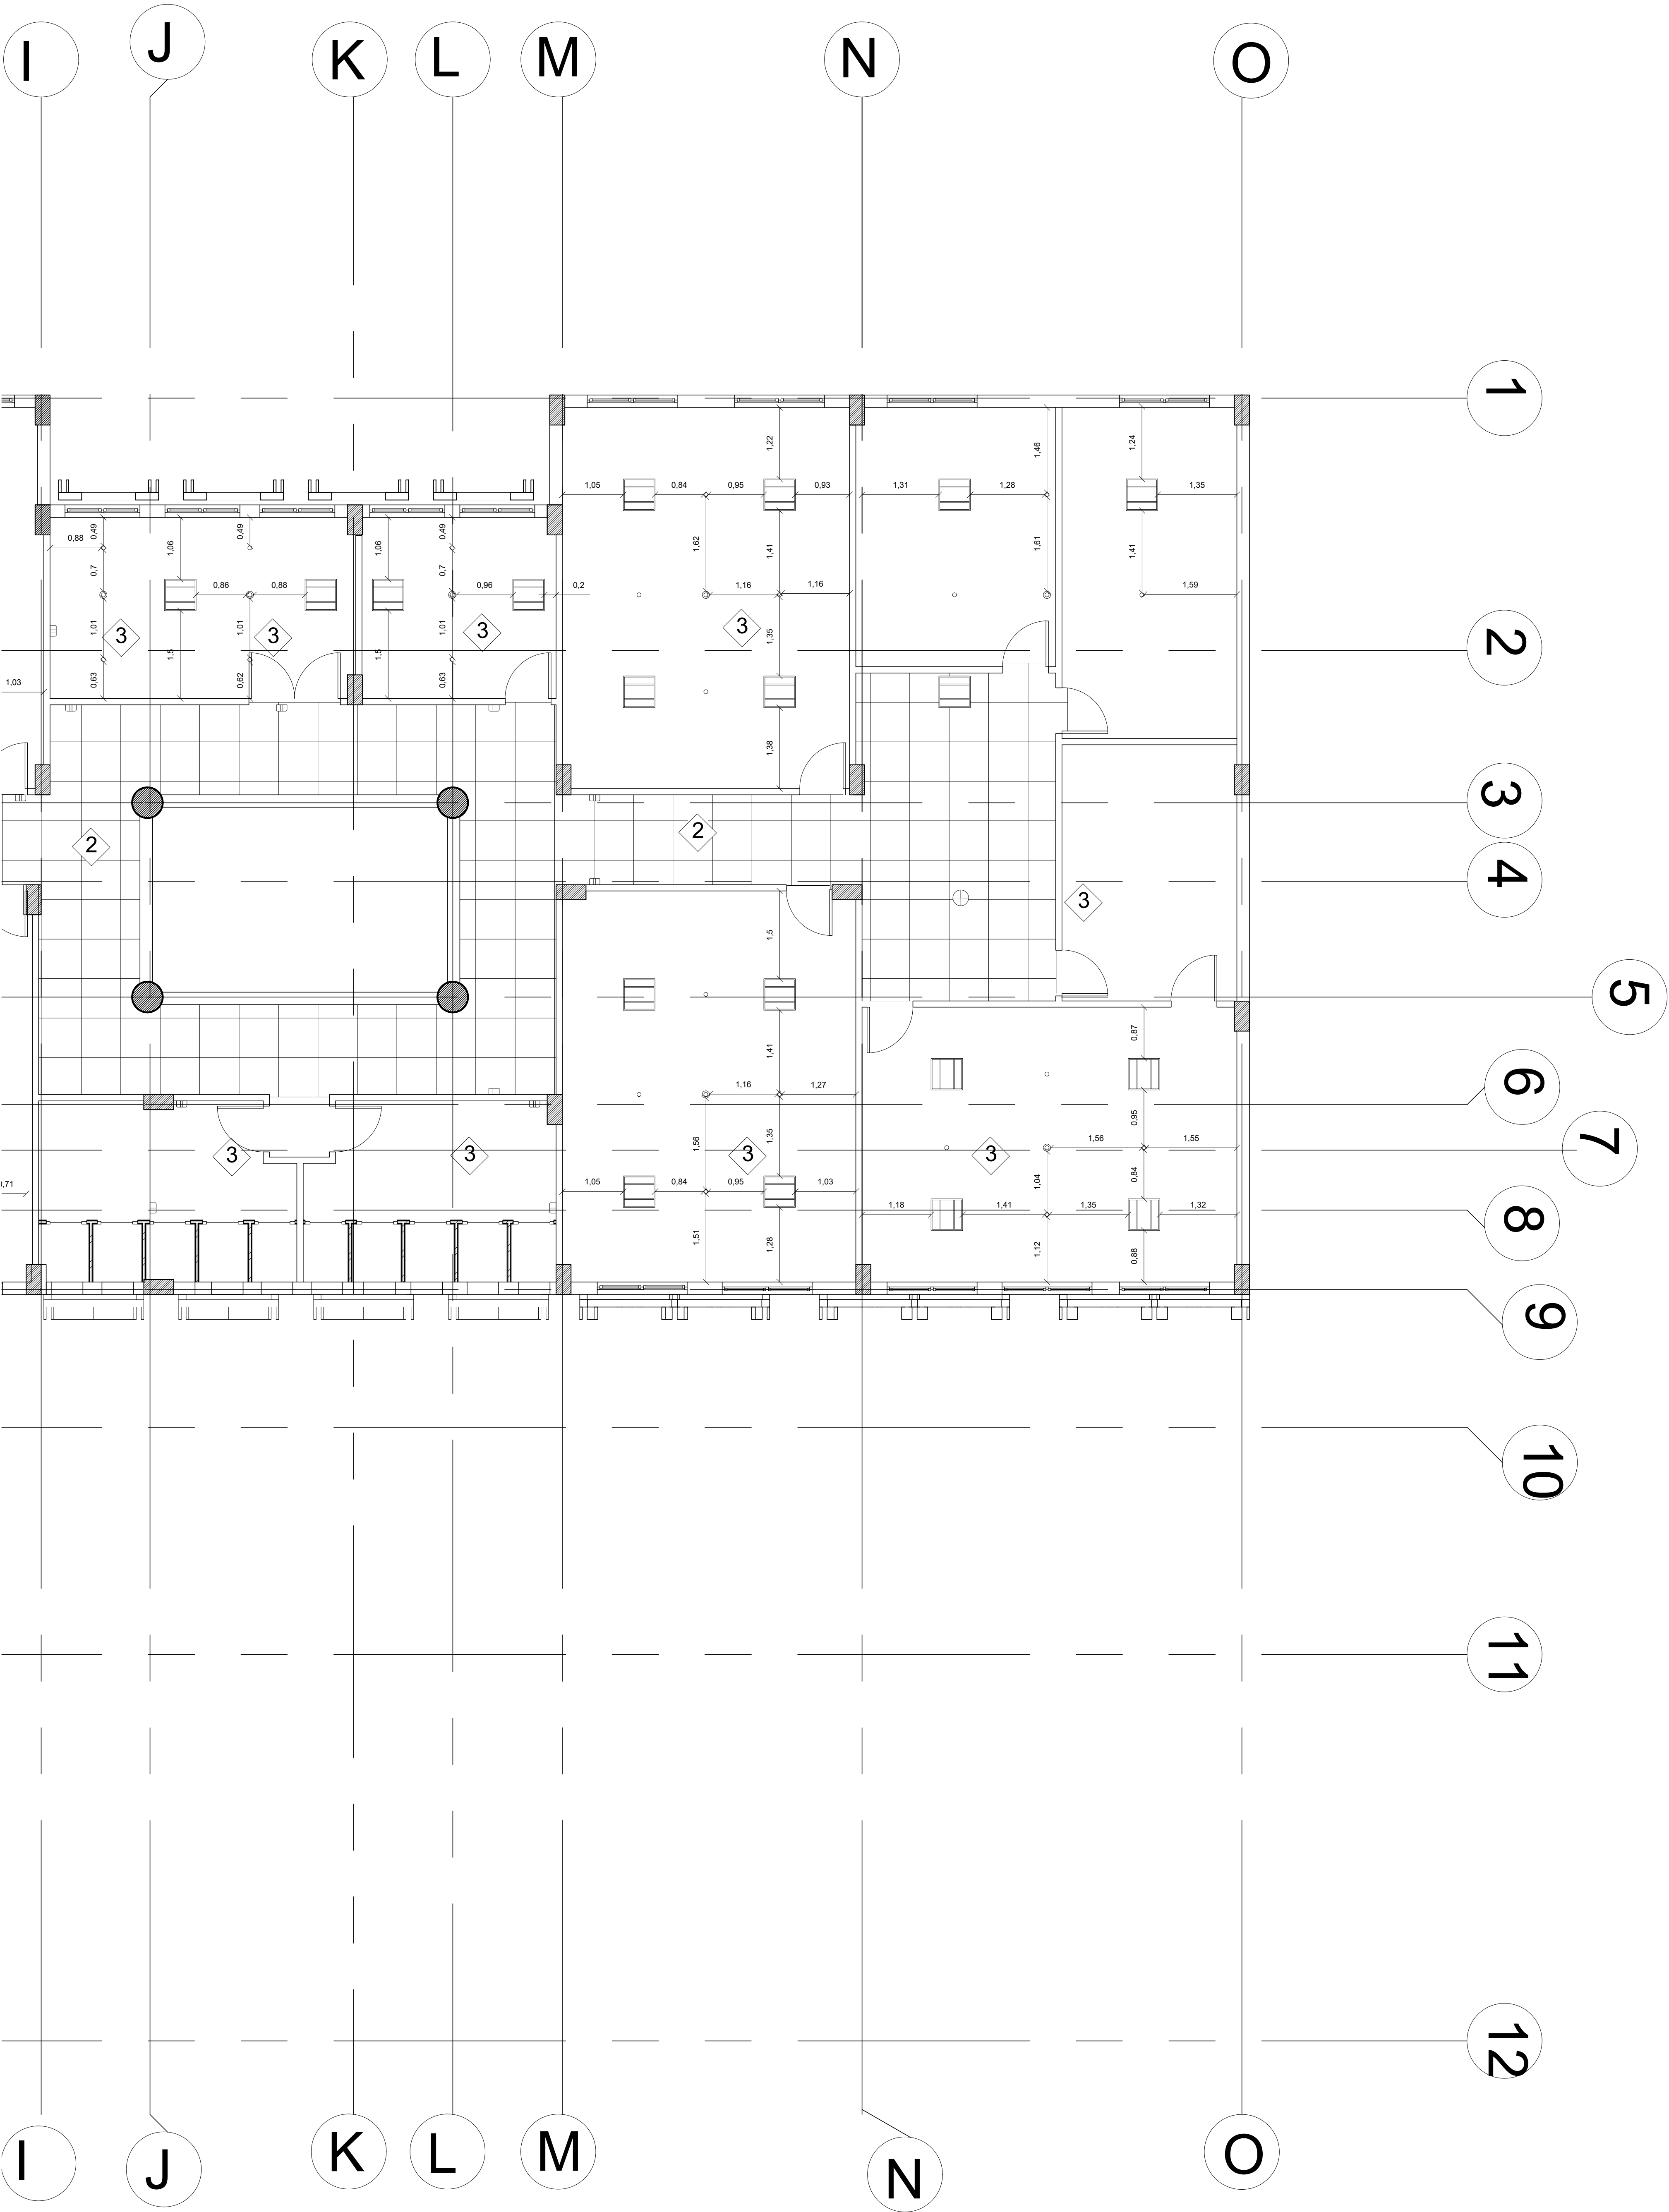

NORTH

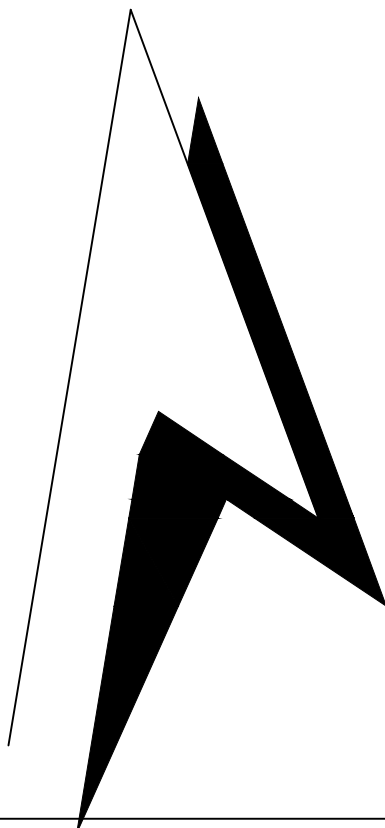

Ceiling


No.	Description
1	expanded mesh covered with cement coating and finished with acrylic paint
2	metal tiles(60x60cm) susbended ceiling
3	acrylic paint over cement coating
4	gypsum boards susbended ceiling


Symbol	Description
	recess luminair with semispecular louvers for 2x40w flourescent lamps (60x60 cm)
	luminair with semispecular cover for 2x9w lamps (D=29cm)
	side luminair with semispecular cover for 1x9w lamps (29x18x12cm)
	smoke detector
	sprinkler head

Abdul rahman Ashraf


DR. MOHAMED AISAED

GROUND FLOOR
SCALE 1:50

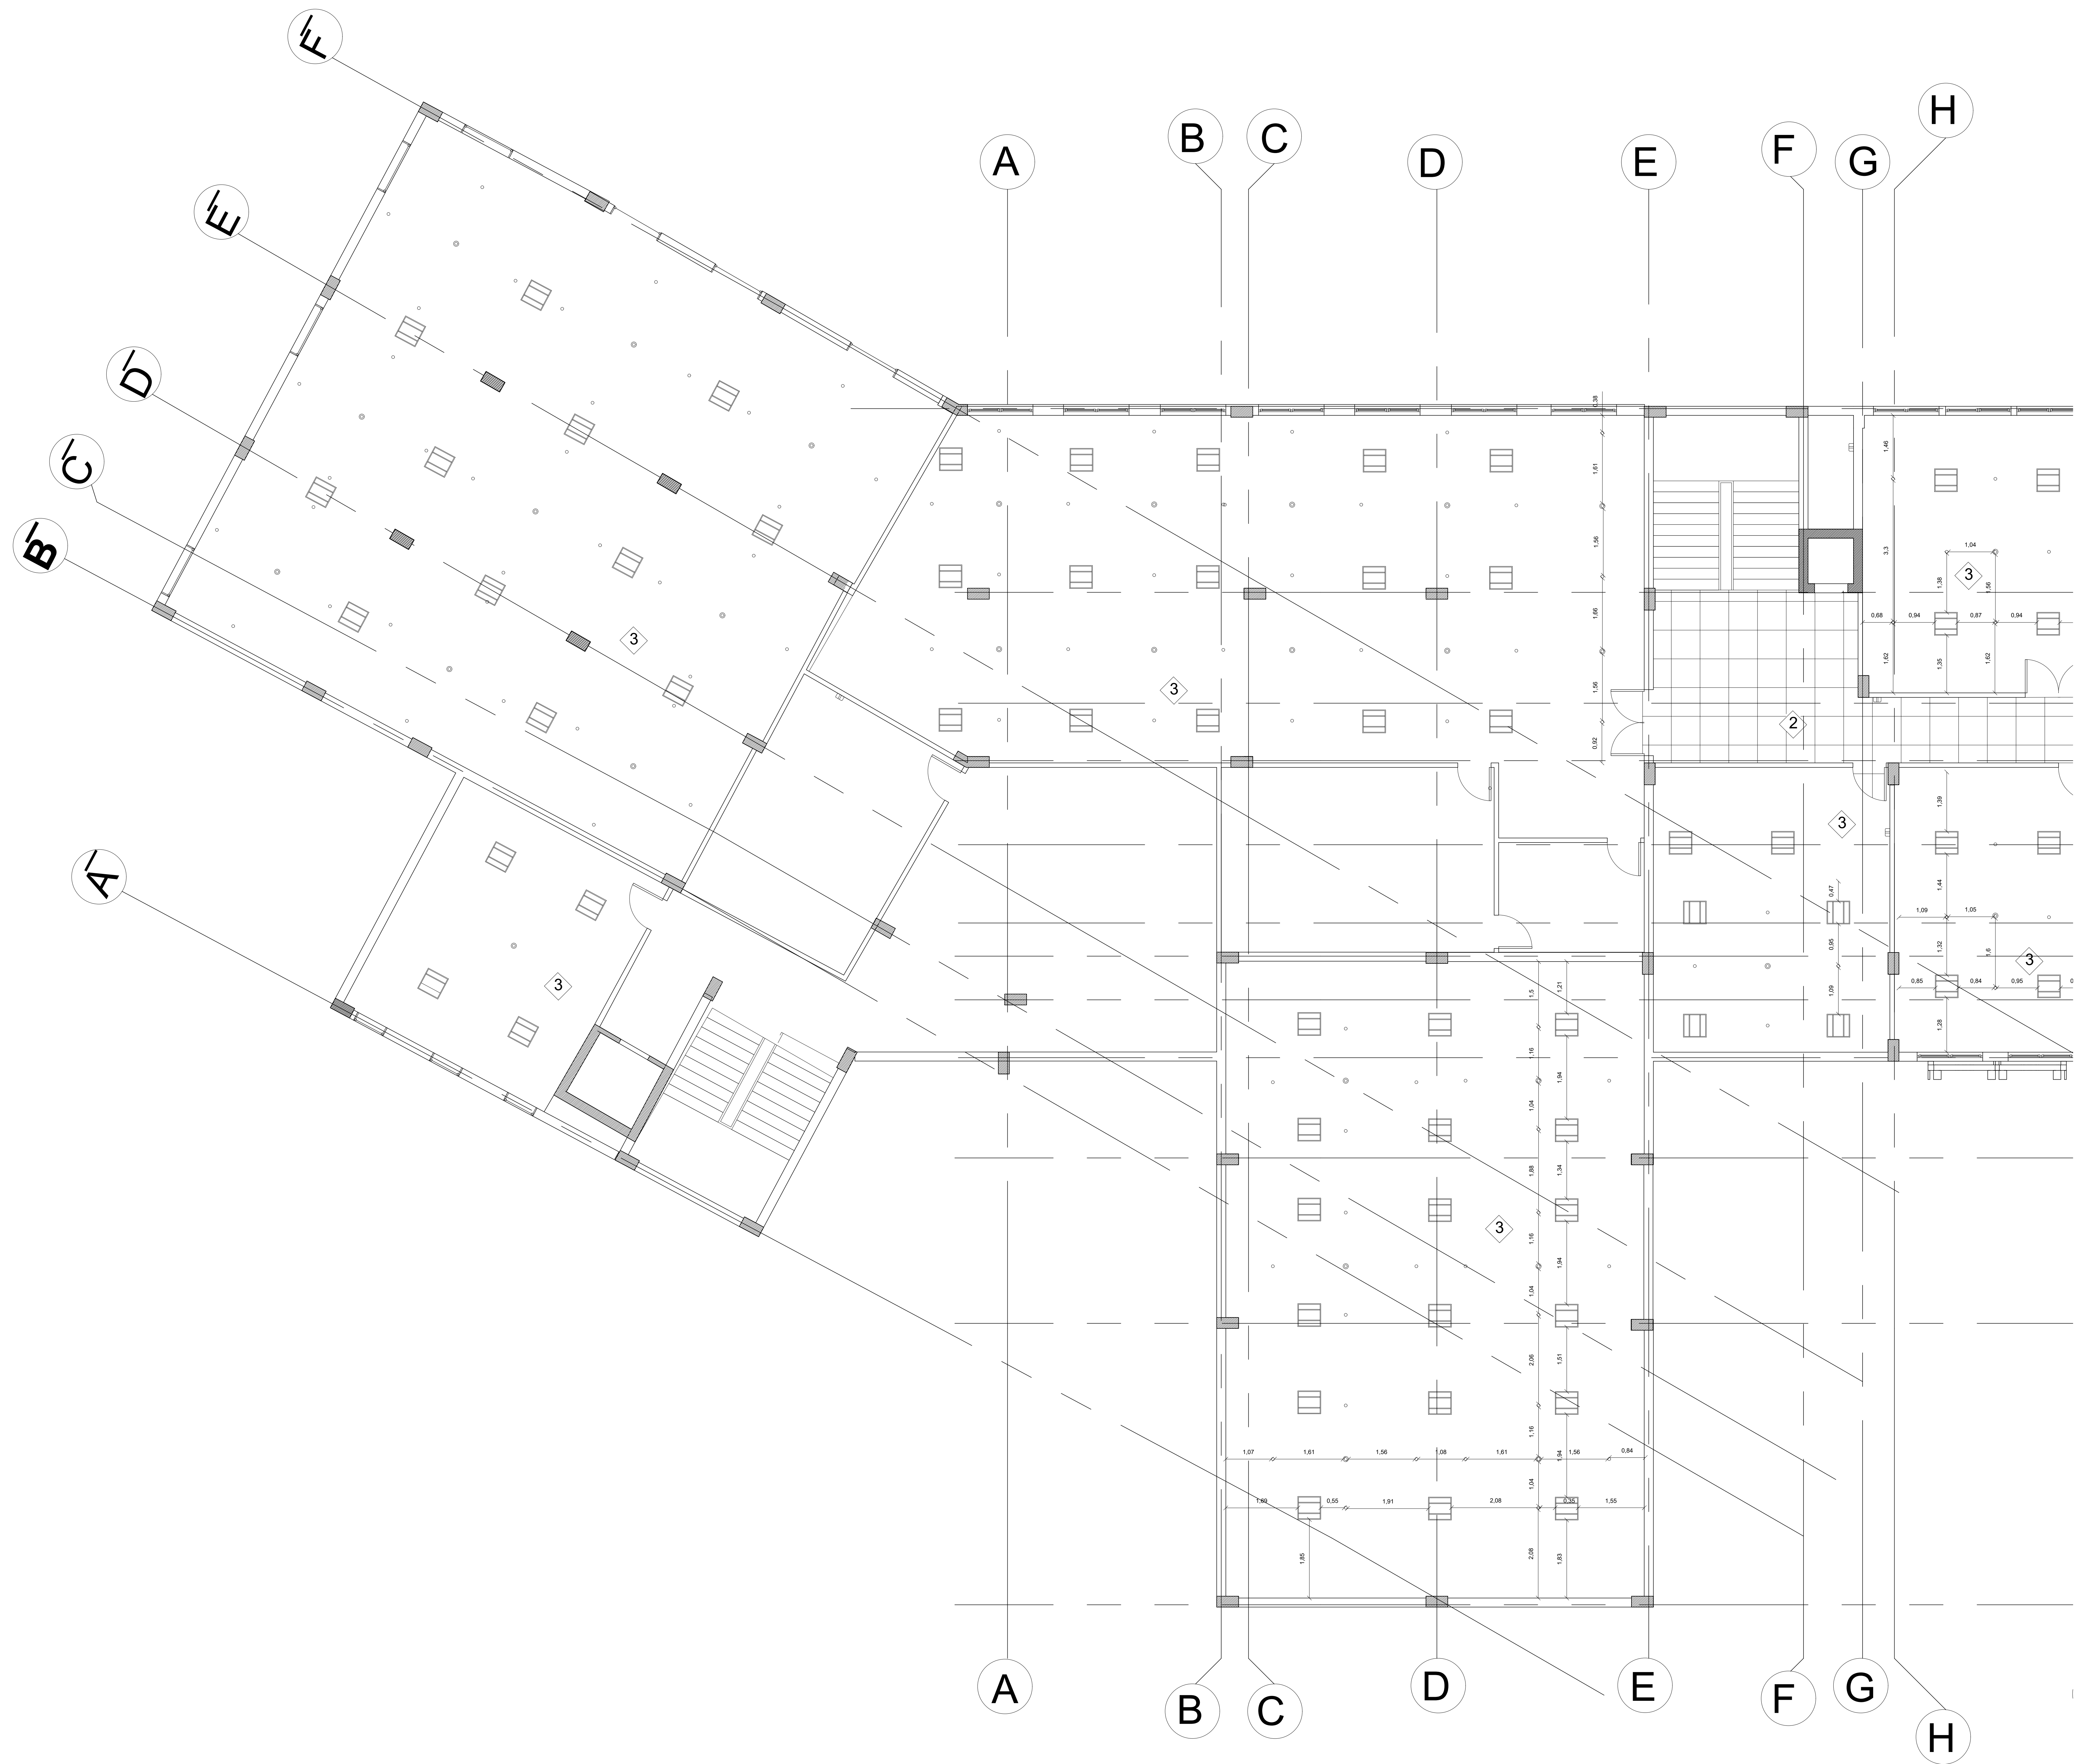

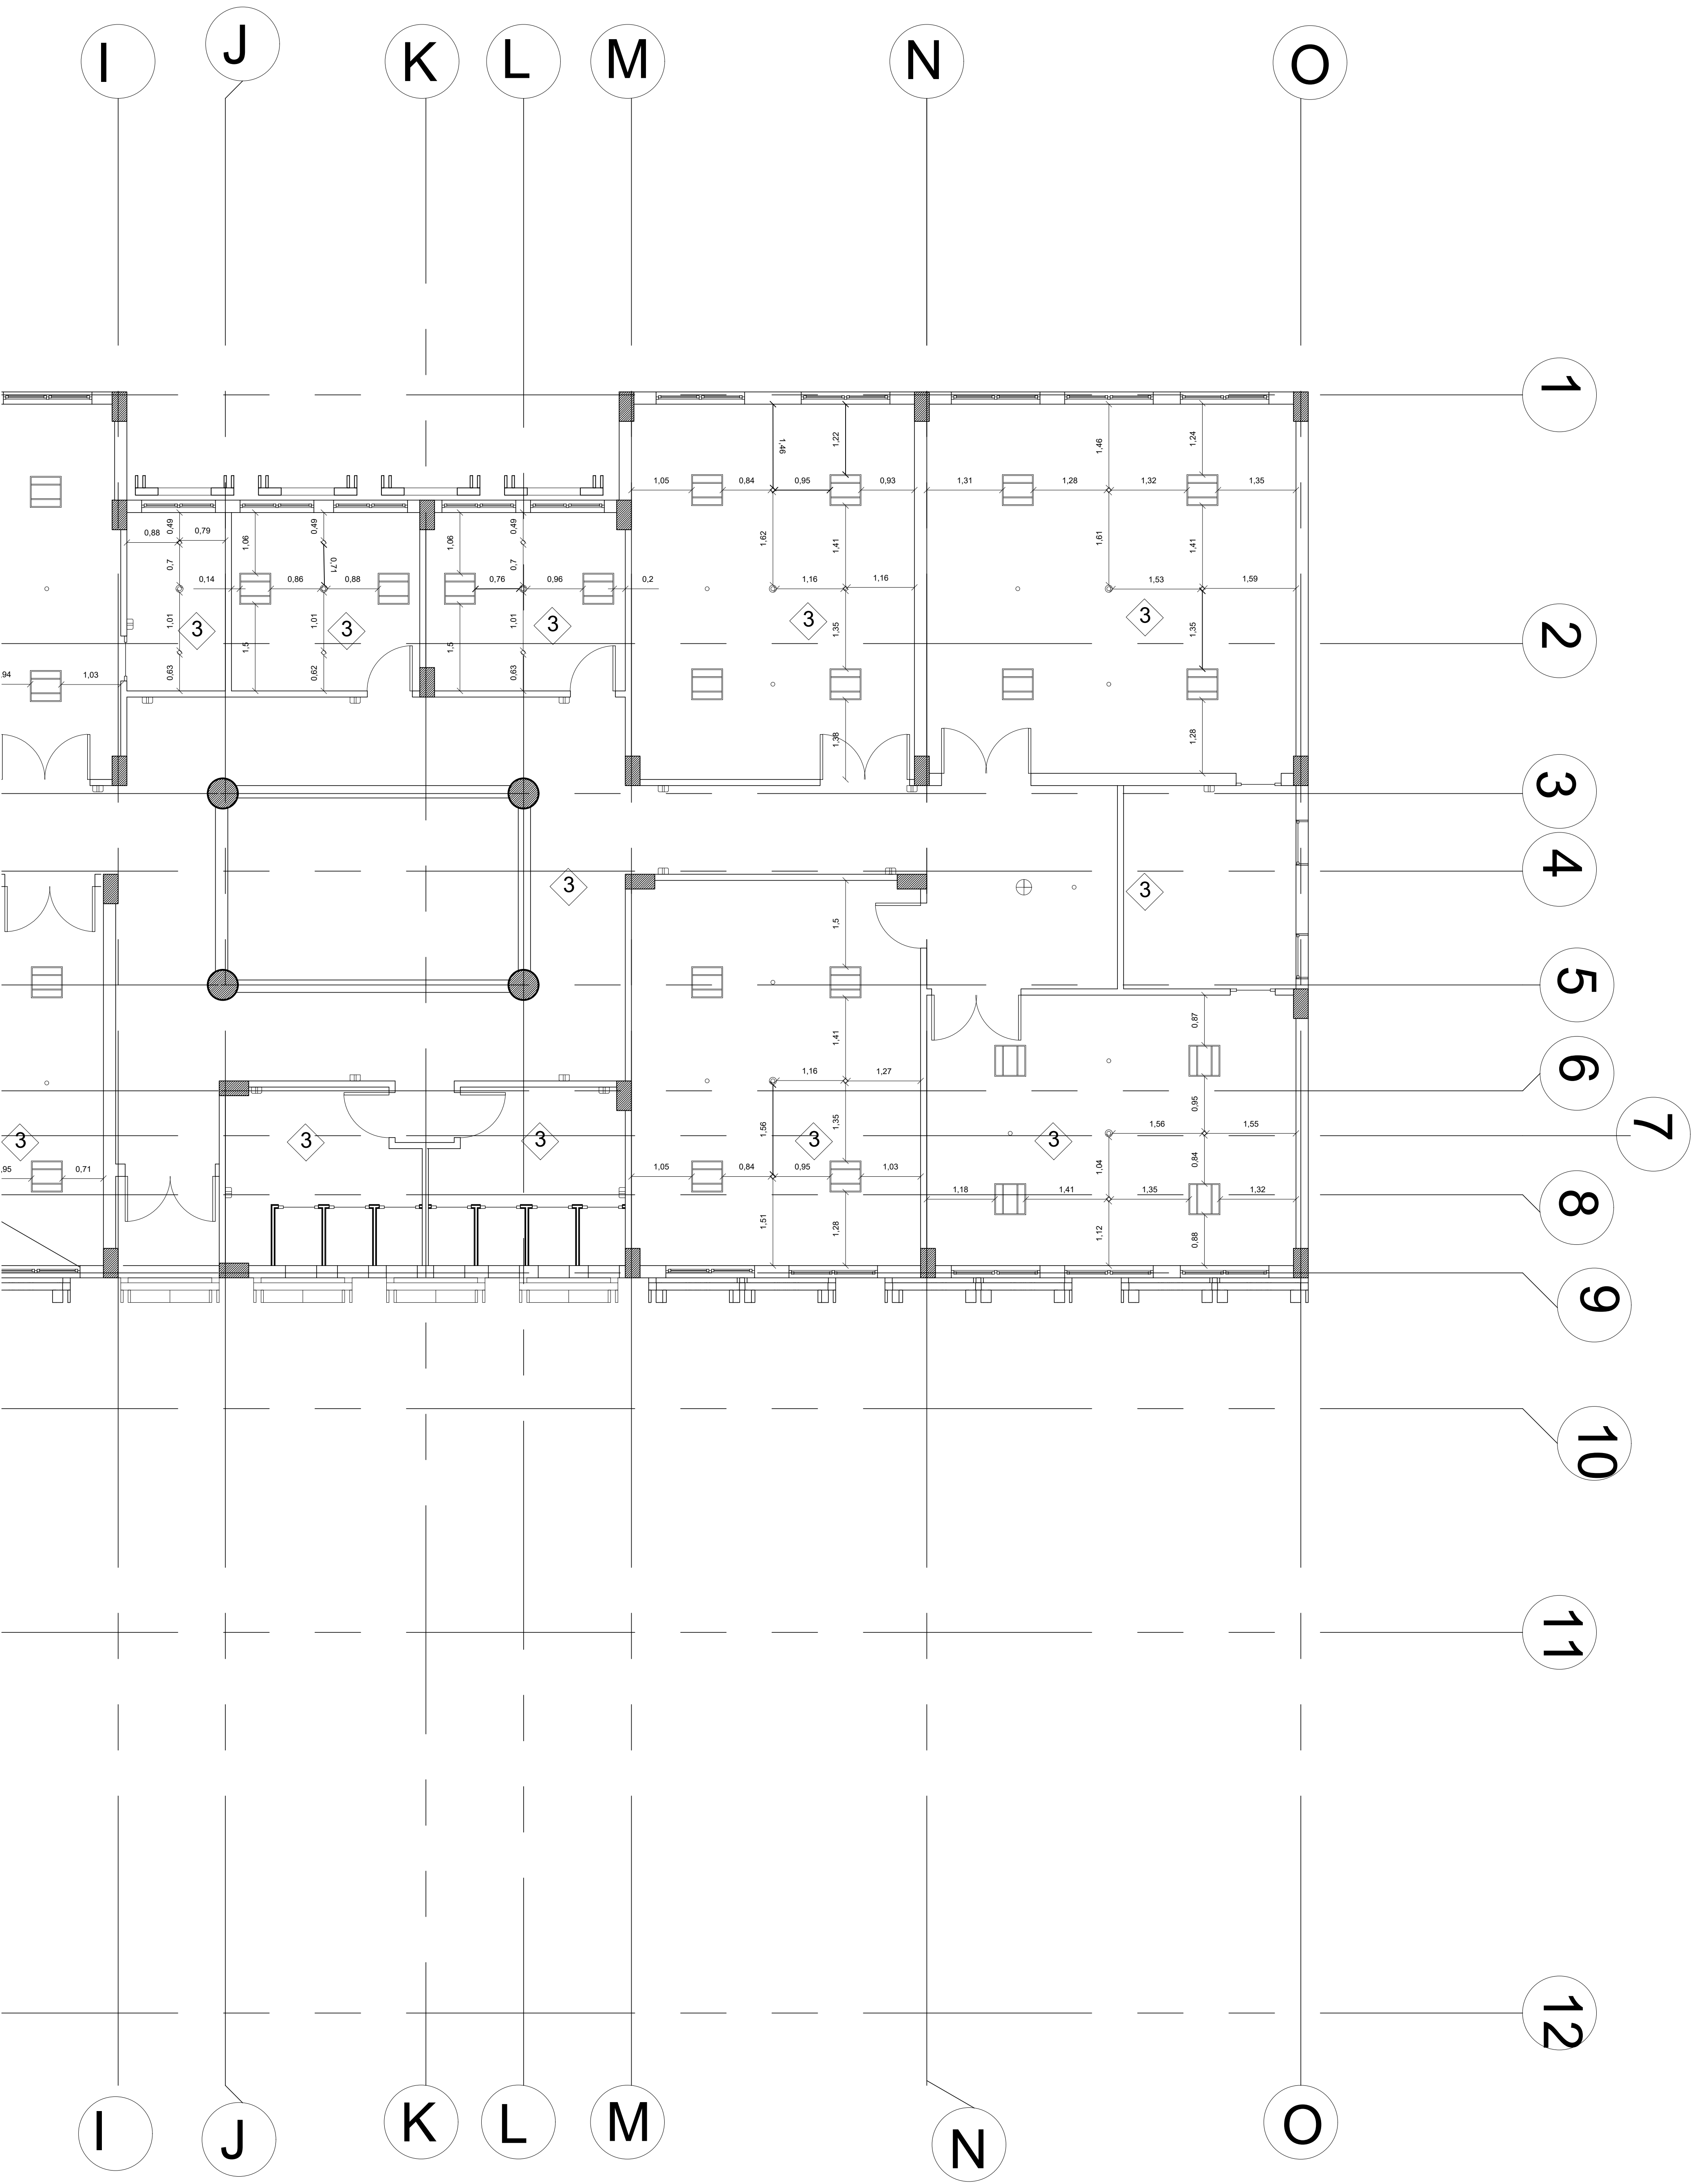

NORTH

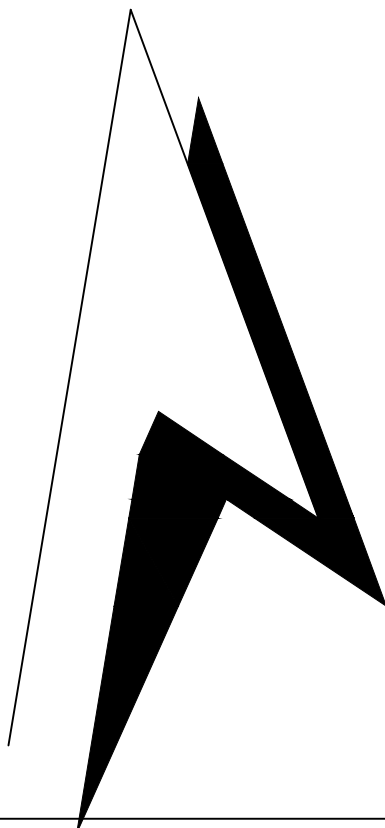

Ceiling


No.	Description
1	expanded mesh covered with cement coating and finished with acrylic paint
2	metal tiles(60x60cm) subsended ceiling
3	acrylic paint over cement coating
4	gypsum boards subsended ceiling

Symbol	Description
	recess luminaire with semispecular louvers for 2x40w flourescent lamps (60x60 cm)
	luminaire with semispecular cover for 2x9w lamps (D=29cm)
	side luminaire with semispecular cover for 1x9w lamps (29x18x12cm)
	smoke detector
	sprinkler head


Abdul rahman Ashraf

DR. MOHAMED AISAED

GROUND FLOOR
SCALE 1:50

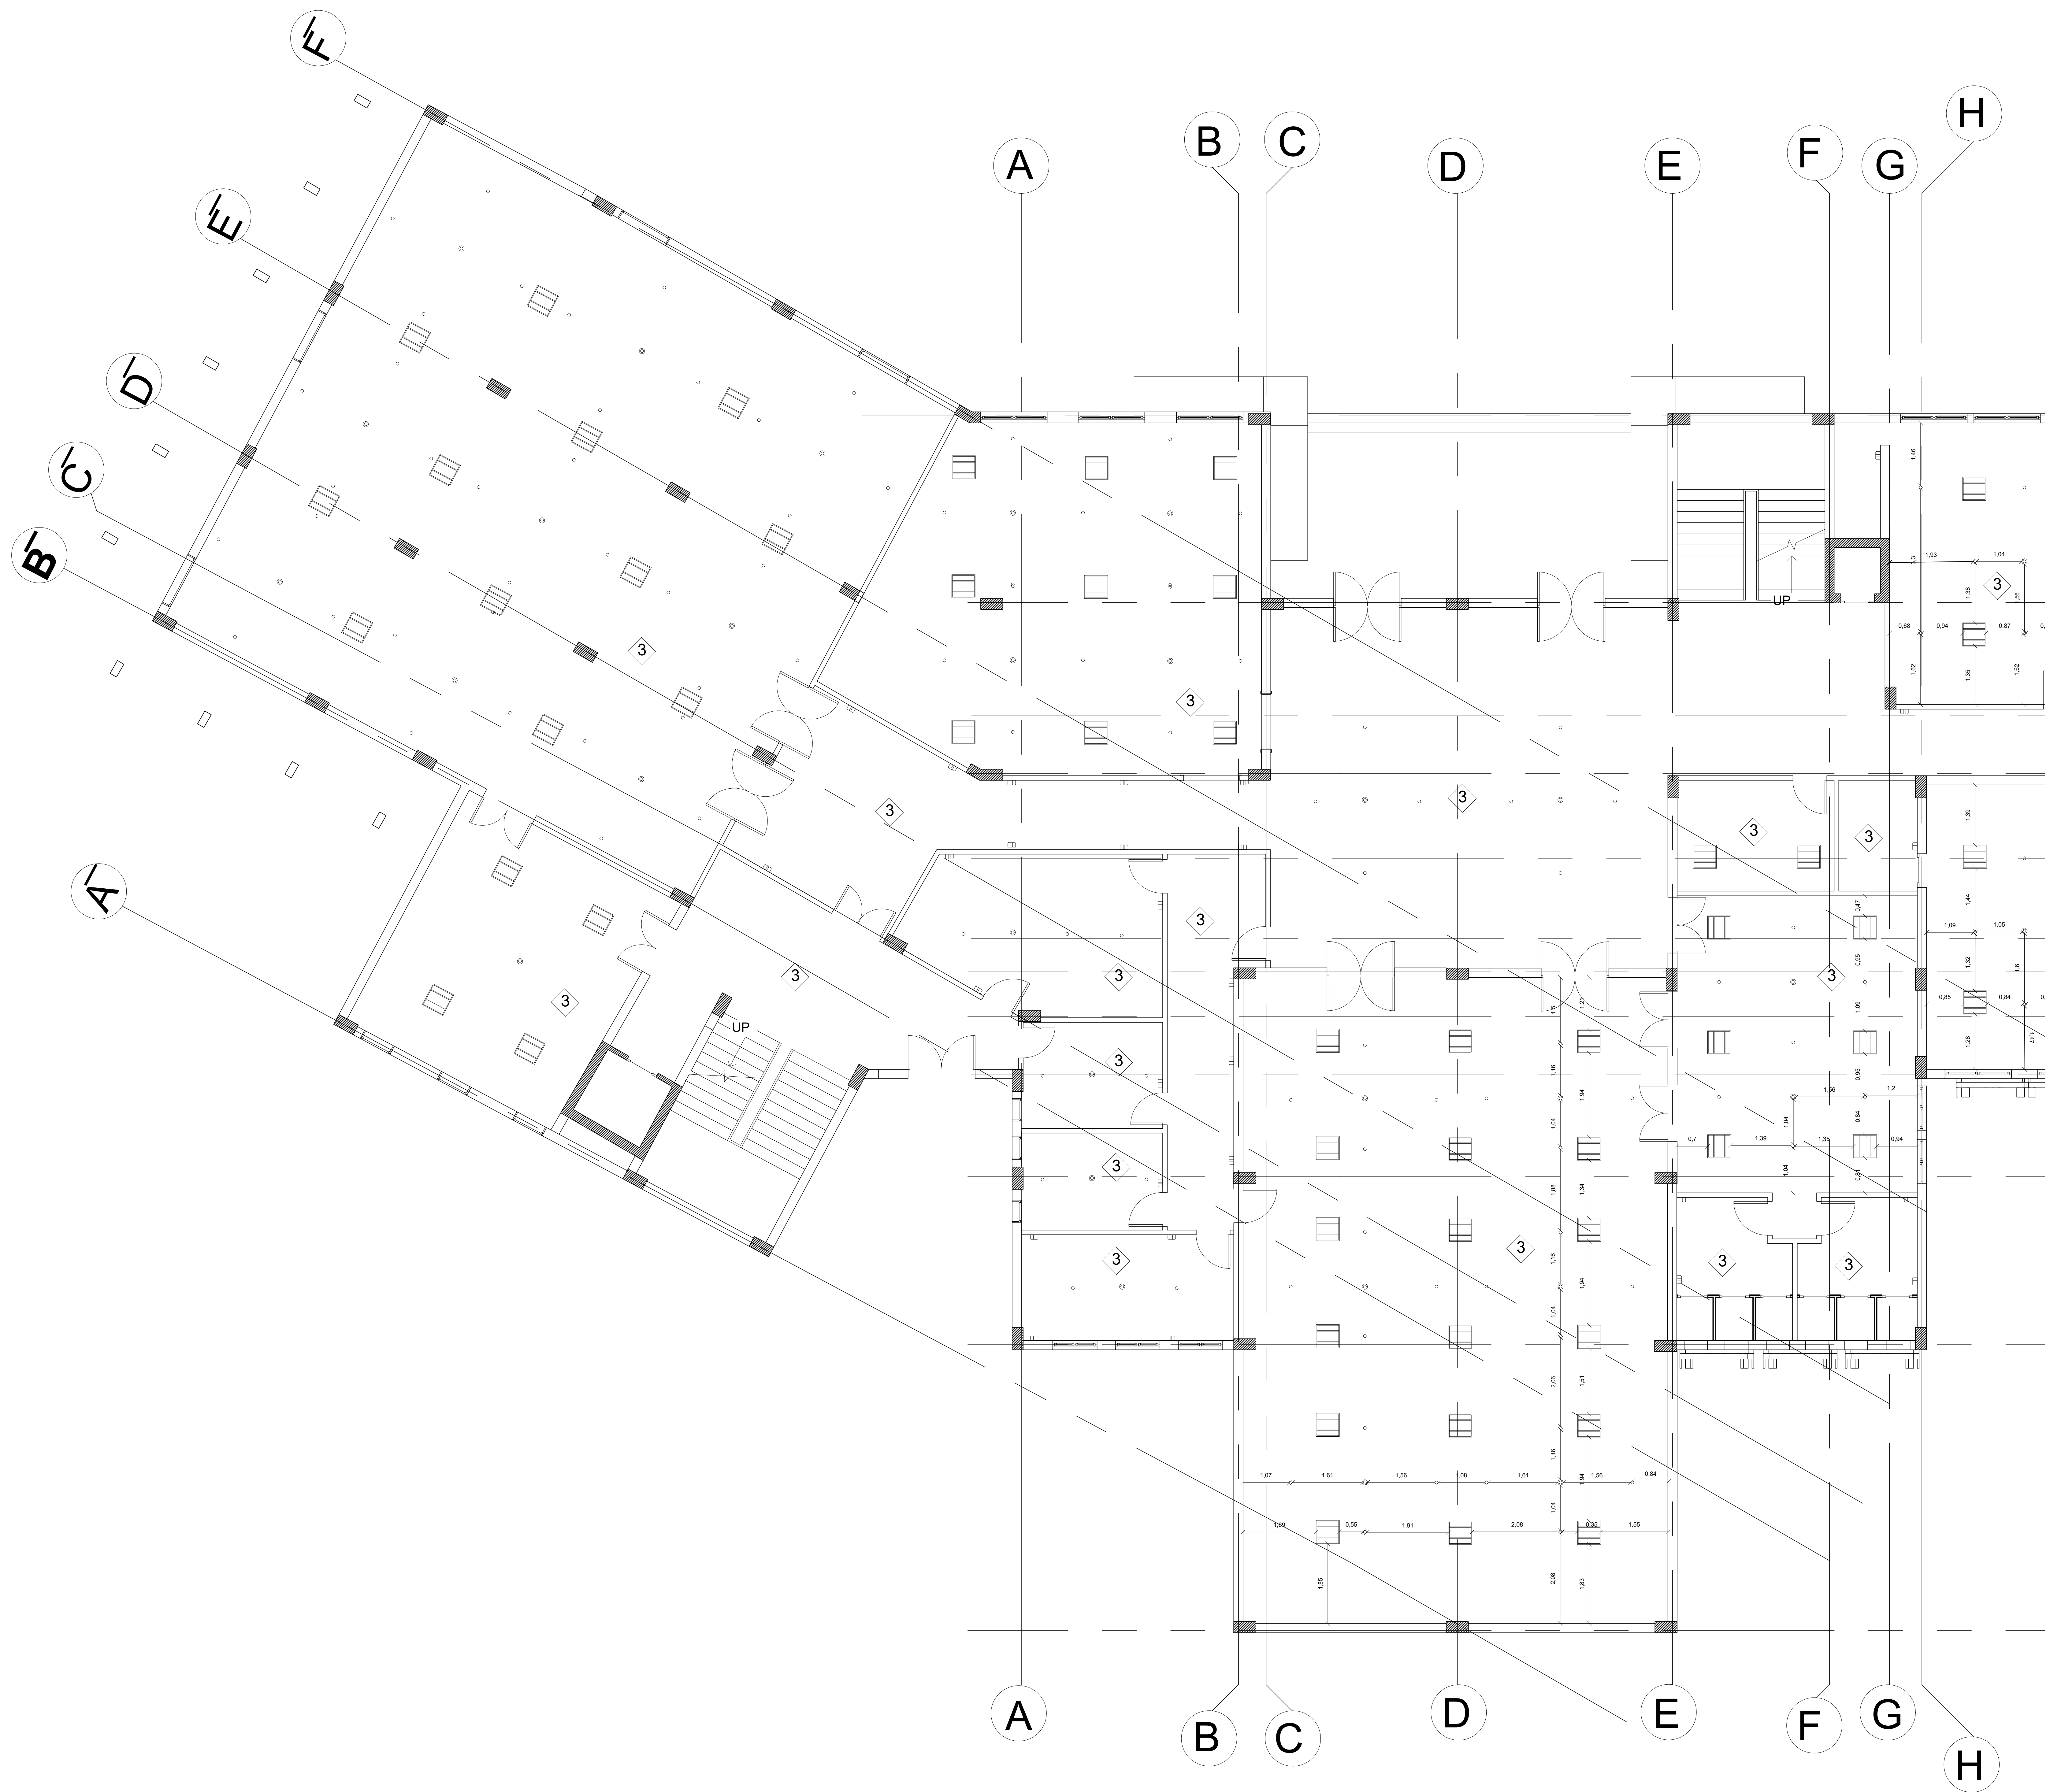


NORTH

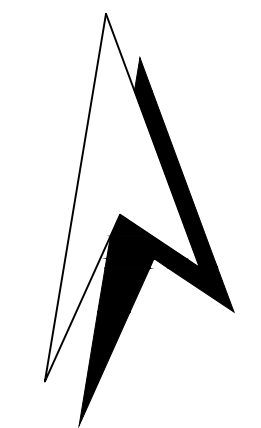

FINISHING TABLES :

CODE	TERM	STATMENT
○	pipe	PVC Rain stack RS
⊙	DRAG	Root drain RD
≡≡≡		GROUND SLOPE DIRECTION

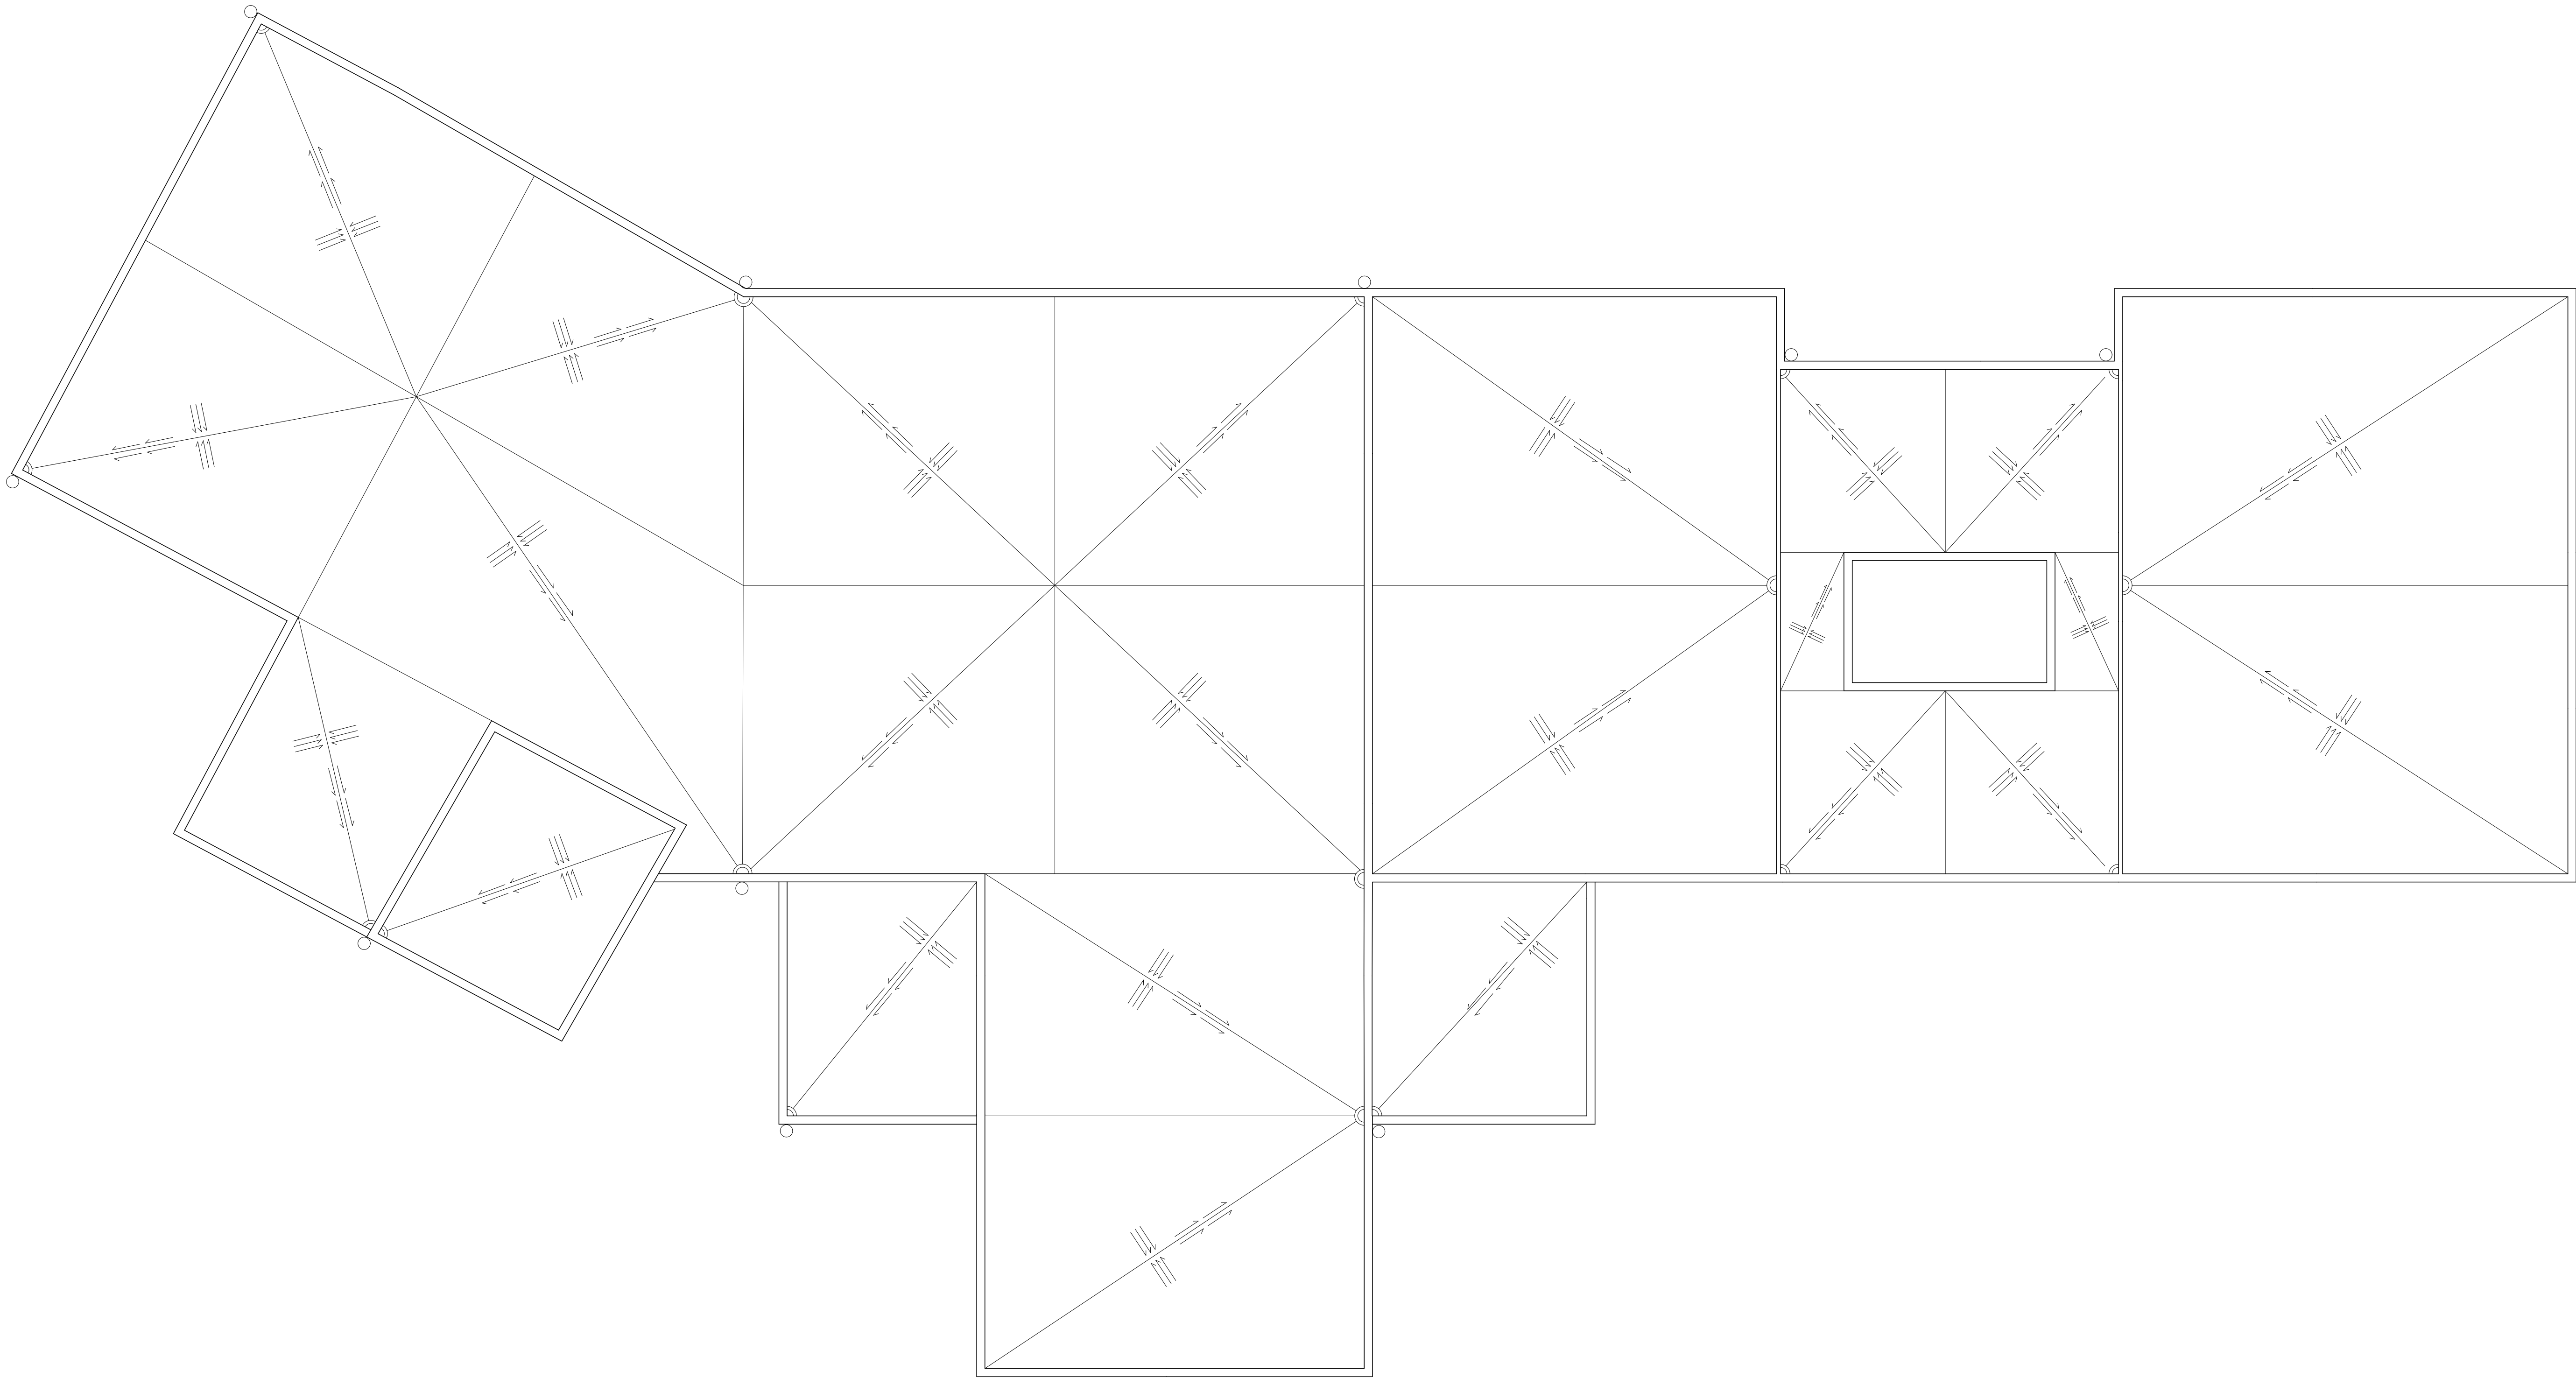


Abdul rahman Ashraf




DR. MOHAMED AISAEED

GROUND FLOOR
SCALE 1:50

NORTH

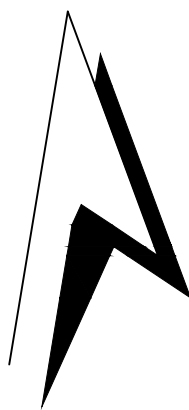

Abbreviation	Discrepion
H.W	hot water galvanized pipes
C.W	cold water galvanized pipes
F.D	floor drain
C.O	clean out
W.P	waste pipe (u.p.v.c)
S.P	soil pipes(u.p.v.c)
S.S	soil stack(u.p.v.c)10cm
W.S	waste stack (u.p.v.c)7.5cm
V.S	ventilation stack(u.p.v.c)5cm
G.T	gally trap
S.V	stop valve
W.H	electric water heater(10 liter)
I.C	inspection chamber

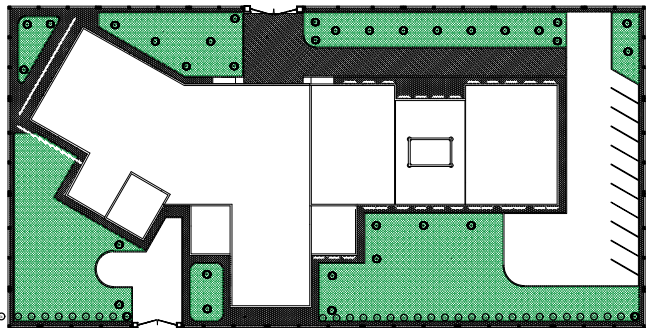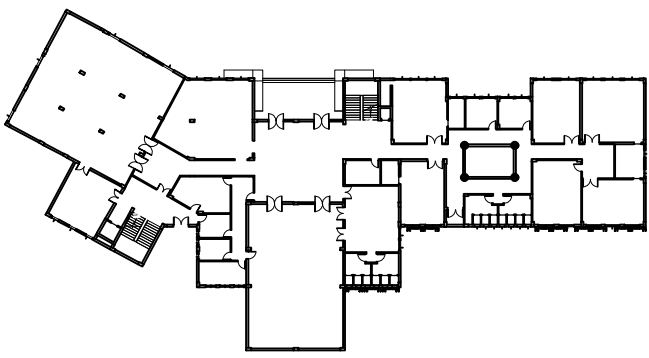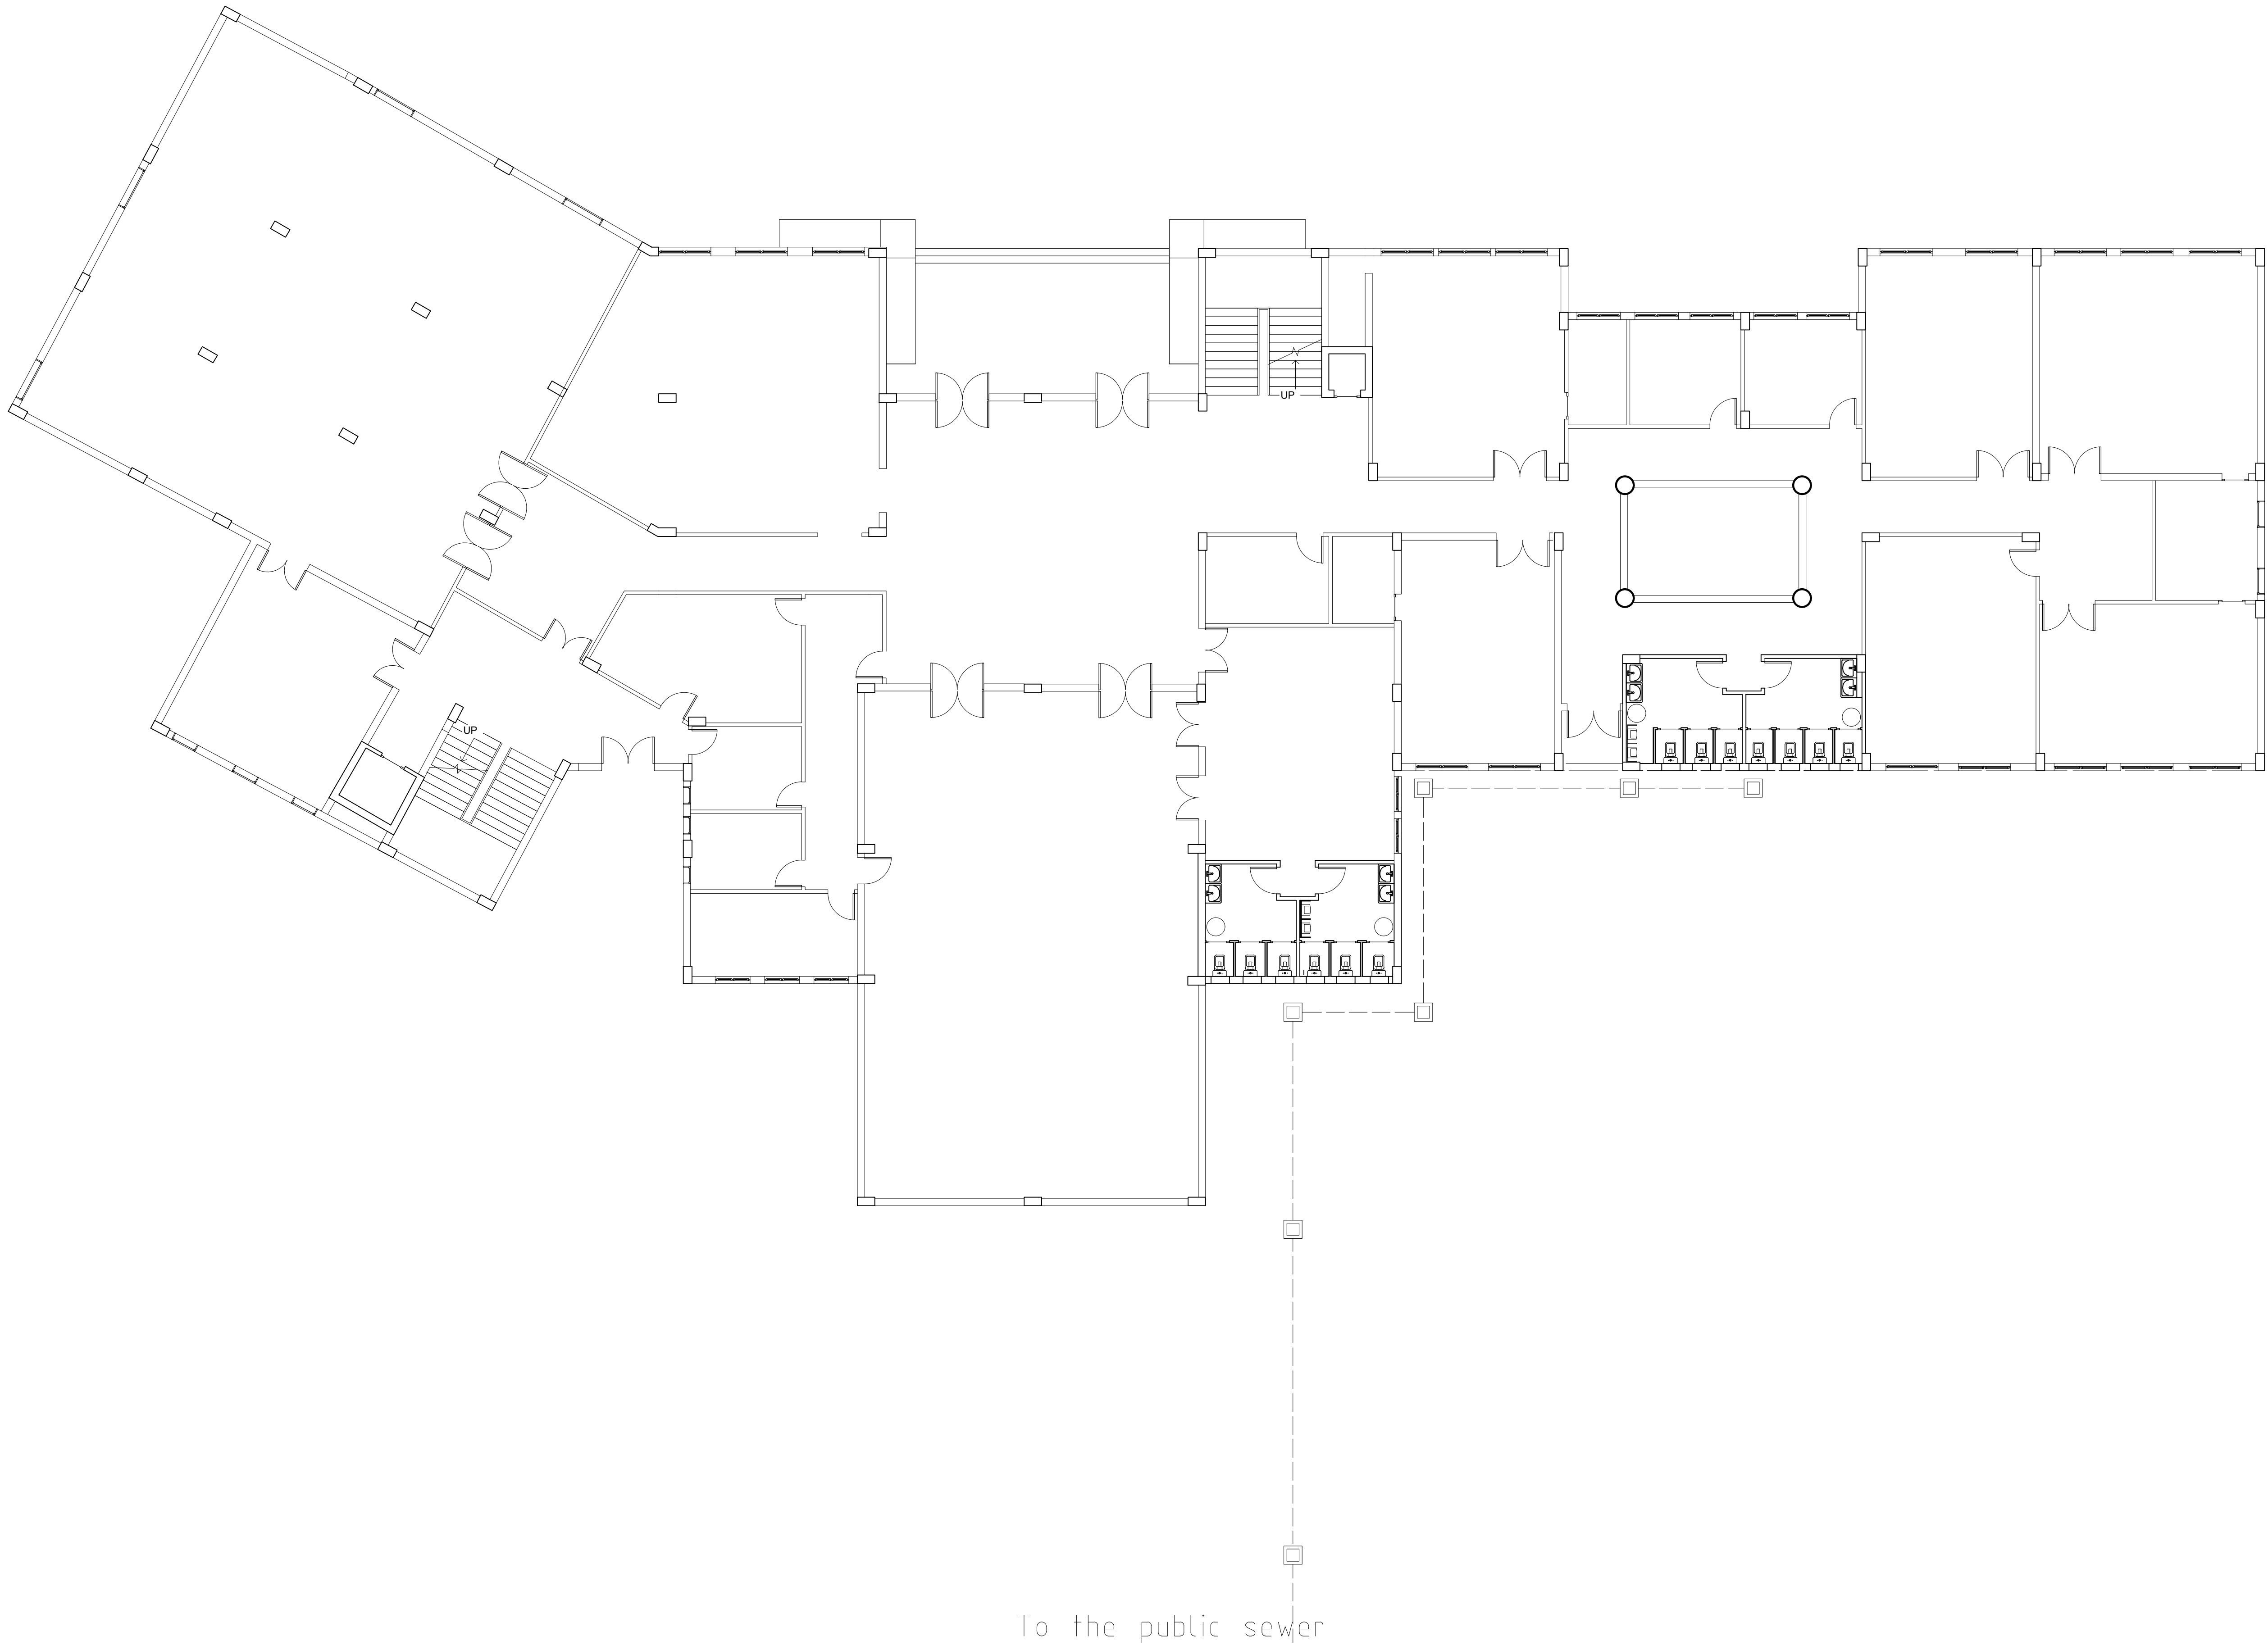


Abdul rahman Ashraf





DR. MOHAMED AISAEED

GROUND FLOOR
SCALE 1:50

NORTH

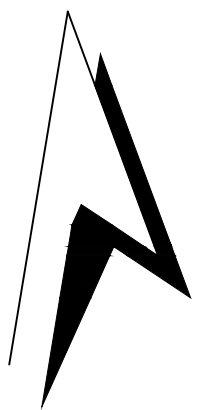


Abbreviation	Discrepion
H.W	hot water galvanized pipes
C.W	cold water galvanized pipes
F.D	floor drain
C.O	clean out
W.P	waste pipe (u.p.v.c)
S.P	soil pipes(u.p.v.c)
S.S	soil stack(u.p.v.c)10cm
W.S	waste stack (u.p.v.c)7.5cm
V.S	ventilation stack(u.p.v.c)5cm
G.T	gally trap
S.V	stop valve
W.H	electric water heater(10 liter)
I.C	inspection chamber

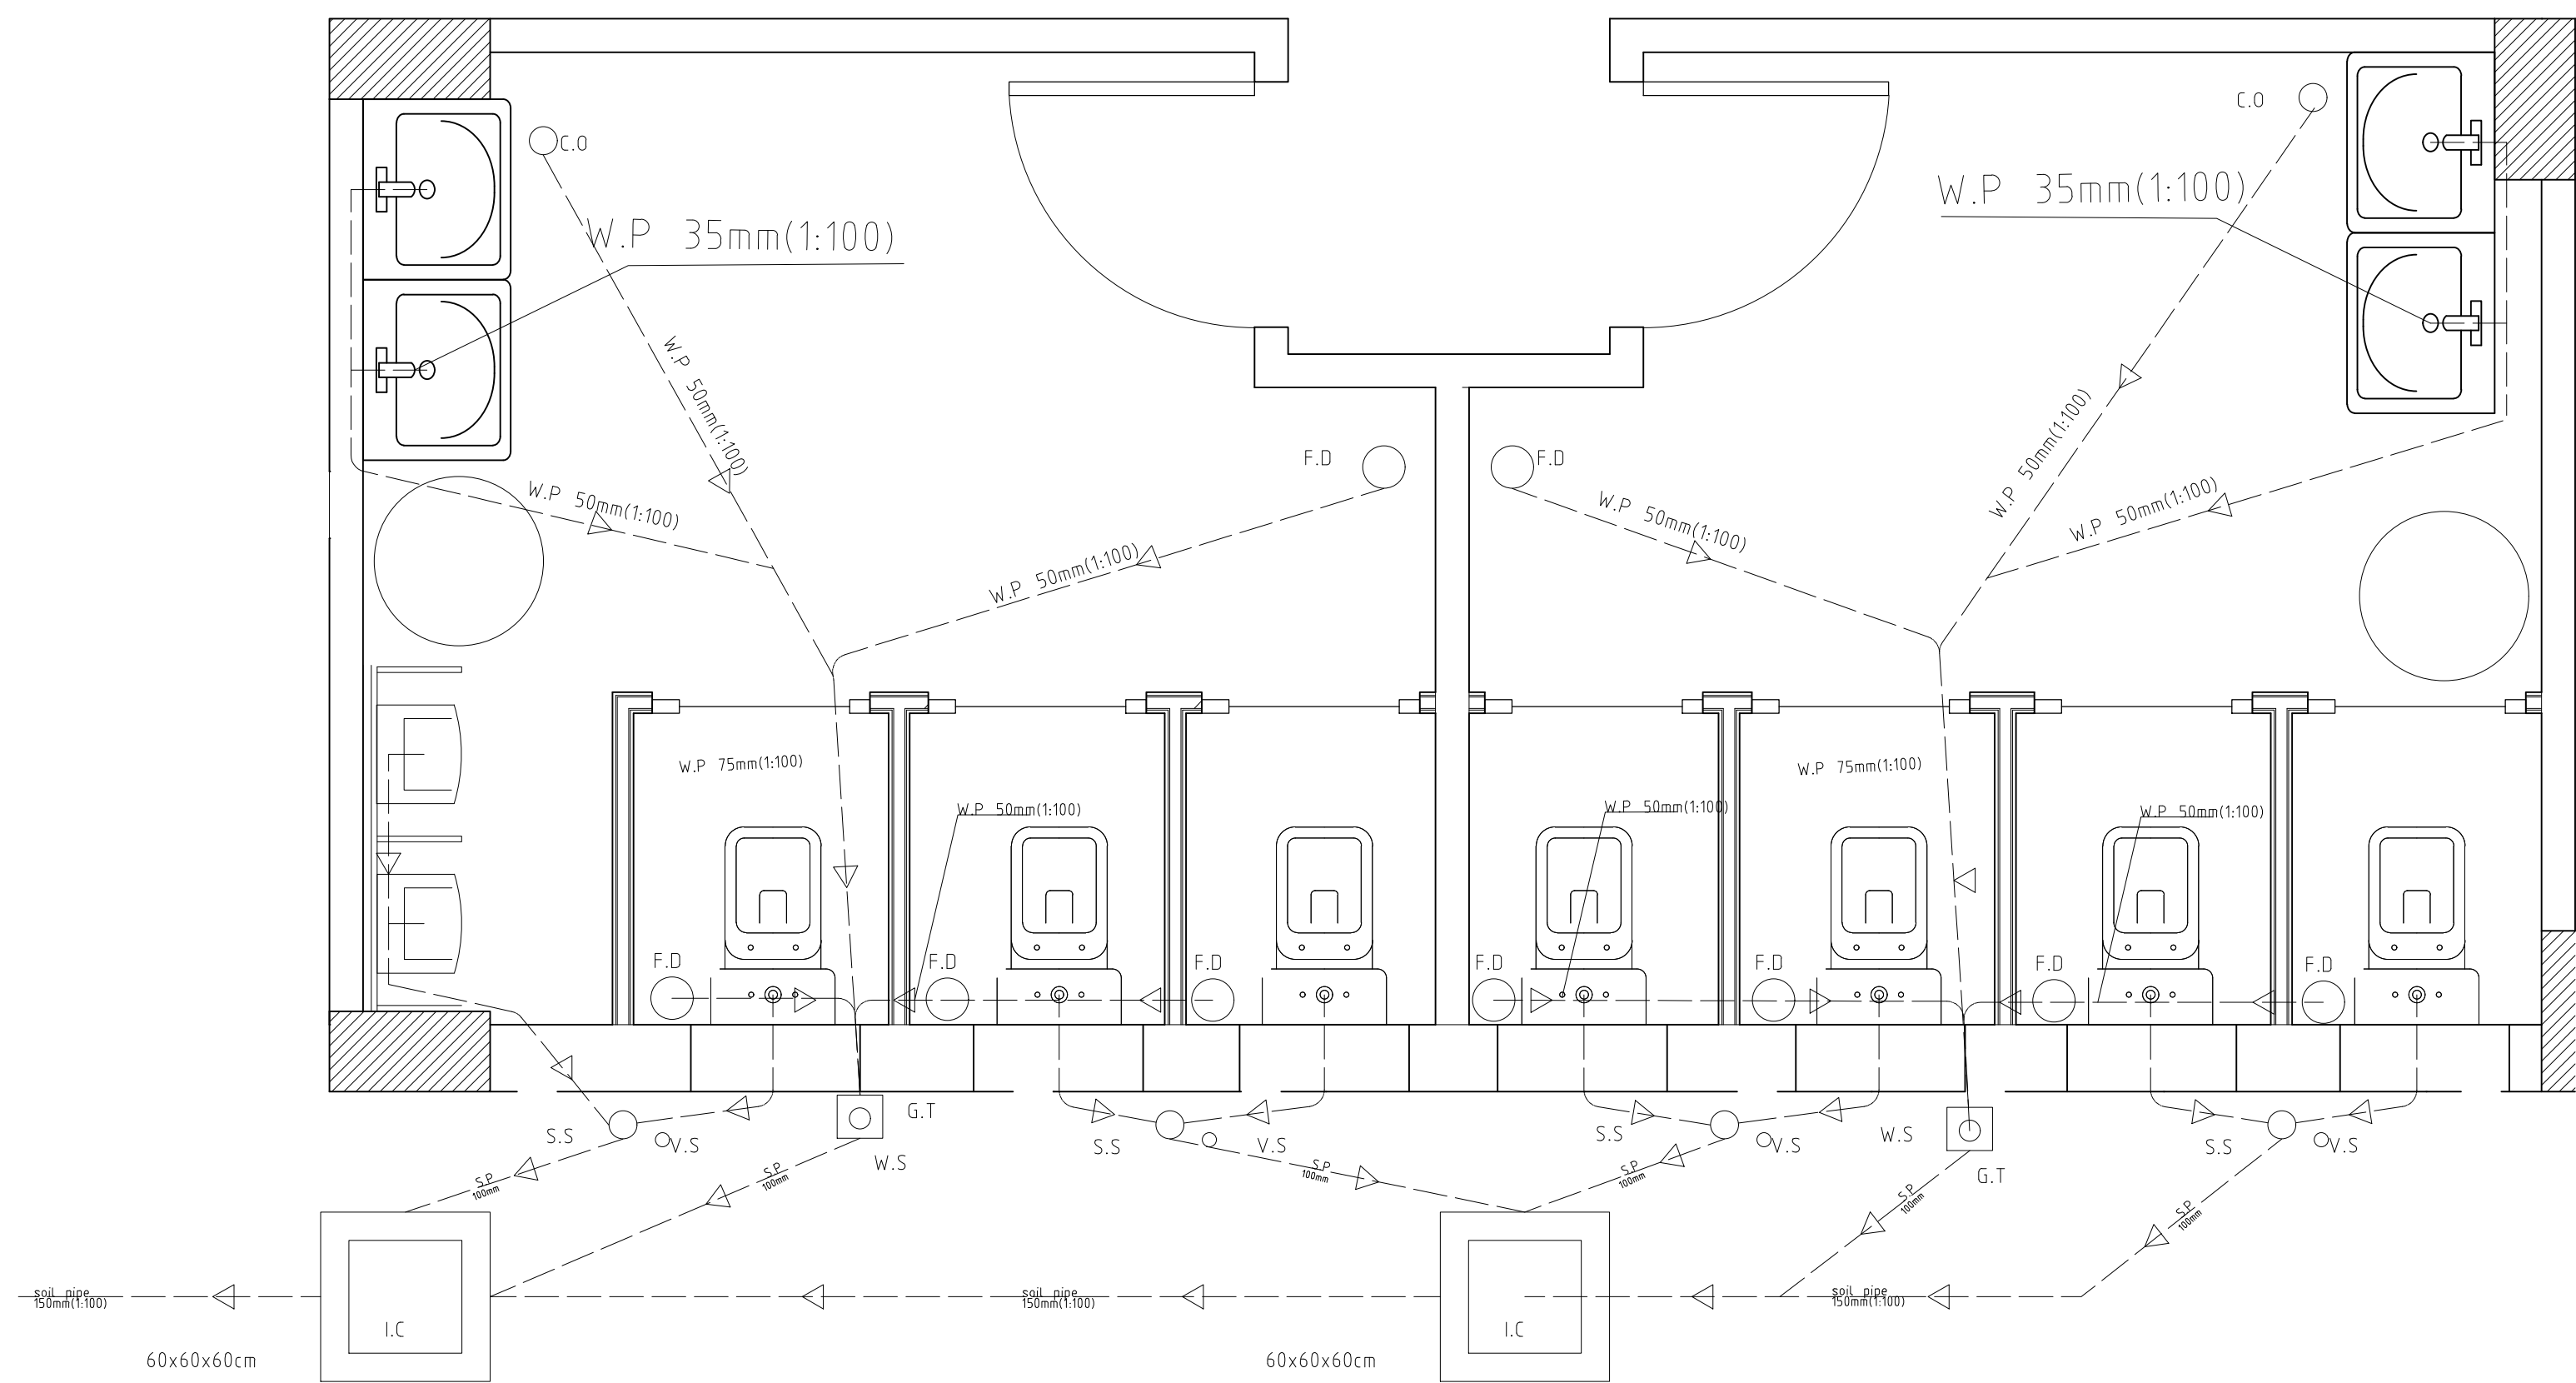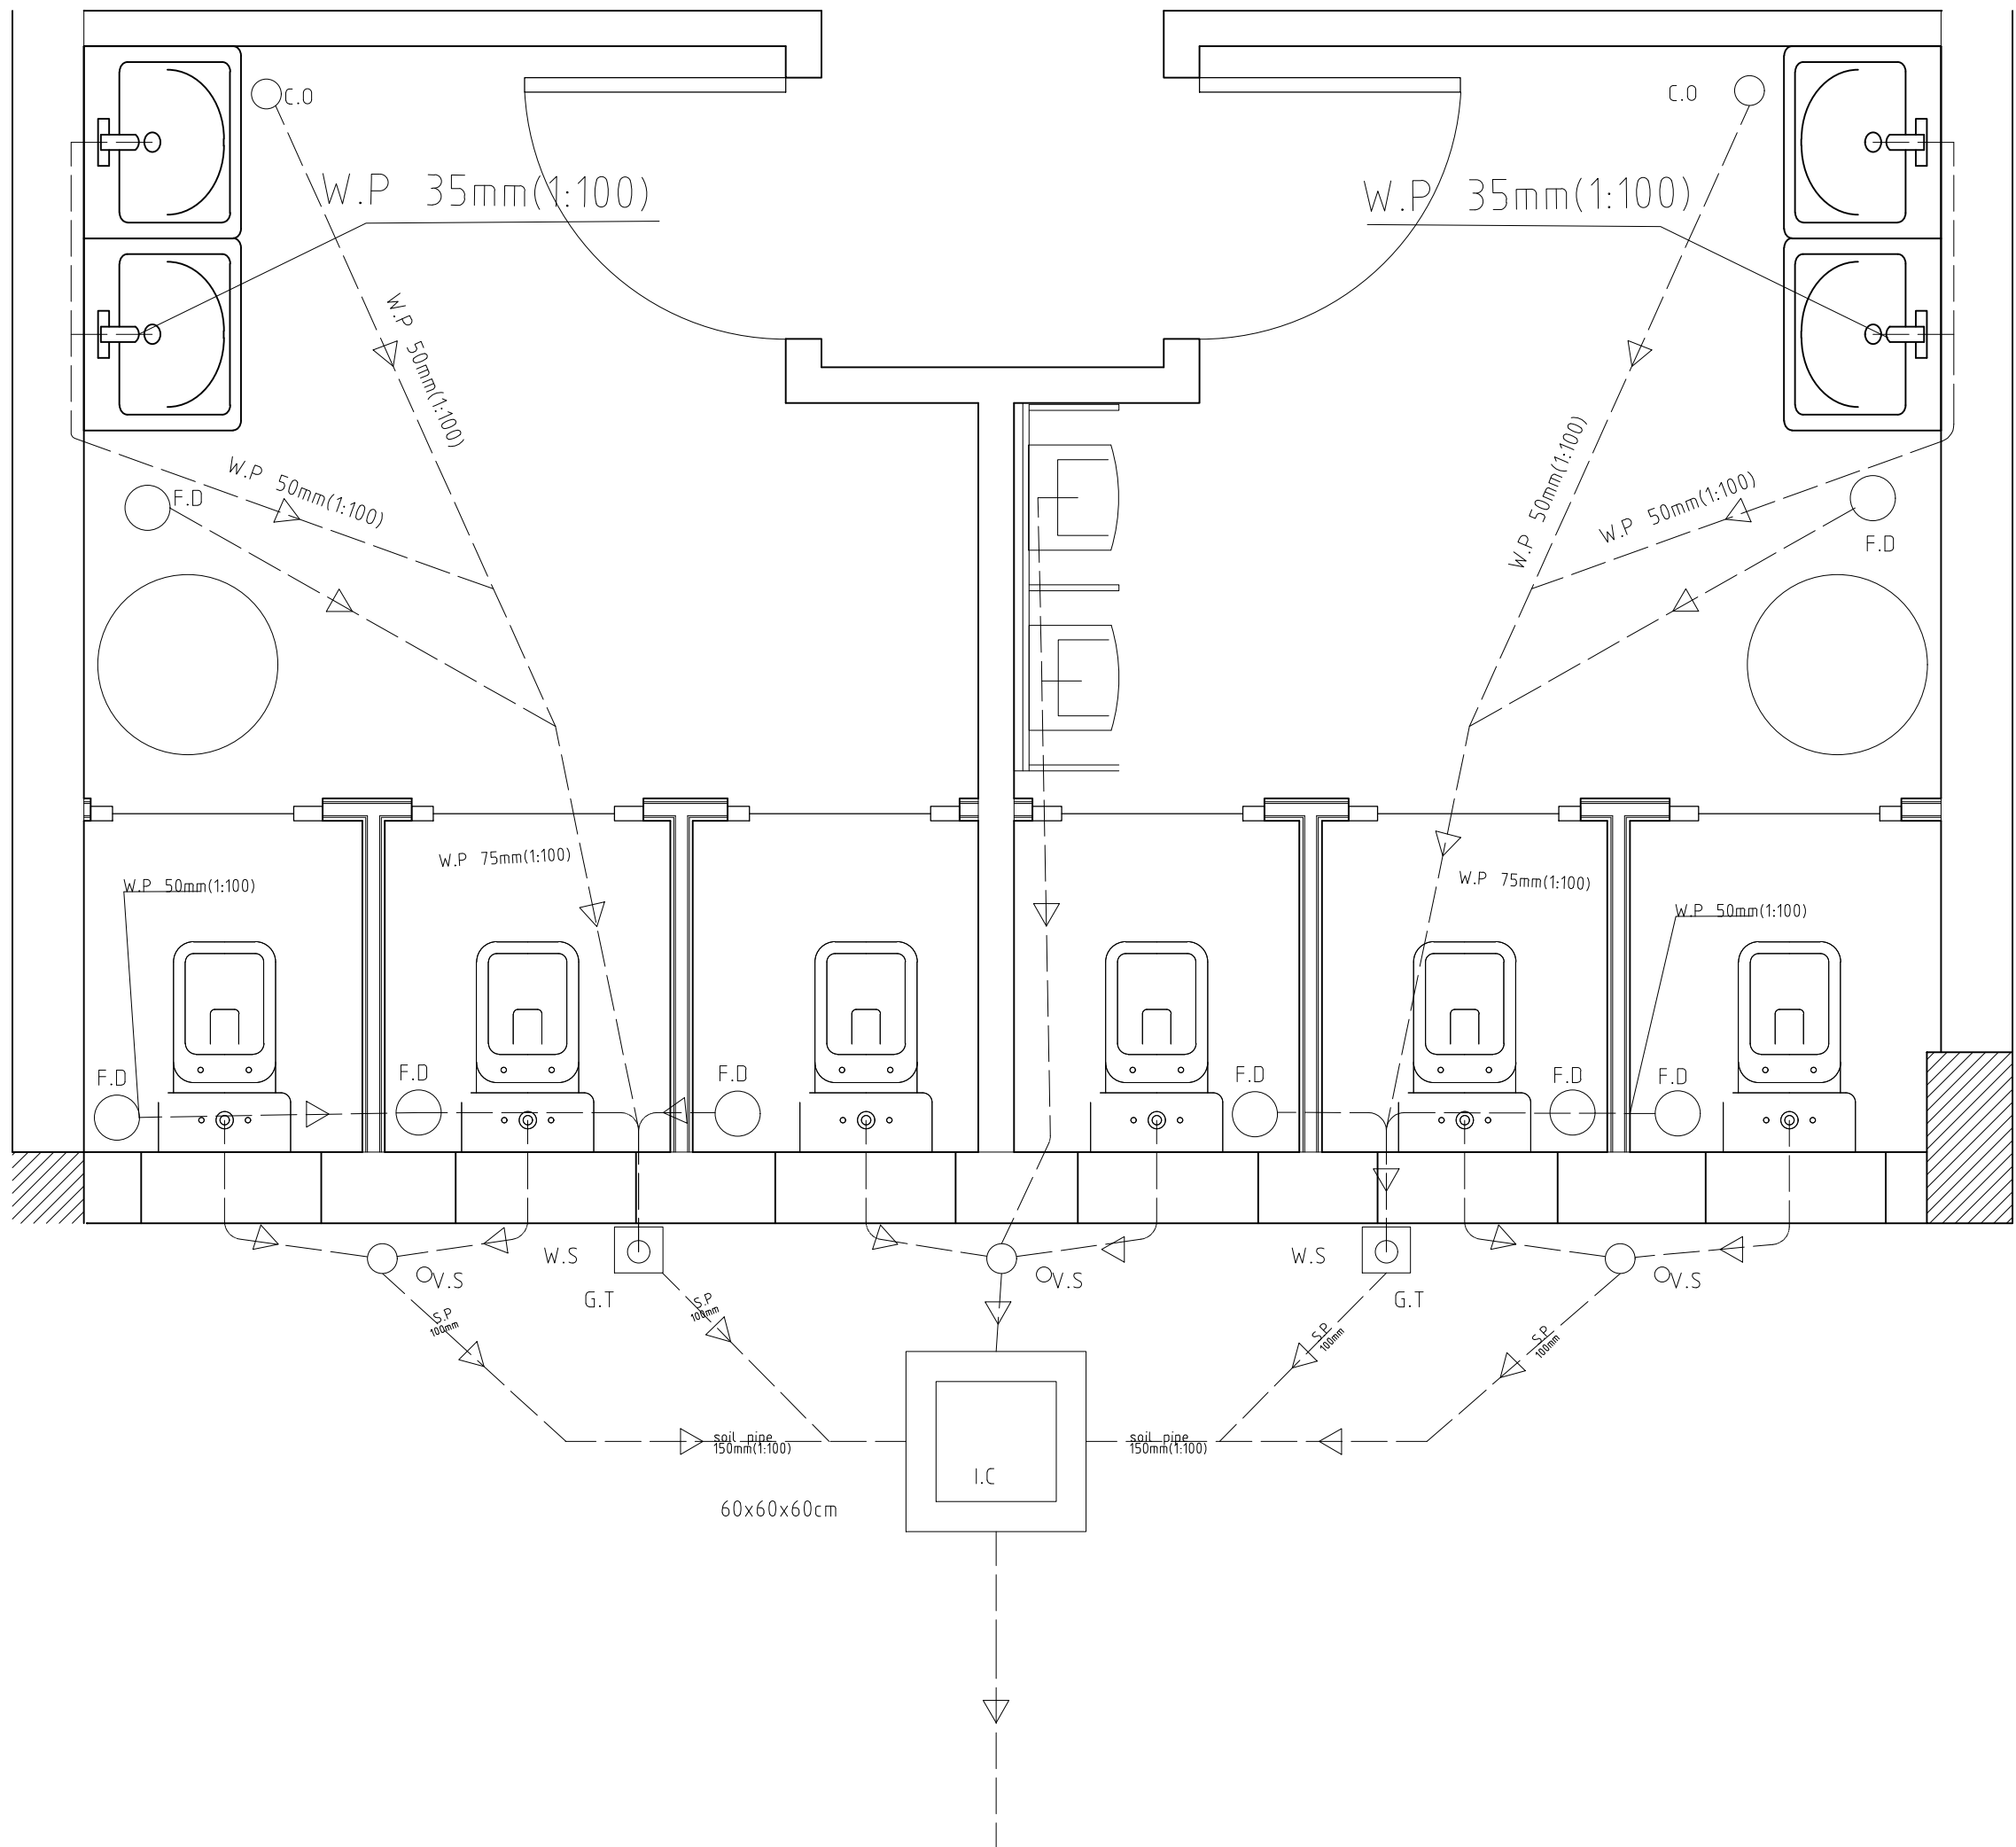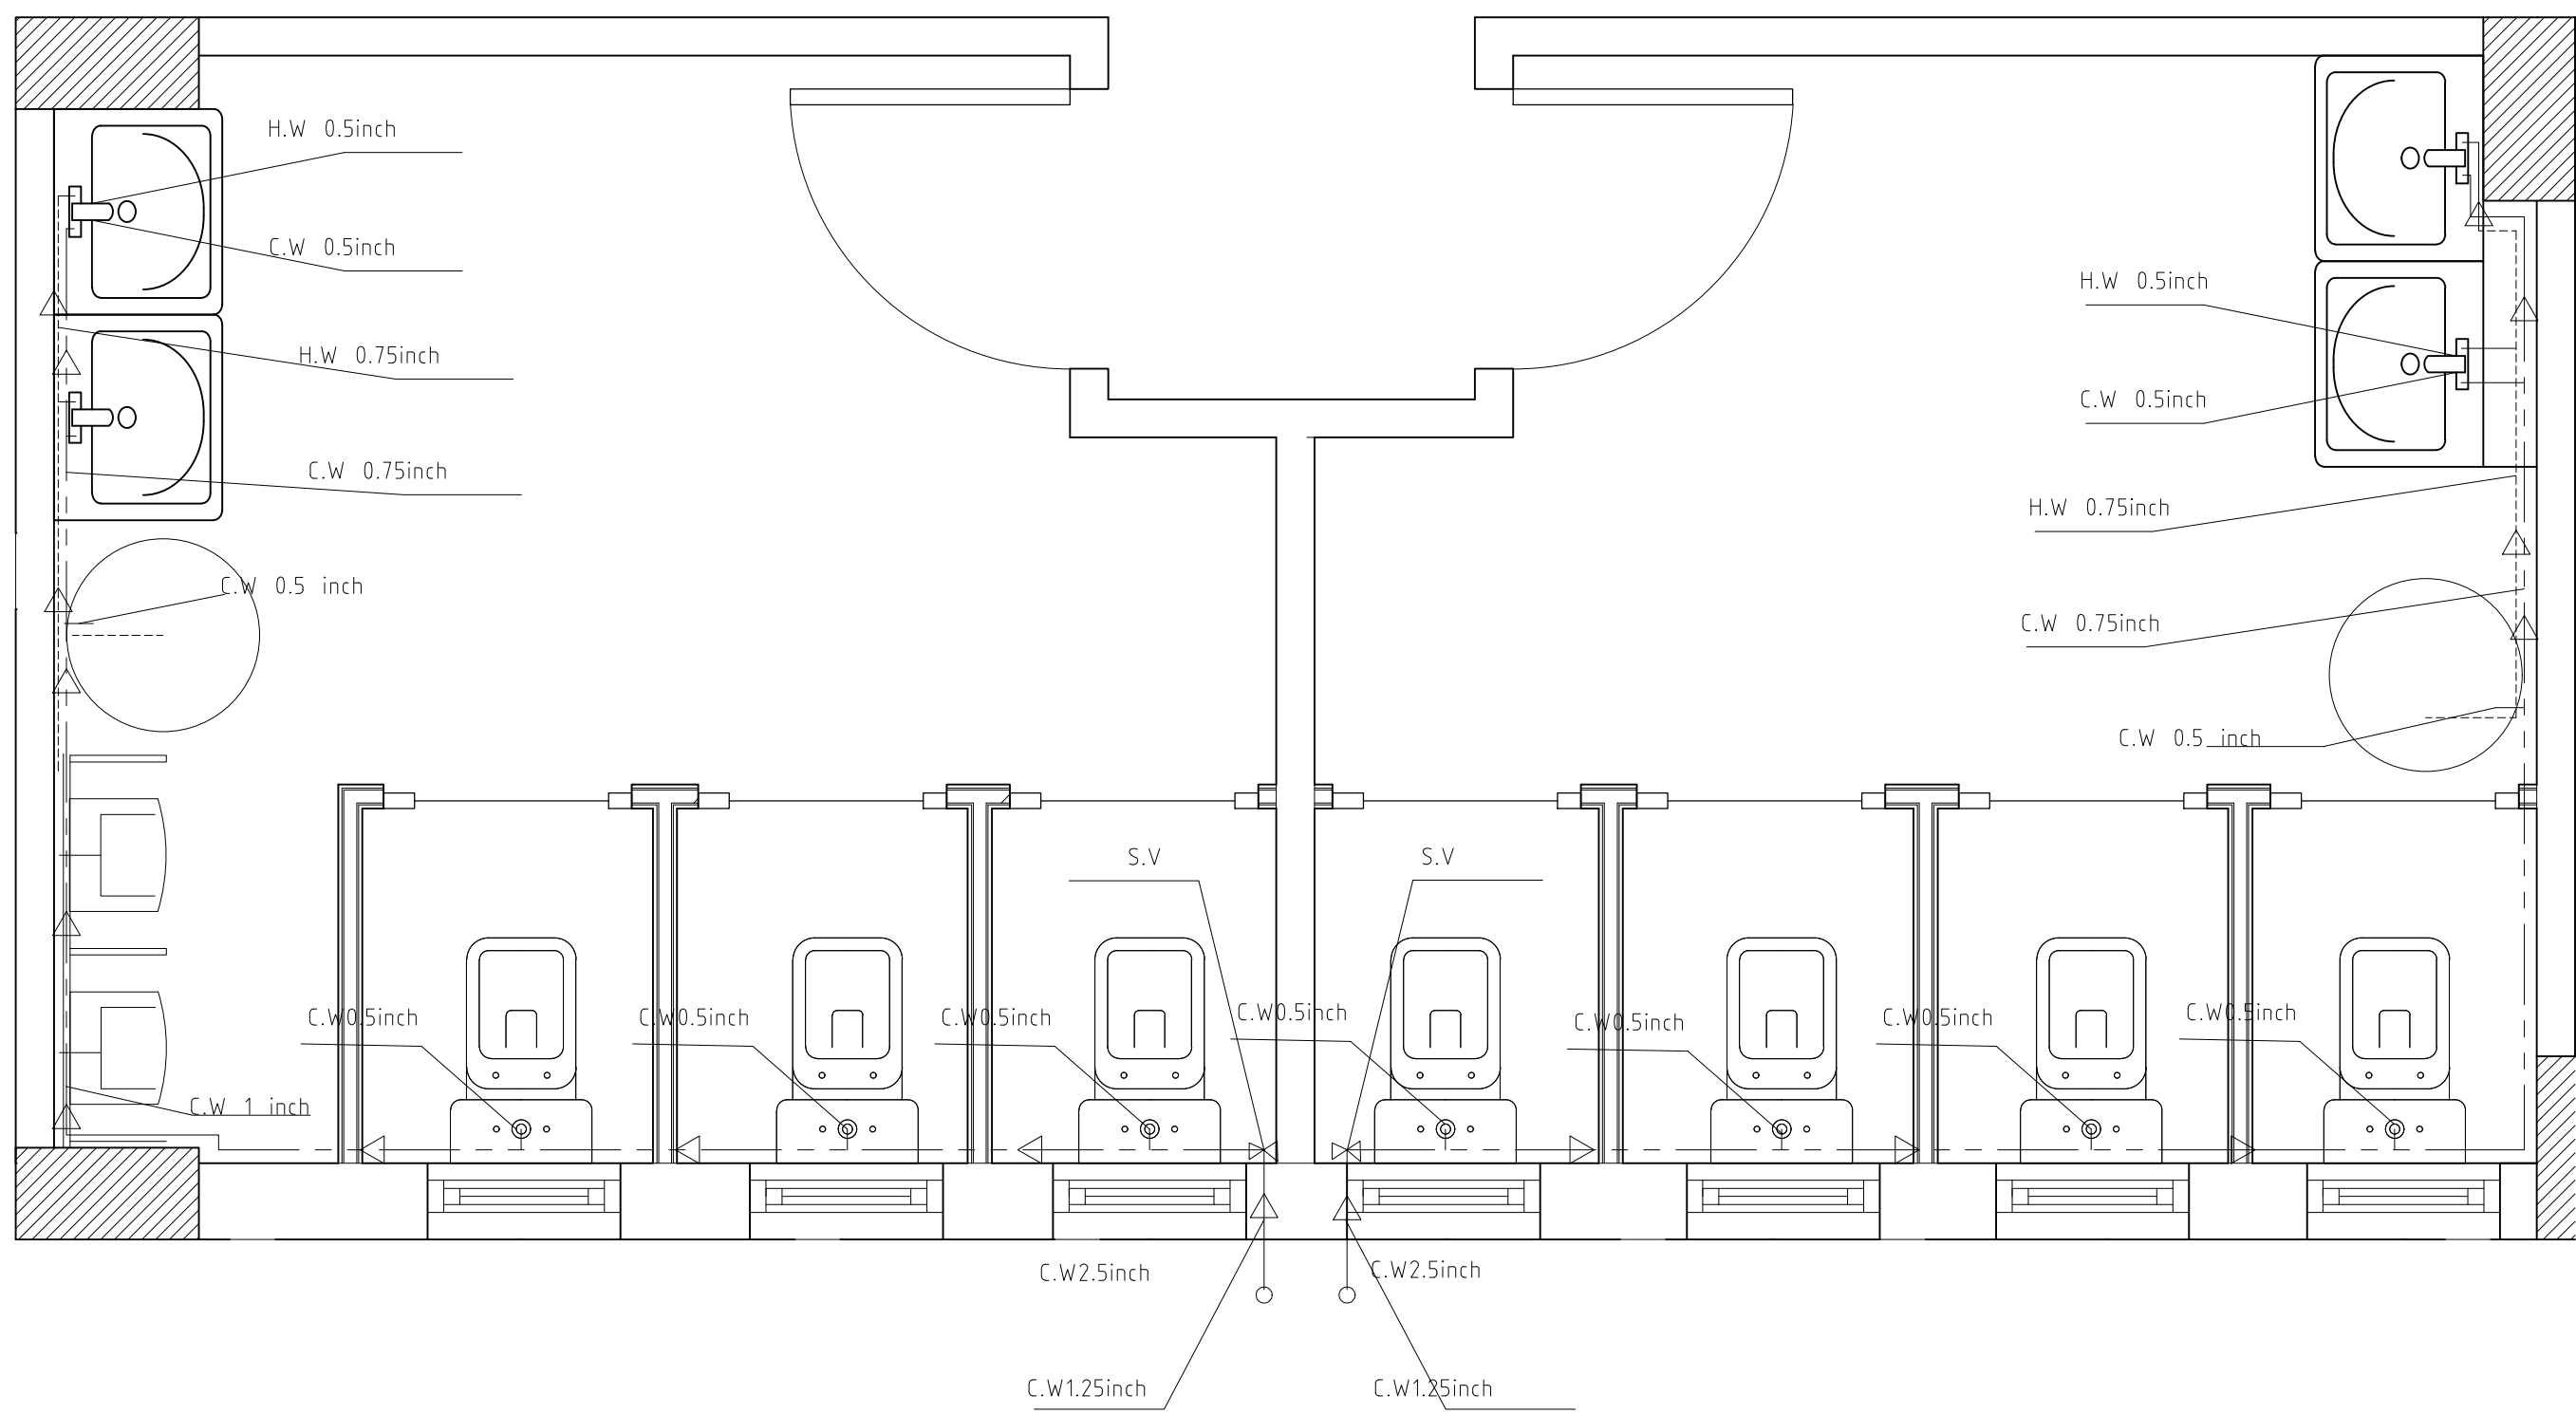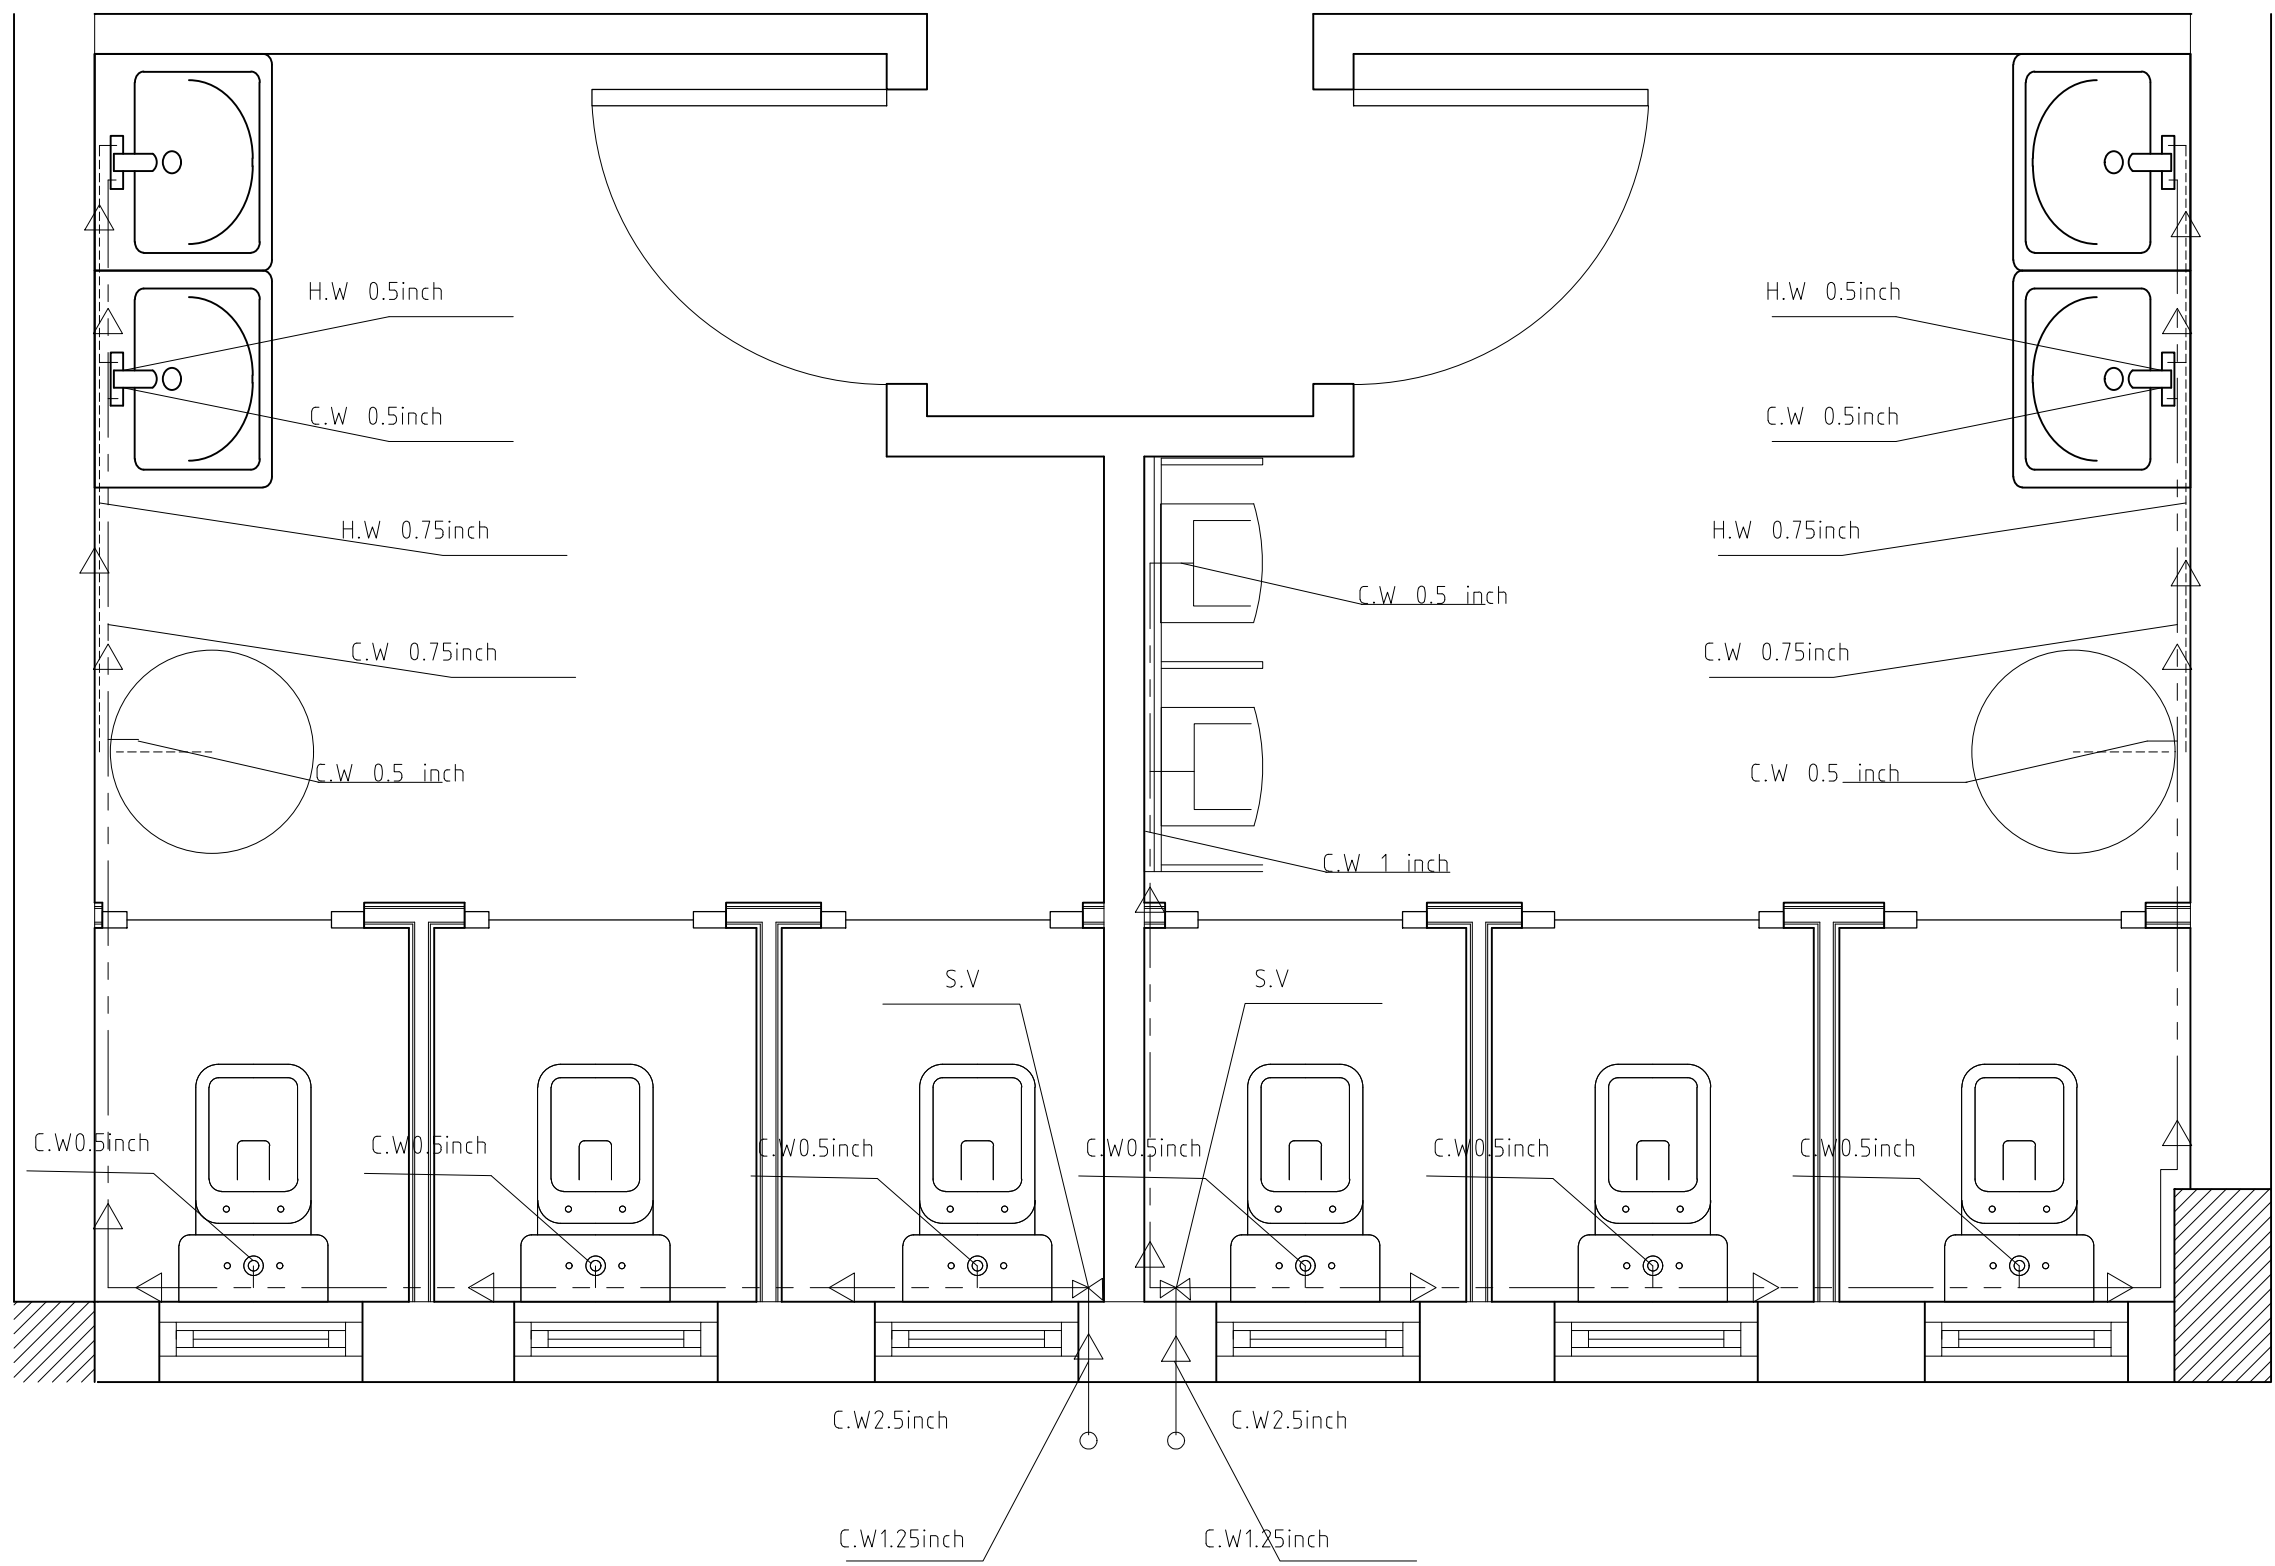

Abdul rahman Ashraf

DR. MOHAMED AISAEED

GROUND FLOOR
SCALE 1:50

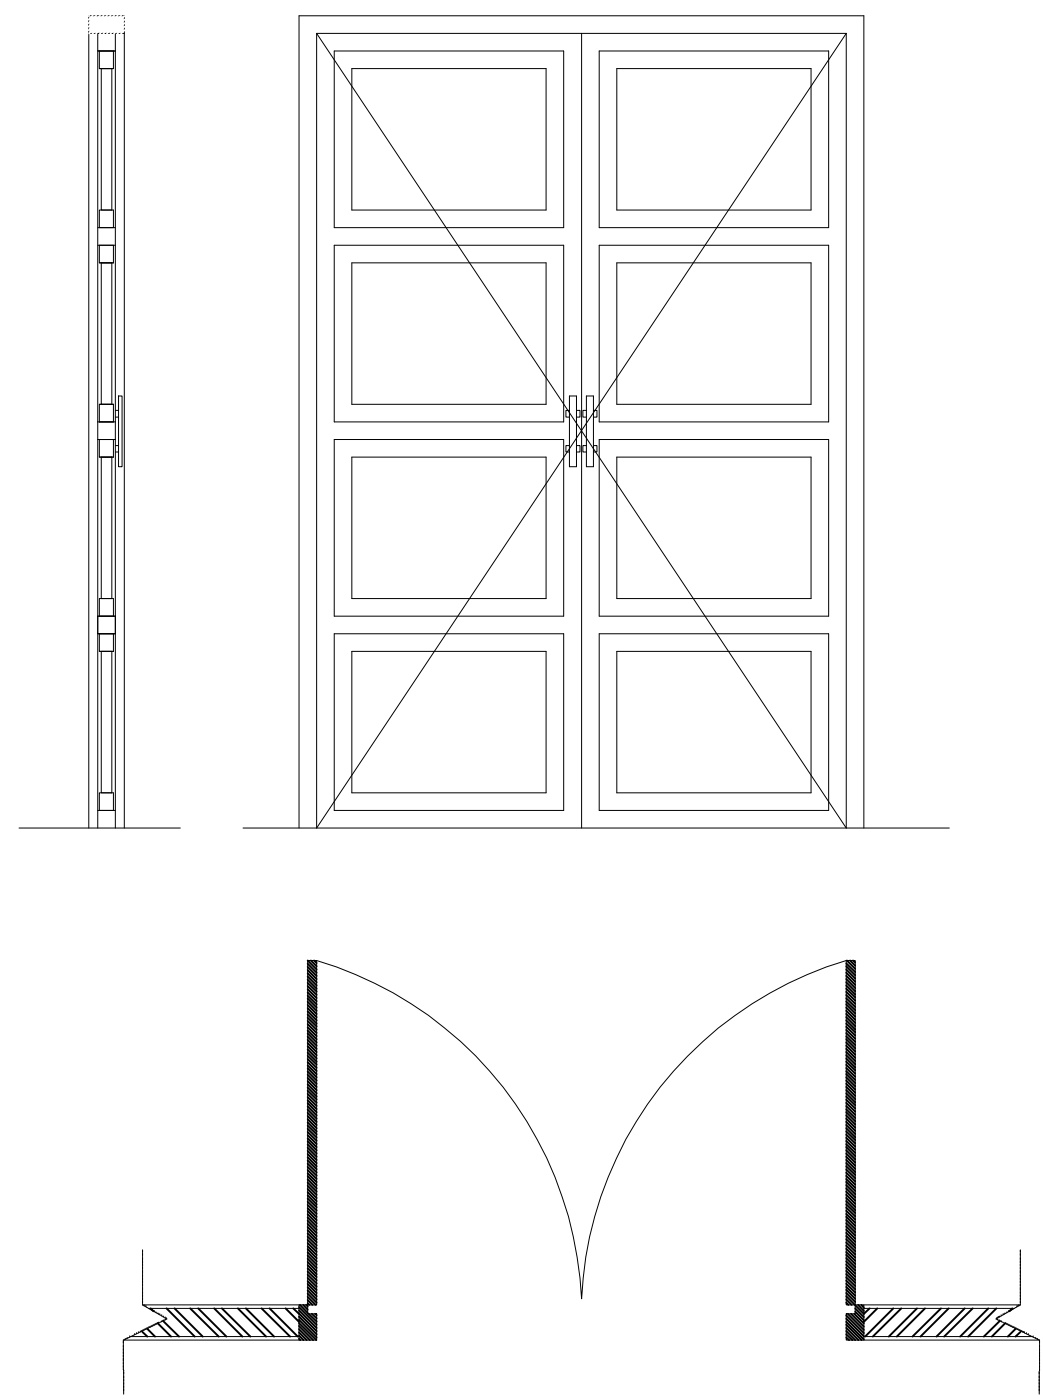

name: D1


location: halls' entrance

numbers: 14

hight: 2.2

width: 1.7

hinged door
with wooden frame and
pine
hollow flush
two leaves

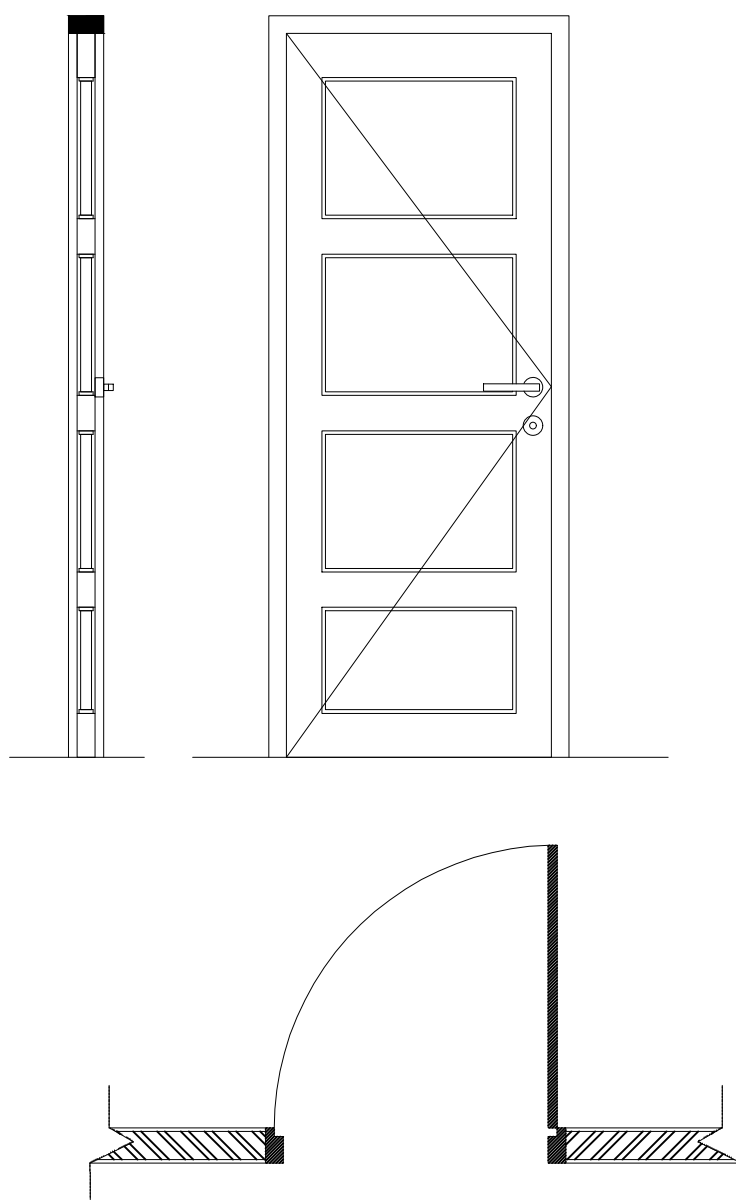

name: D4


location: office entrance

numbers: 16

hight: 2.2

width: 0.9

hinged door
with wooden frame and
pine
hollow flush
one leave

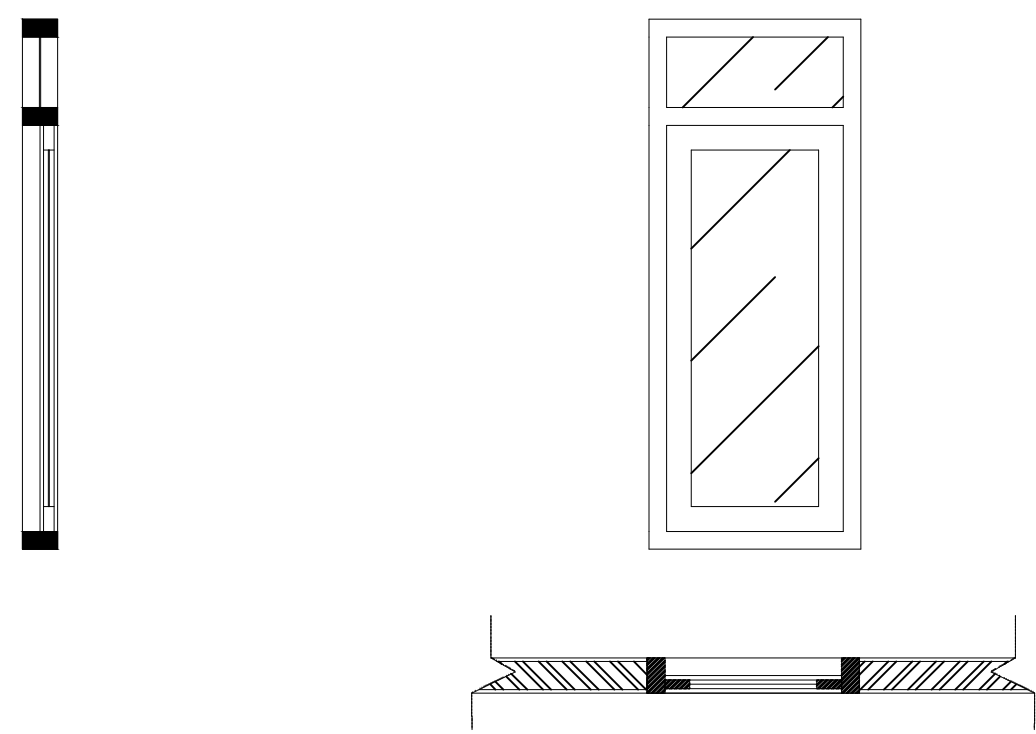

name: W3

location: bathrooms

numbers: 16

hight: 1

width: 0.6

sill hight: 1.4

hinged window
with aluminum frame and
pine
with glass sustem
aluminum frame holding
6mm clear glass

Door schedule				
type mark	count	width	Height	Description
D1	14	1.70m	2.2m	hinged door two sides wooden laminated
D2	4	1.70m	2.2m	hinged door two sides aluminum and glass system
D3	13	0.80m	2.2m	hinged door one side corlar clading suiting partitions
D4	16	0.90m	2.2m	hinged door one side wooden laminated

Window schedule					
type mark	count	width	Height	sill Height	Description
W1	14	1.2m	1.50m	1m	fixed one sidesaluminum and glass system
W2	18	1.7m	1.50m	1m	hinged two sides aluminum and glass system
W3	16	0.6m	1m	1.4m	hinged one side aluminum and glass system

